




Gesamte Konstruktion ist Roh				
A		Befestigung Modulisch geändert		P.Koch
B		Ergänzungen für Befestigung Modulisch		P.Koch
INDEX		ANORDNUNG GEWÄHRUNG		HAUSE

MAUCHLE

Stahlbau

Industriestrasse 9 - CH-6210 Sursee - T +41 41 925 12 51 - info@mauchle-stahlbau.ch

Auftrag:		24027		BAUHERR	
Zeichner:		P.Koch		Axpo Solutions AG	
		Interne Kontrolle		BAUSTELLE	
ABTEILUNG		UNTERSCHRIFT		NalpSolar	
				BENENNUNG	
				Primärkonstruktion Typ C	
				Typ 2026	
PL		J. Mäder		Ansicht, Schnitt & Details	
				ZEICHNUNGSPERSON	
MASSSTAB		1:10	1:20	1:50	24027 S O M 010 B
ANSICHT		 		PROJEKT TITELBLATT FOLGENZUSAMMENHANG BESCHÜBUNG	

SEHR WICHTIG! DIESE ZEICHNUNG IST UNTER BESTEHENDE IDENTIFIKATION UND DARP NICHT OHNE UNTERRE GENEHMIGUNG VERWENDET WERDEN! SONST KÖNNEN DRITTE PERSONEN ZUSÄTZLICHE VERANTWORTUNG TRAGEN!