
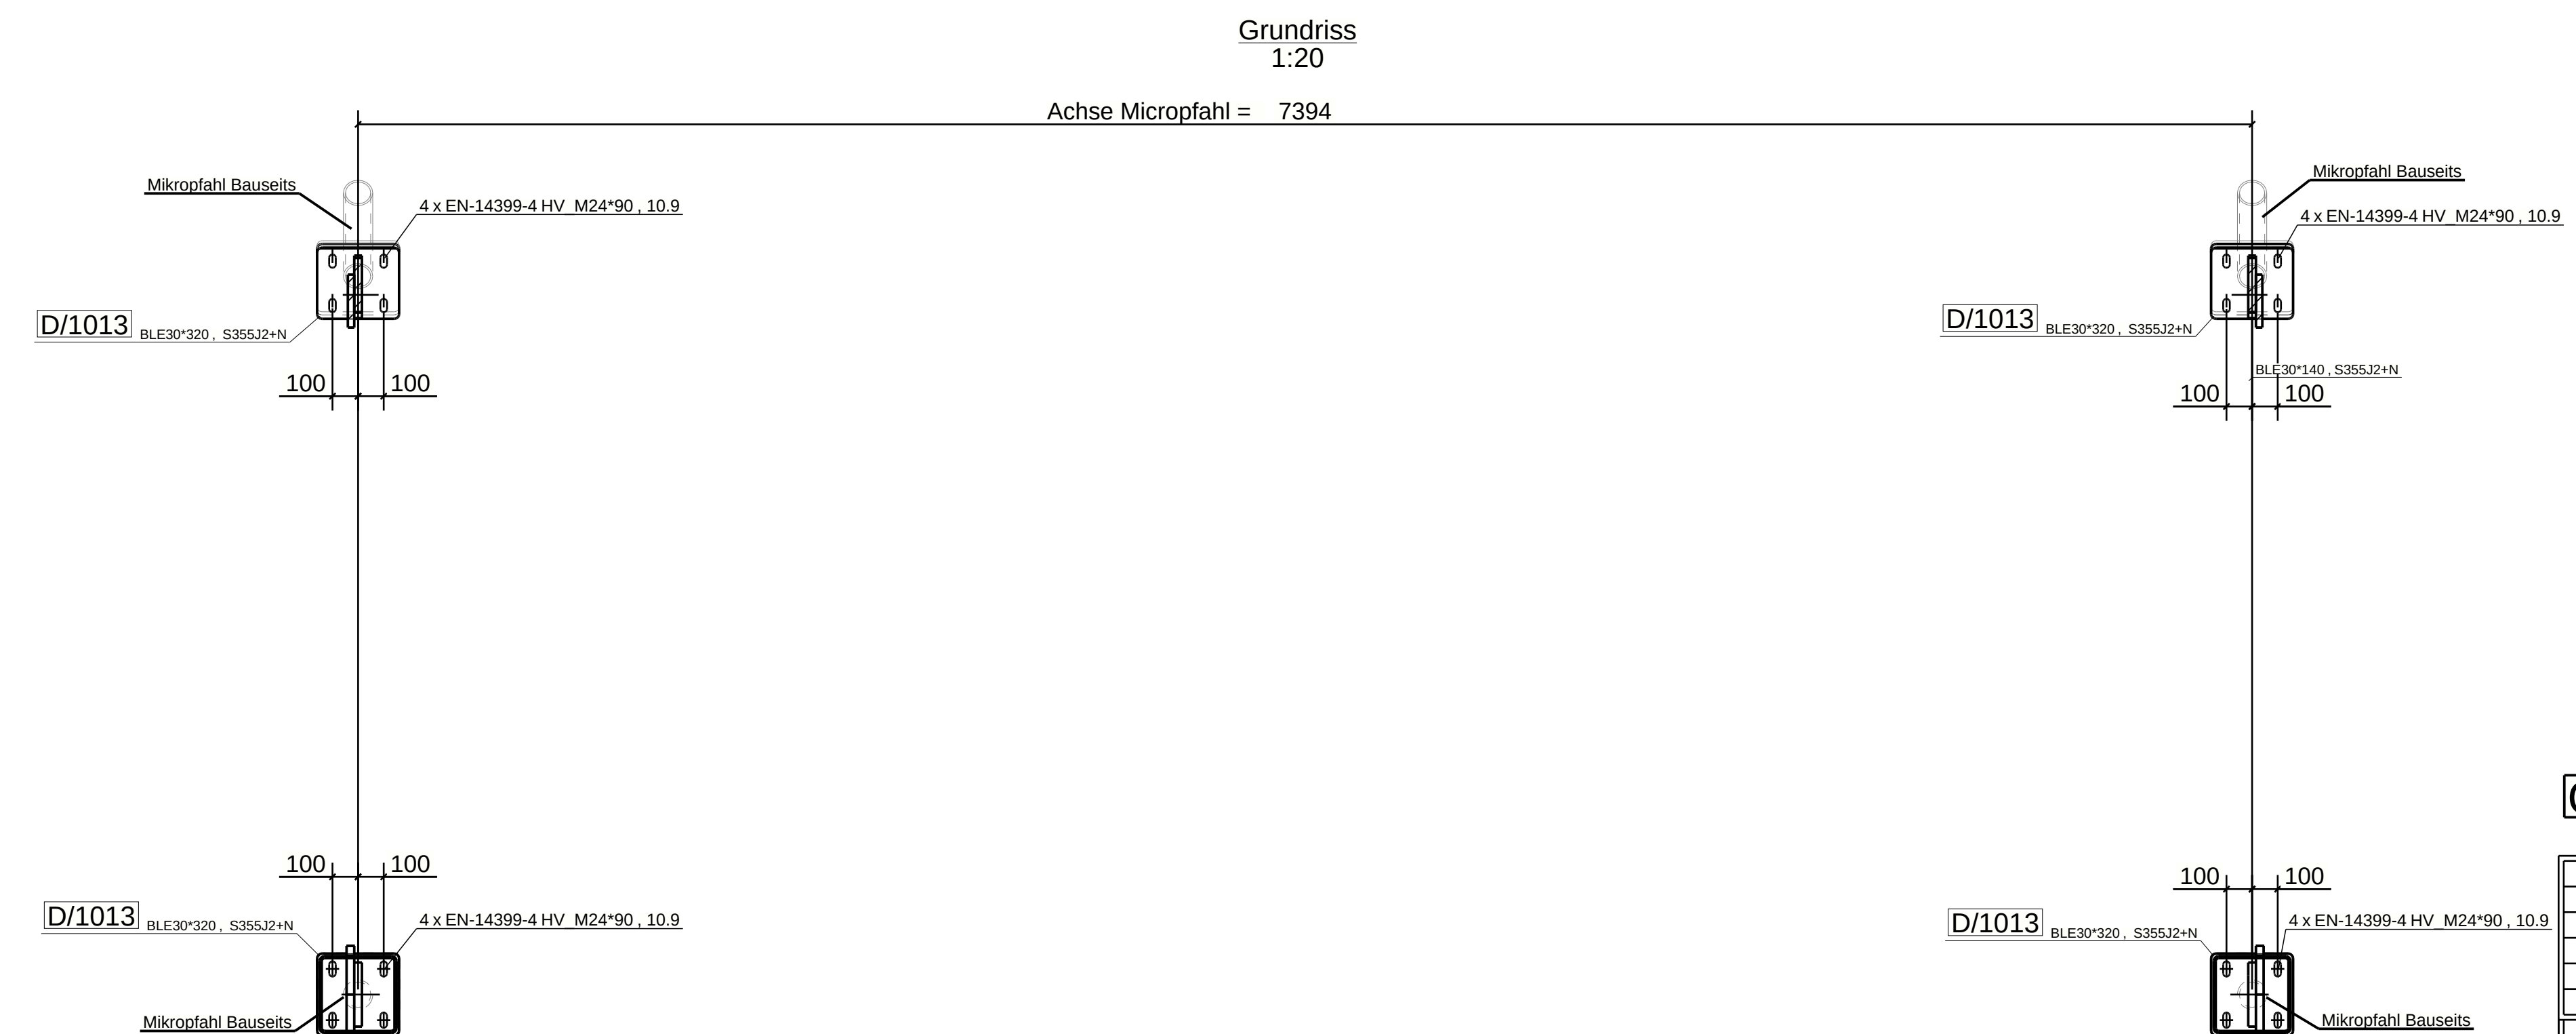
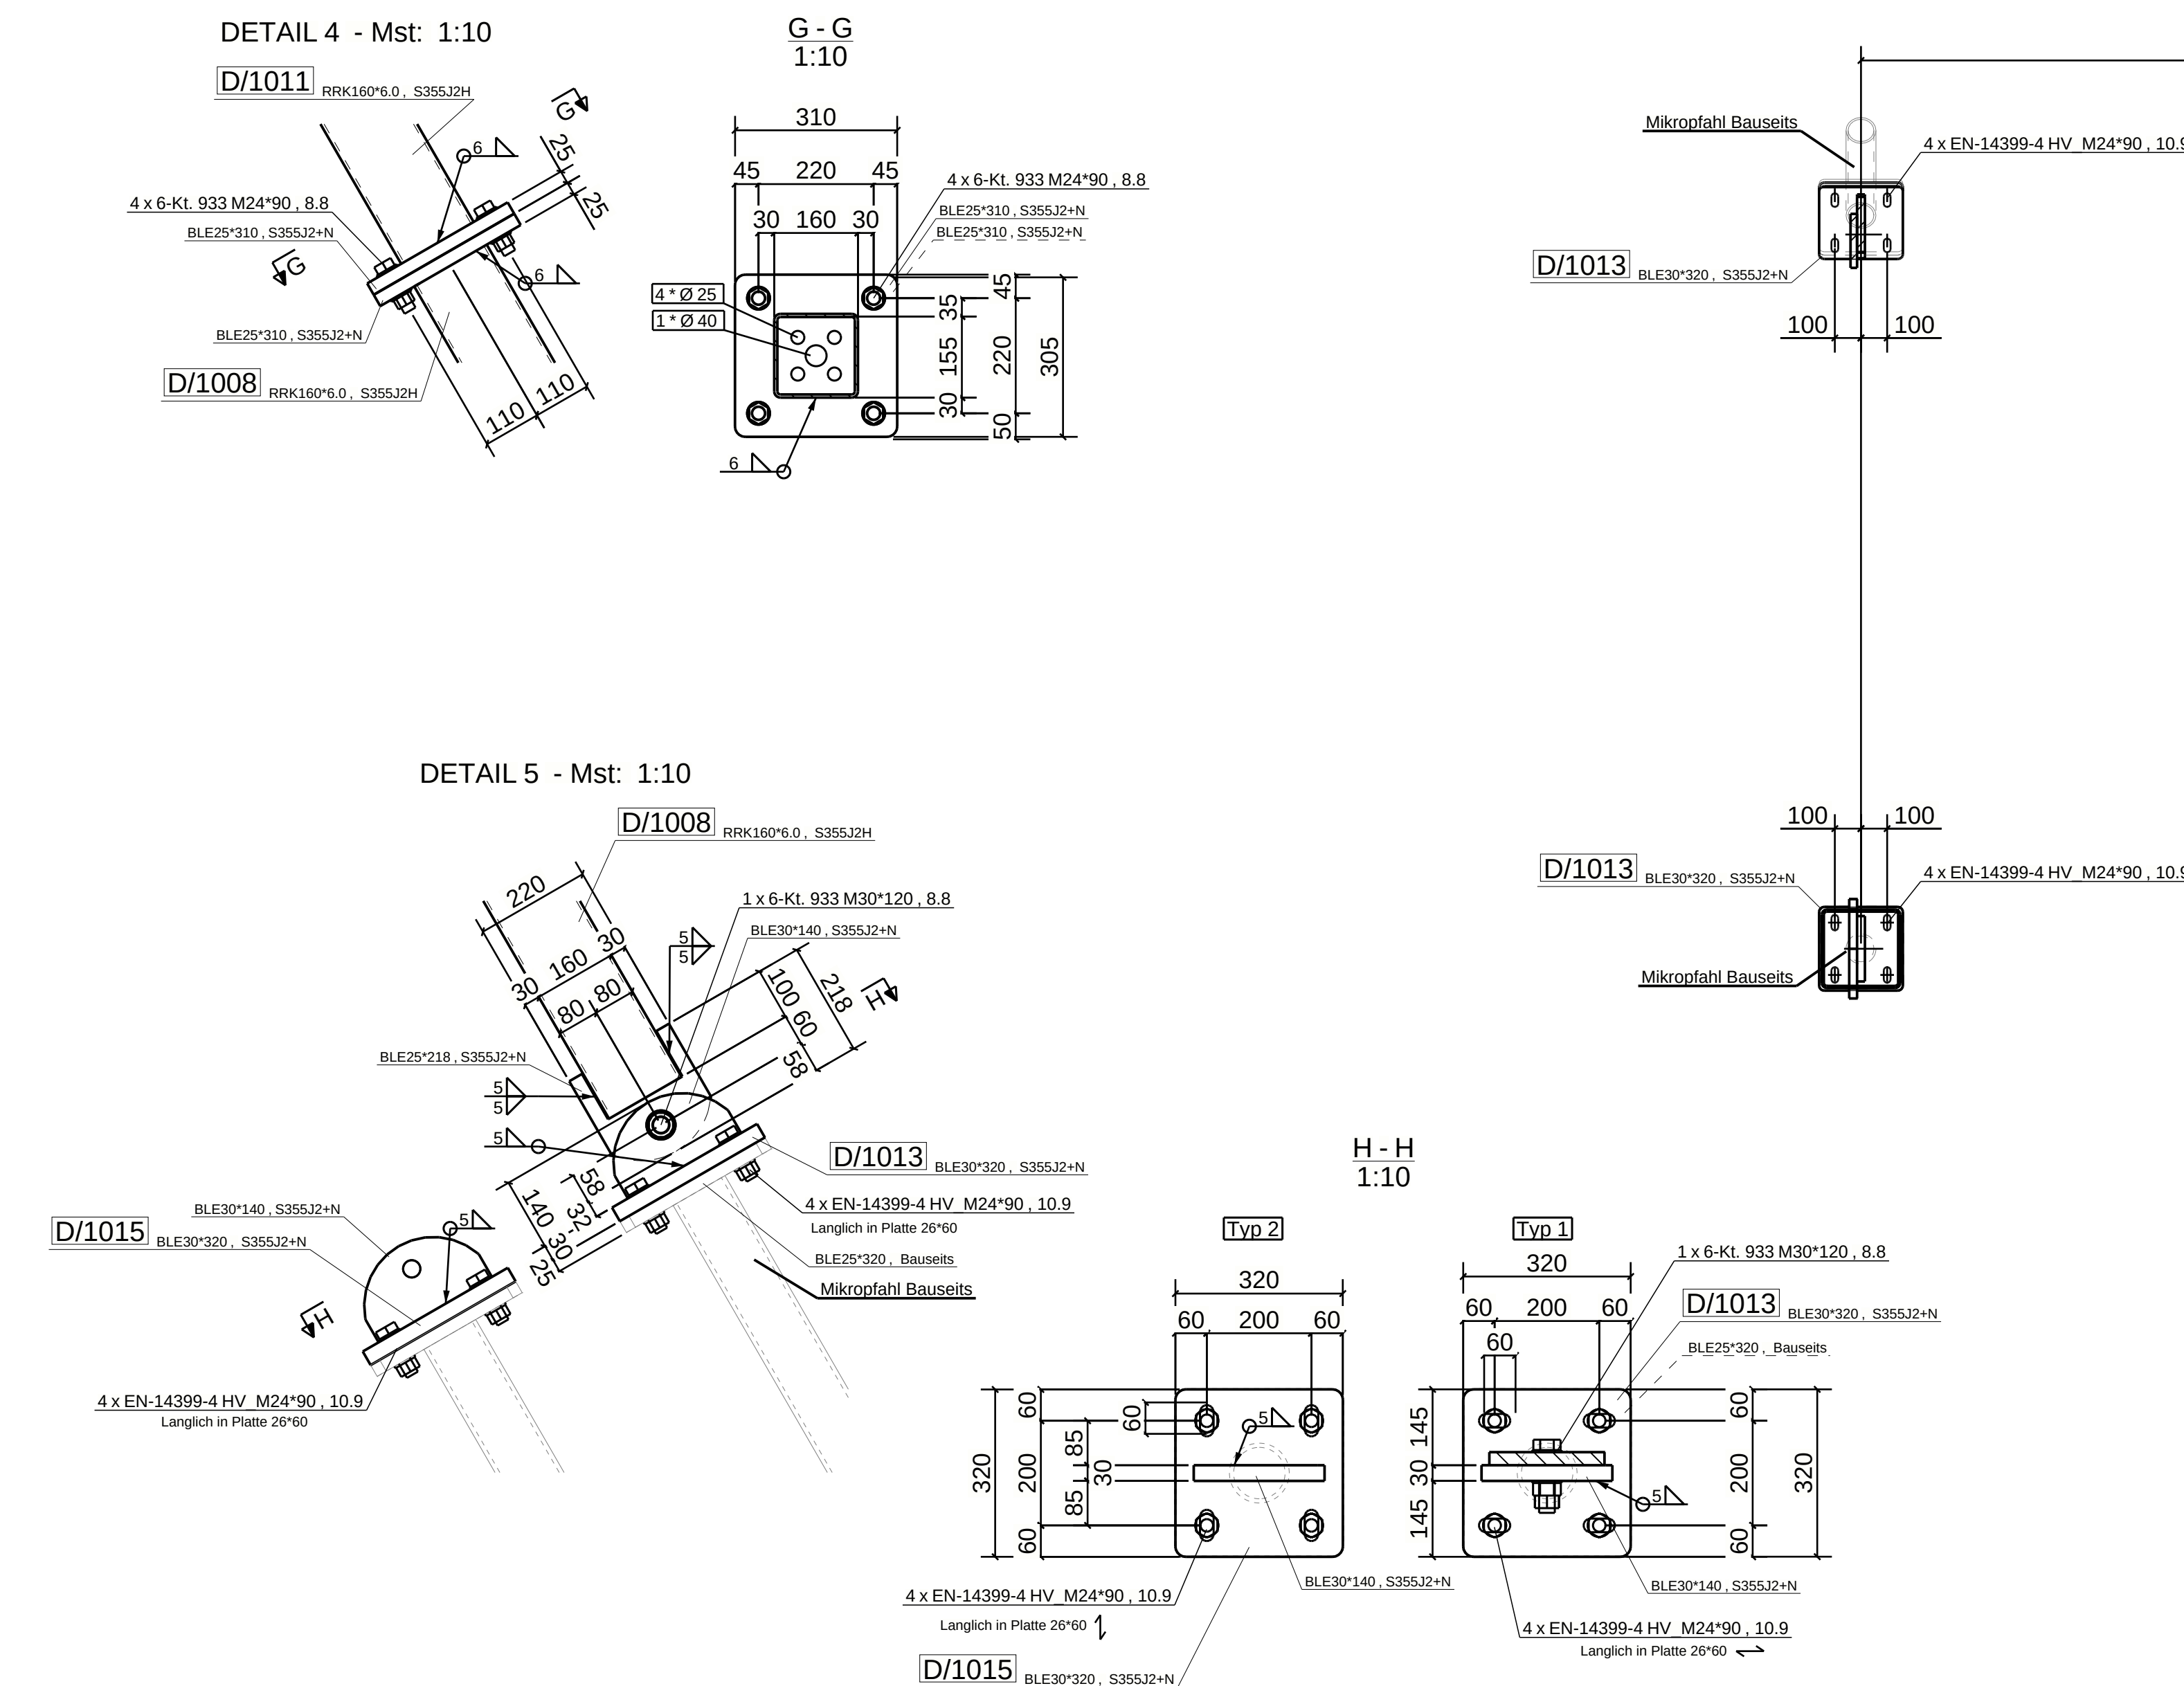
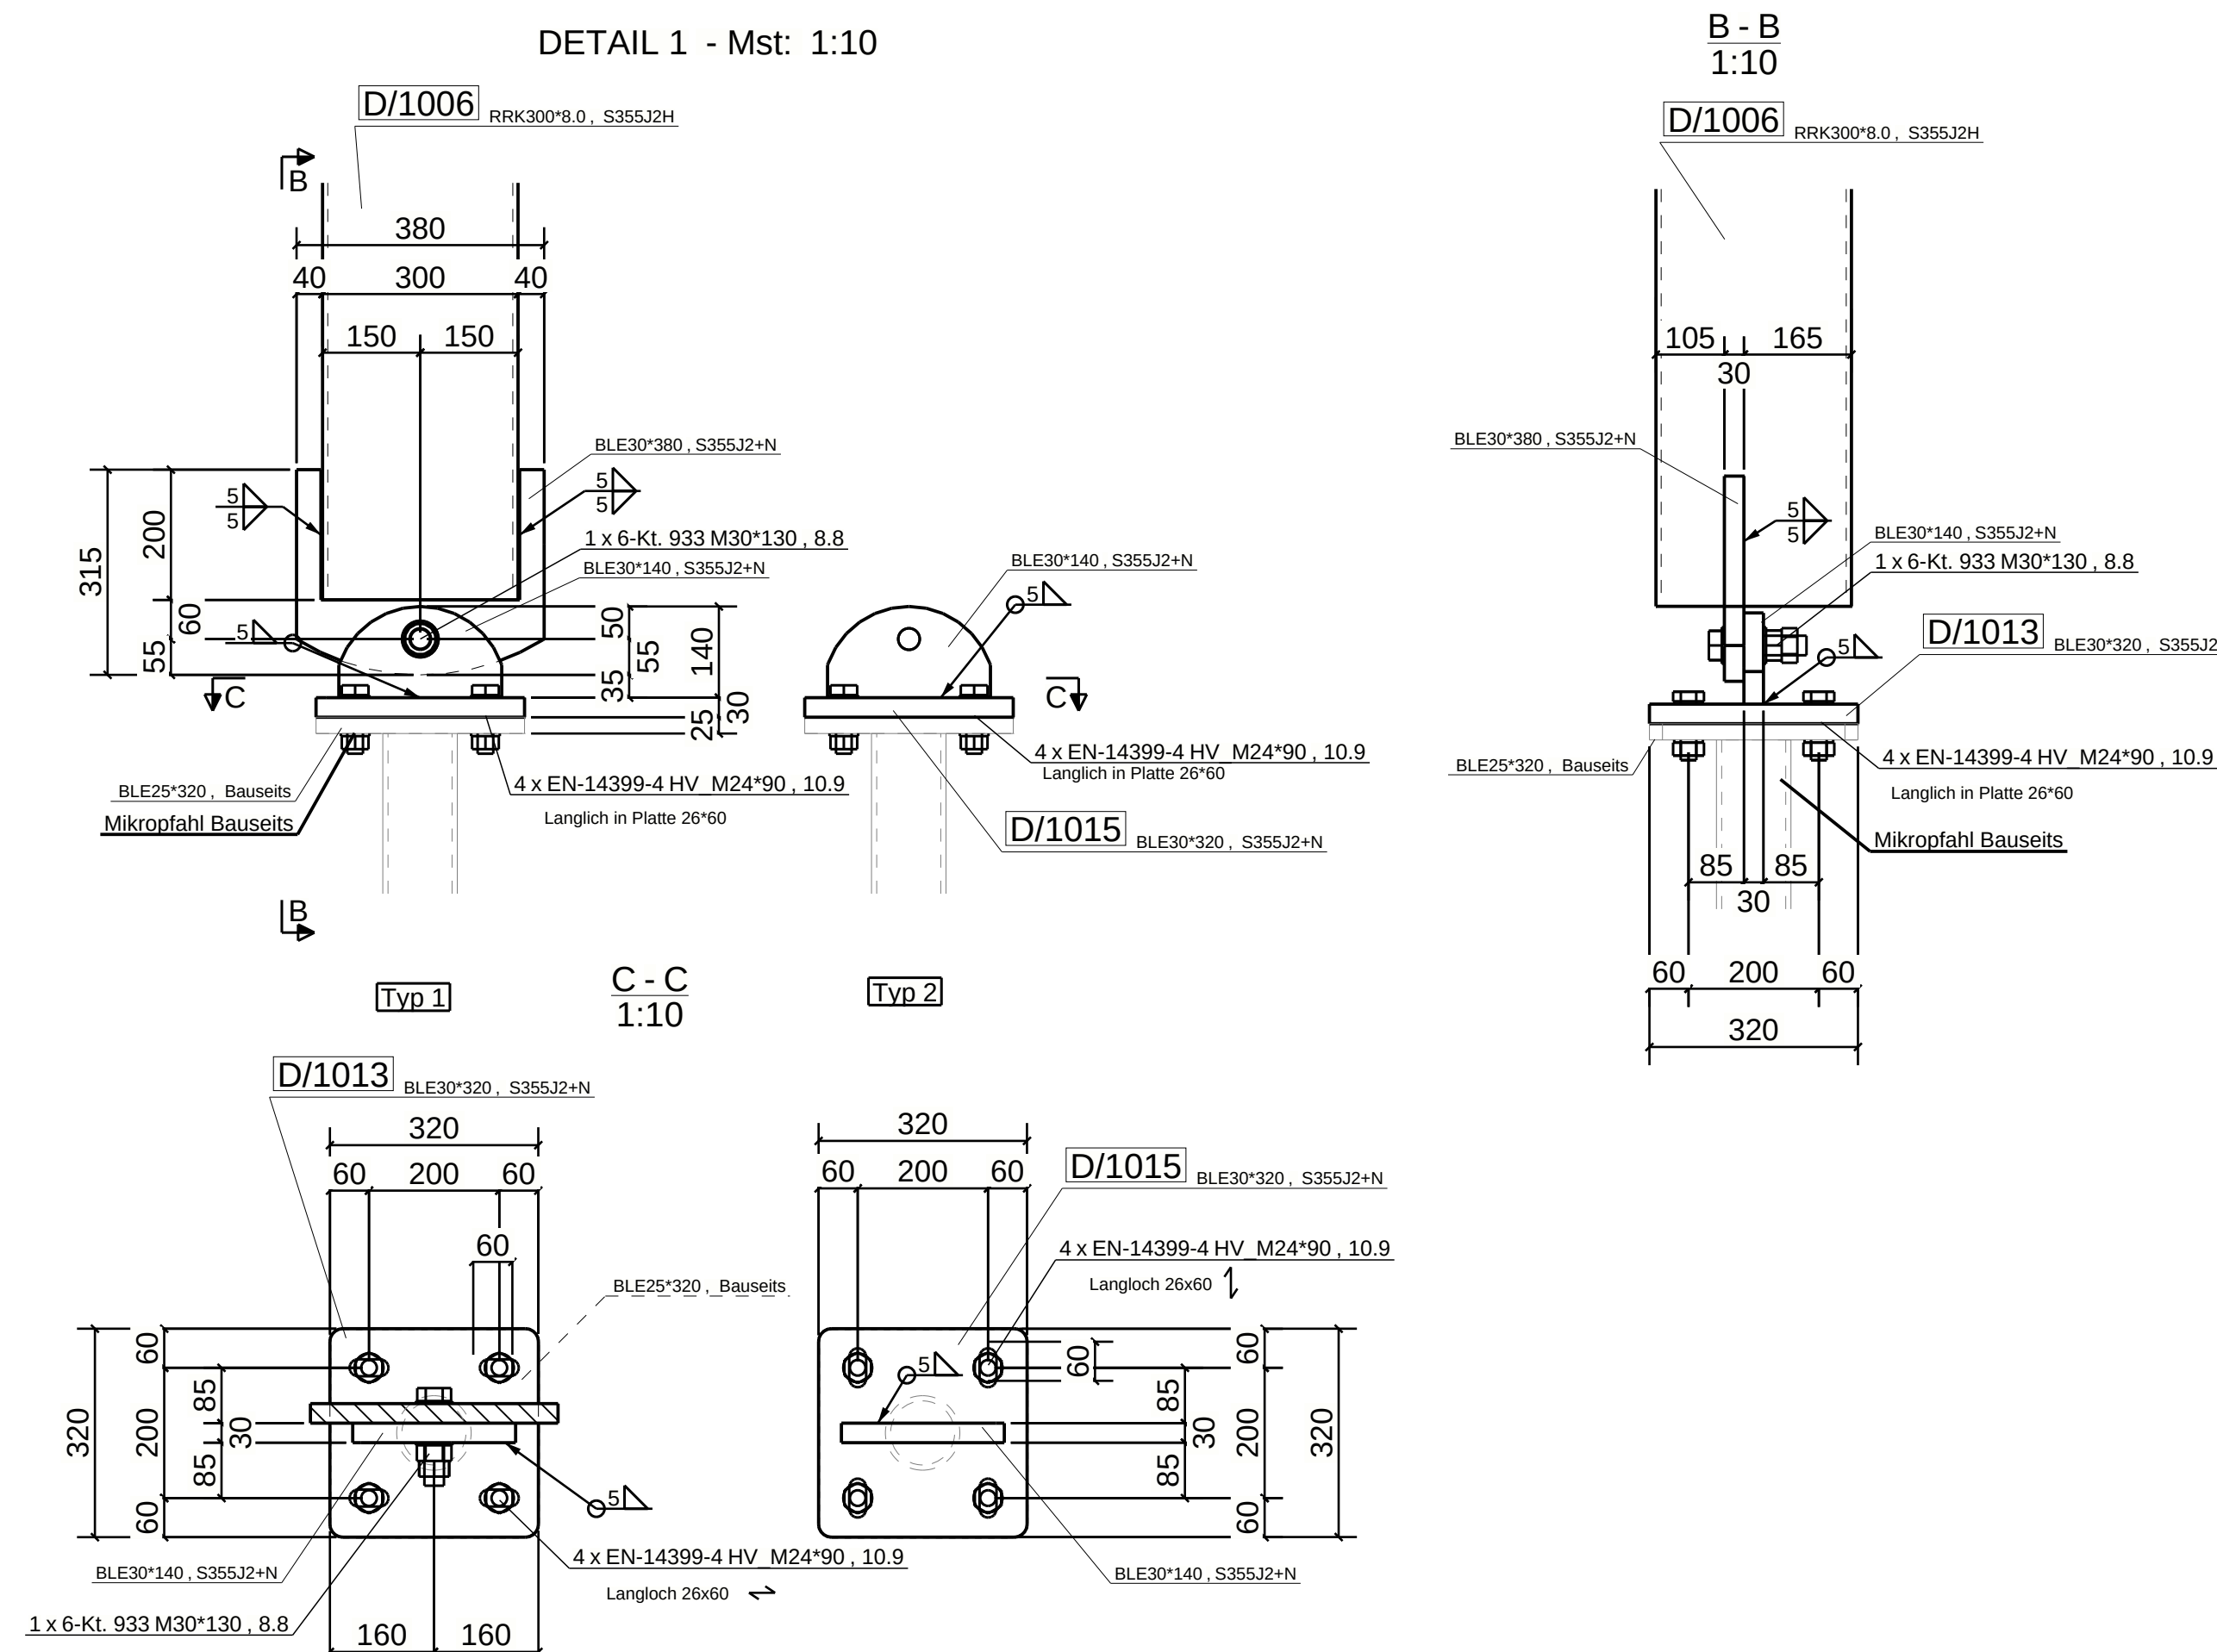


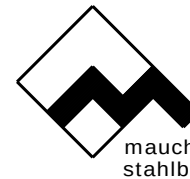

B	07.08.2025	Schraubenbeschriftung				J Maier	
		Detail 3 geändert				P Kocher	
Datum		ÄNDERUNGSGEBIENE				NAME	
INDEX							
		MAUCHLE STAHLBAU AG Industriestrasse 9 Tel. 0411 925 12 11 6210 SURSEE info@mauchle Stahlbau.ch					
Auftrag: 24027 Zeichner: PK		BAUWERK Axpo Solutions AG					
Interne Kontrolle ABTEILUNG: UNTERSCHRIFT		BAUSTELE NalpSolar					
PL: L. Durrer		BESCHUNG: Primärkonstruktion Typ D Ansicht, Schnitte & Details					
MAISTAB: 1:10 1:20 1:55		ZEICHNUNGSNUMMER 24027 S 0 M 004 B STRICHART STRICHSTÄRKE LAGE VERLEGEN ZUSÄTZLICHE ANMERKUNGEN BEZUGSZEICHEN					
ANSICHT: 							