
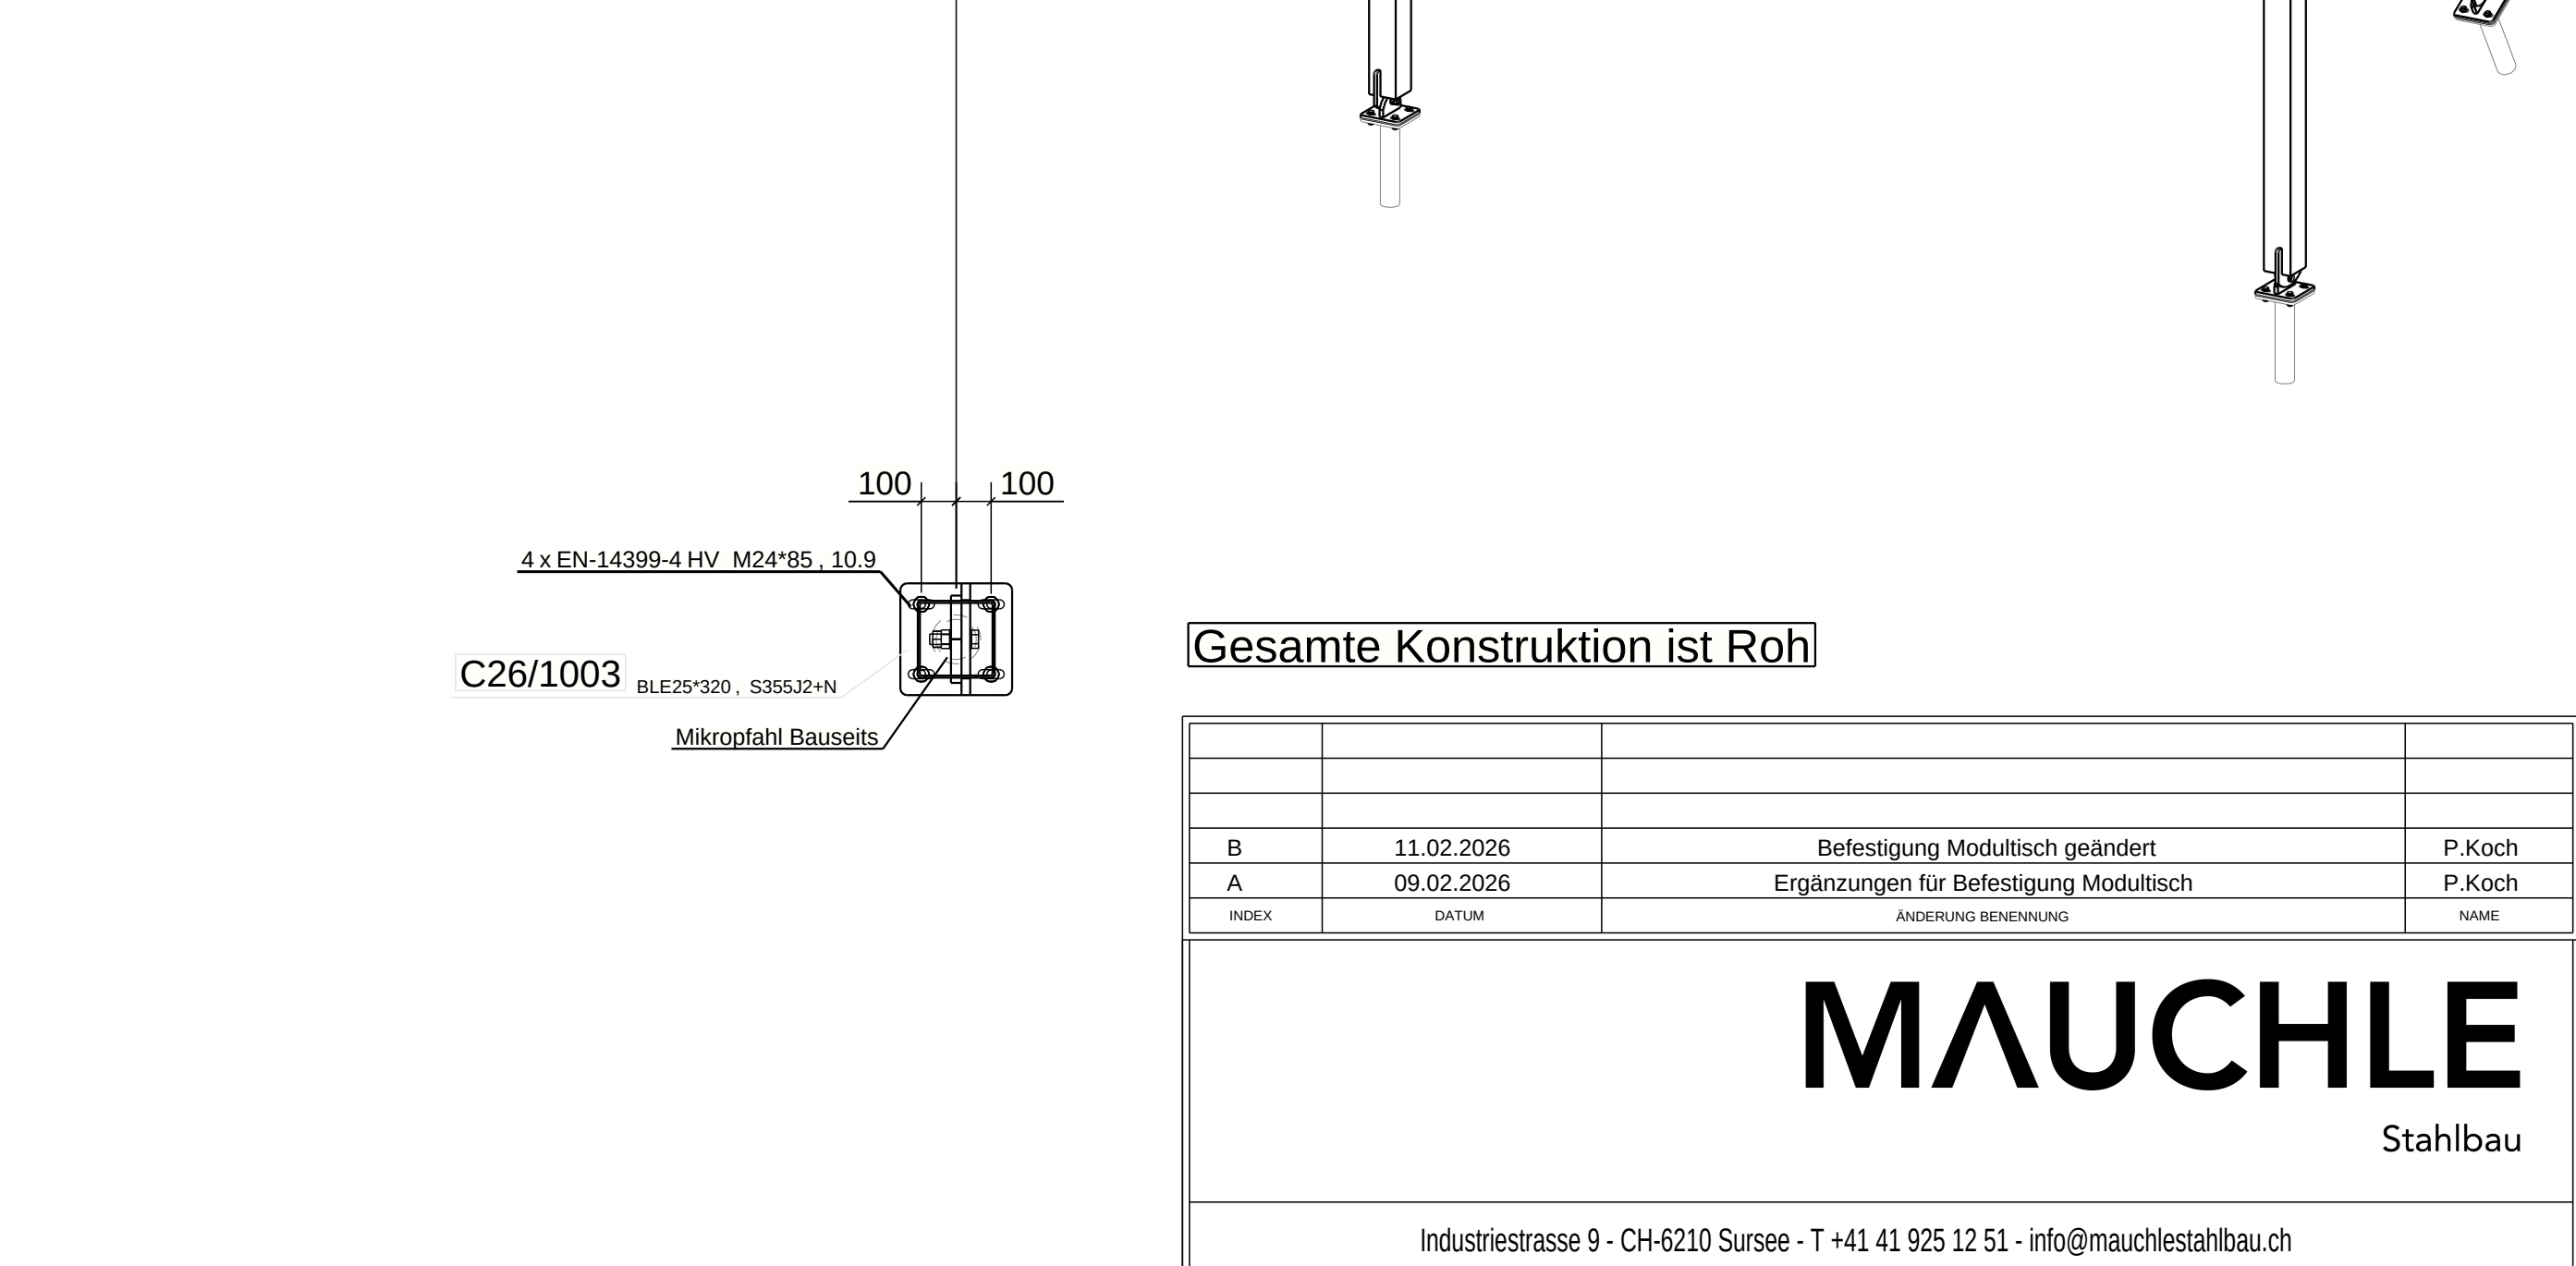
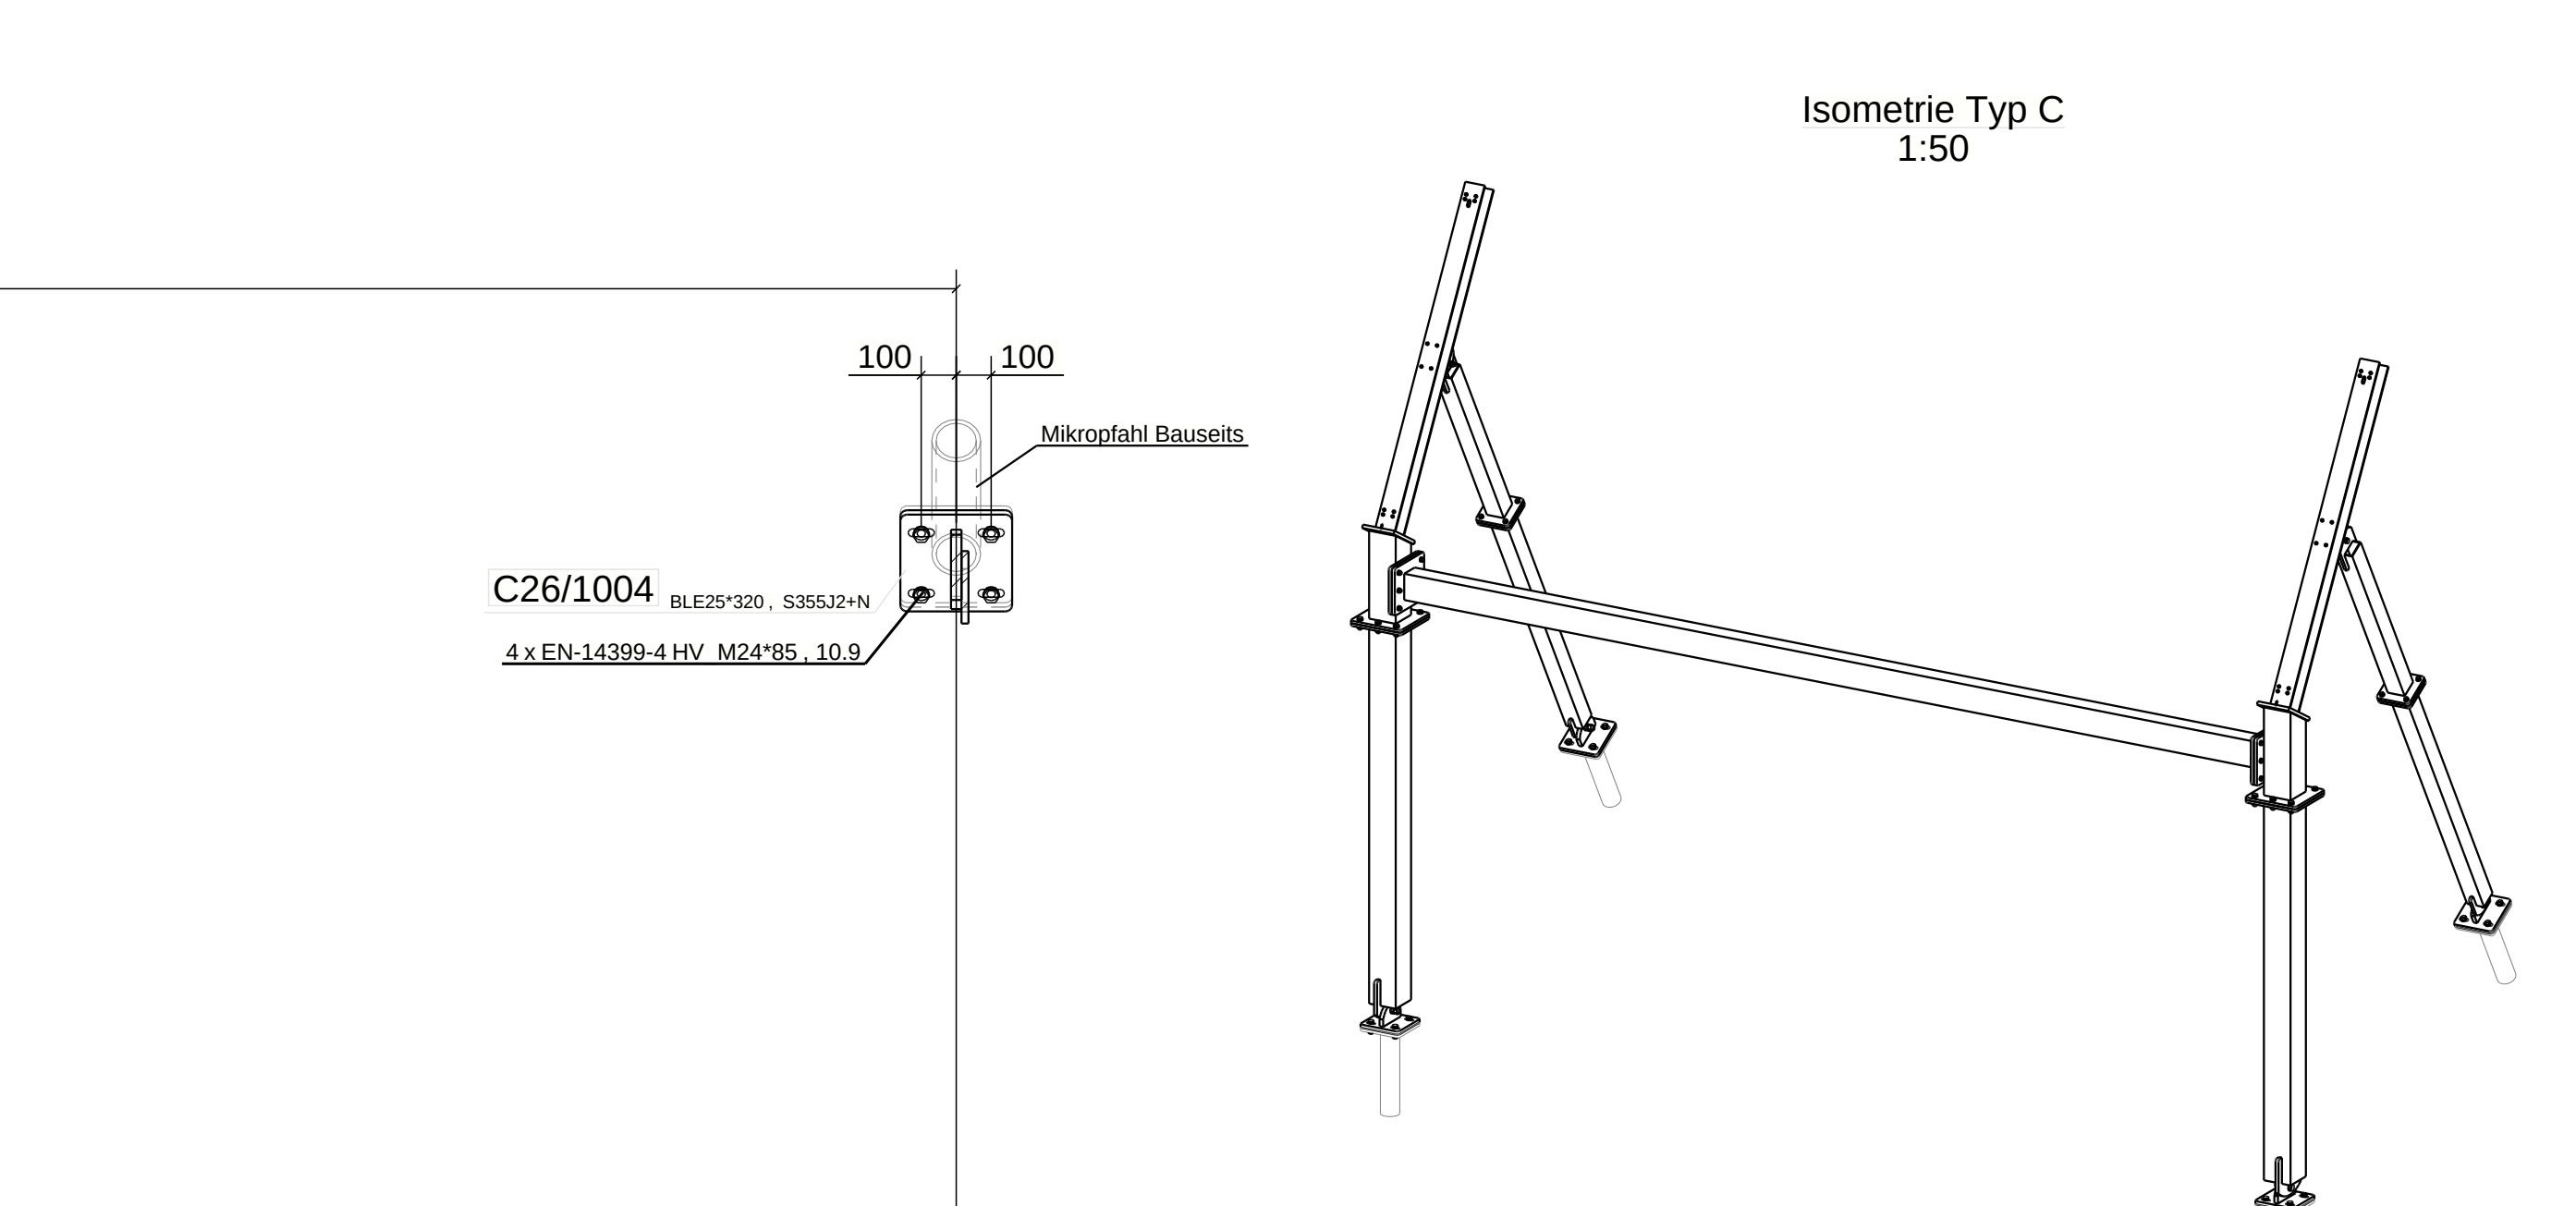
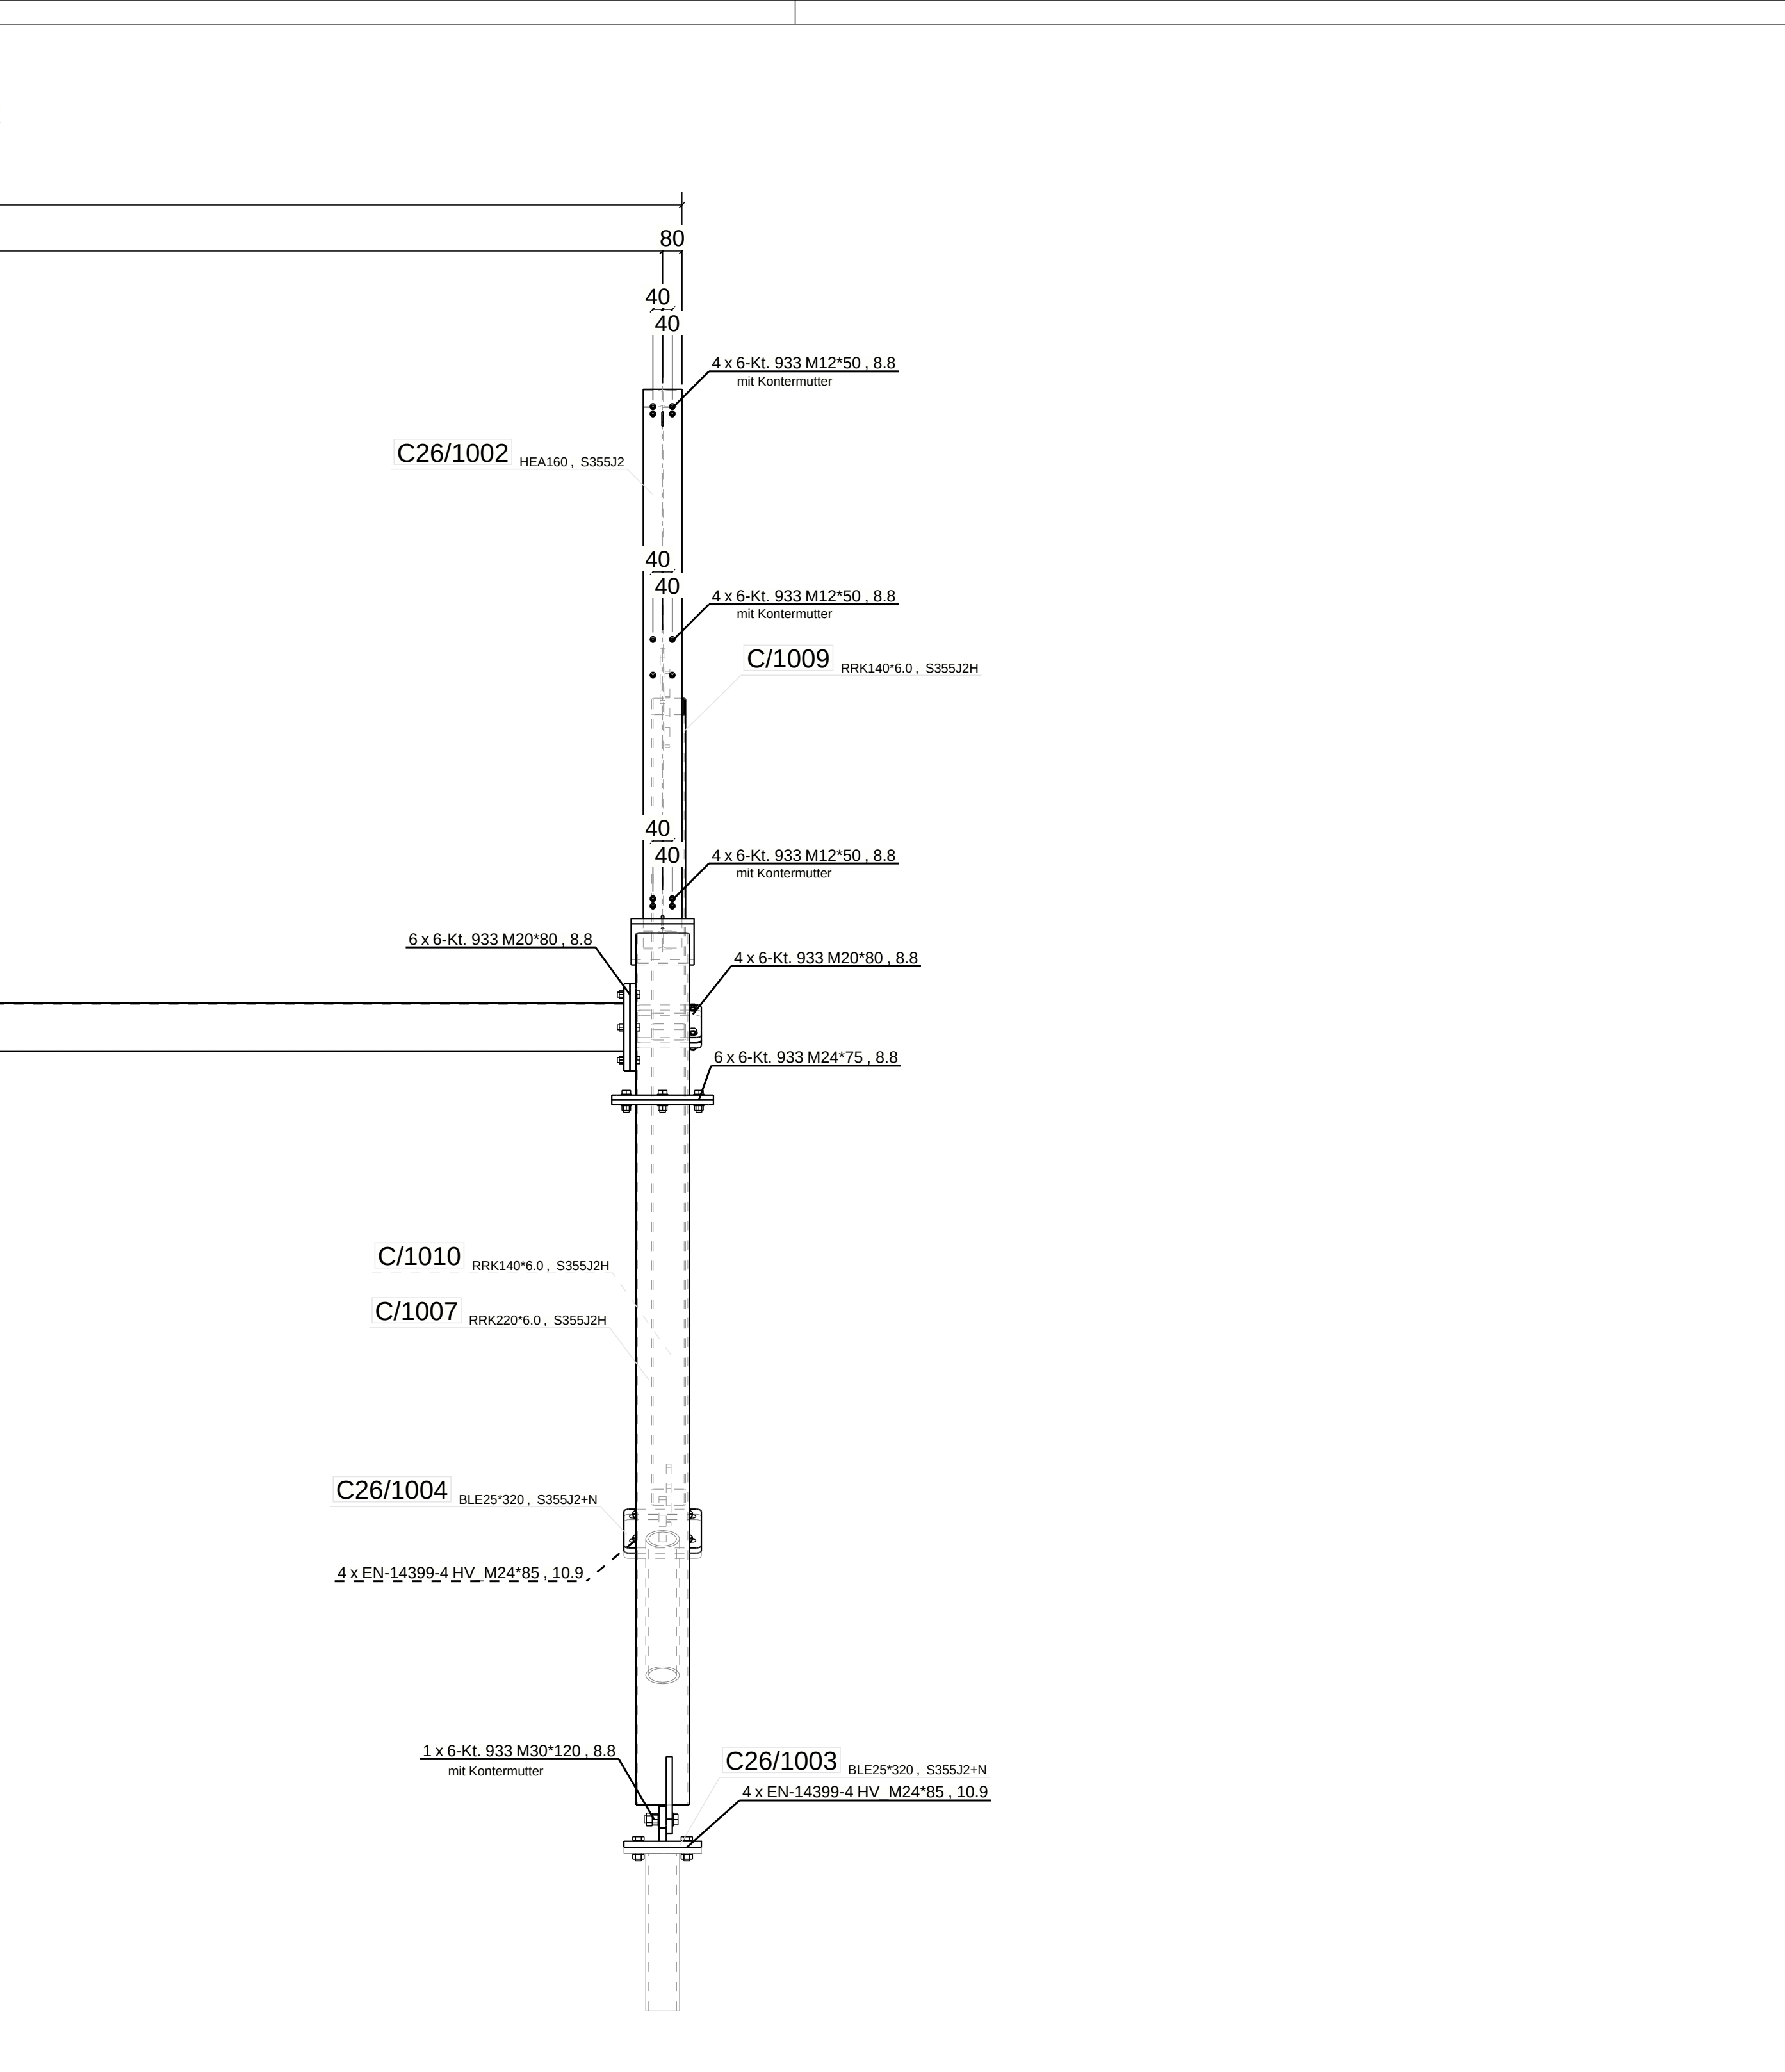


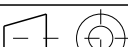

MAUCHLE Stahlbau									
Industriestrasse 9 · CH-4220 Sursee · T +41 41 925 12 51 · info@mauchlestaalbau.ch									
Auftragsnr.: 24027			BAUHEER Xppo Solutions AG						
Zeichner: P. Koch			BAUSTELLE NalpSolar						
Interne Kontrolle			BEZEICHNUNG Primärkonstruktion Typ C Typ 2026 Ansicht, Schnitte & Details						
ABTEILUNG UNTERSCHRIFT									
PL J. Mäder			ZEICHNUNGSNUMMER 24027 S 0 M 010 B						
MASSSTAB 1:10 1:20 1:50									
ANSCHEIT 									
VOR ANSATZ DERER ZEICHNUNG MIT UNTERSCHRIFTEN KONSTRUKTOR UND LEAD SHEET KÖNNEN UNTERSCHIEDLICHE VERFAHREN FÜR JEDE AN DRITTE PERSONEN MITTEILGEBEN WERDEN.									