
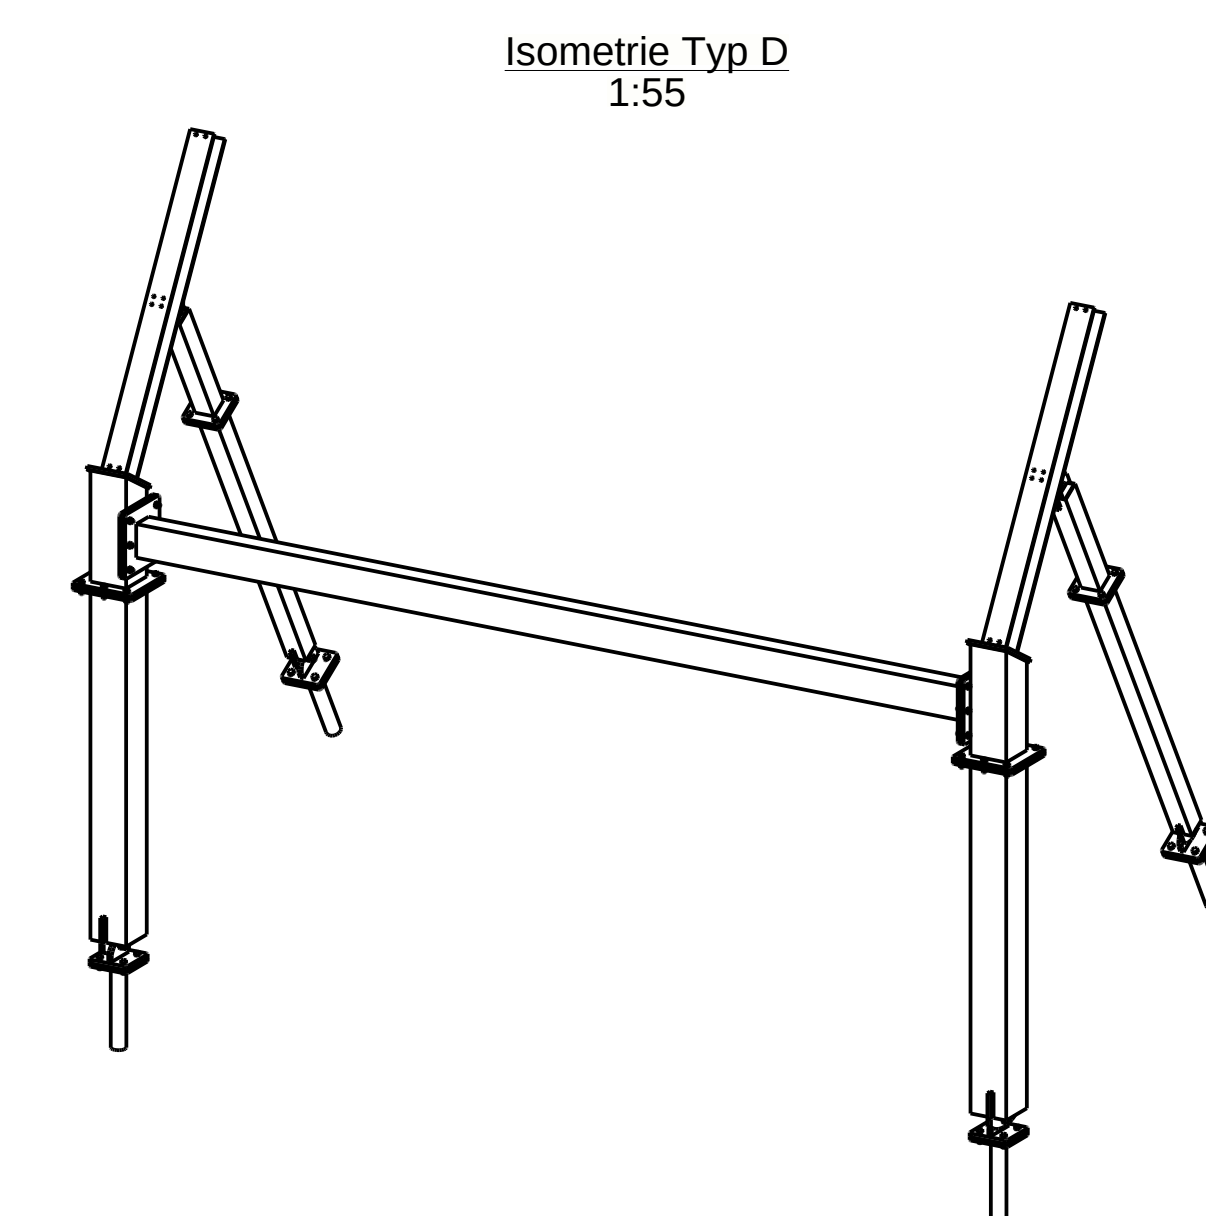
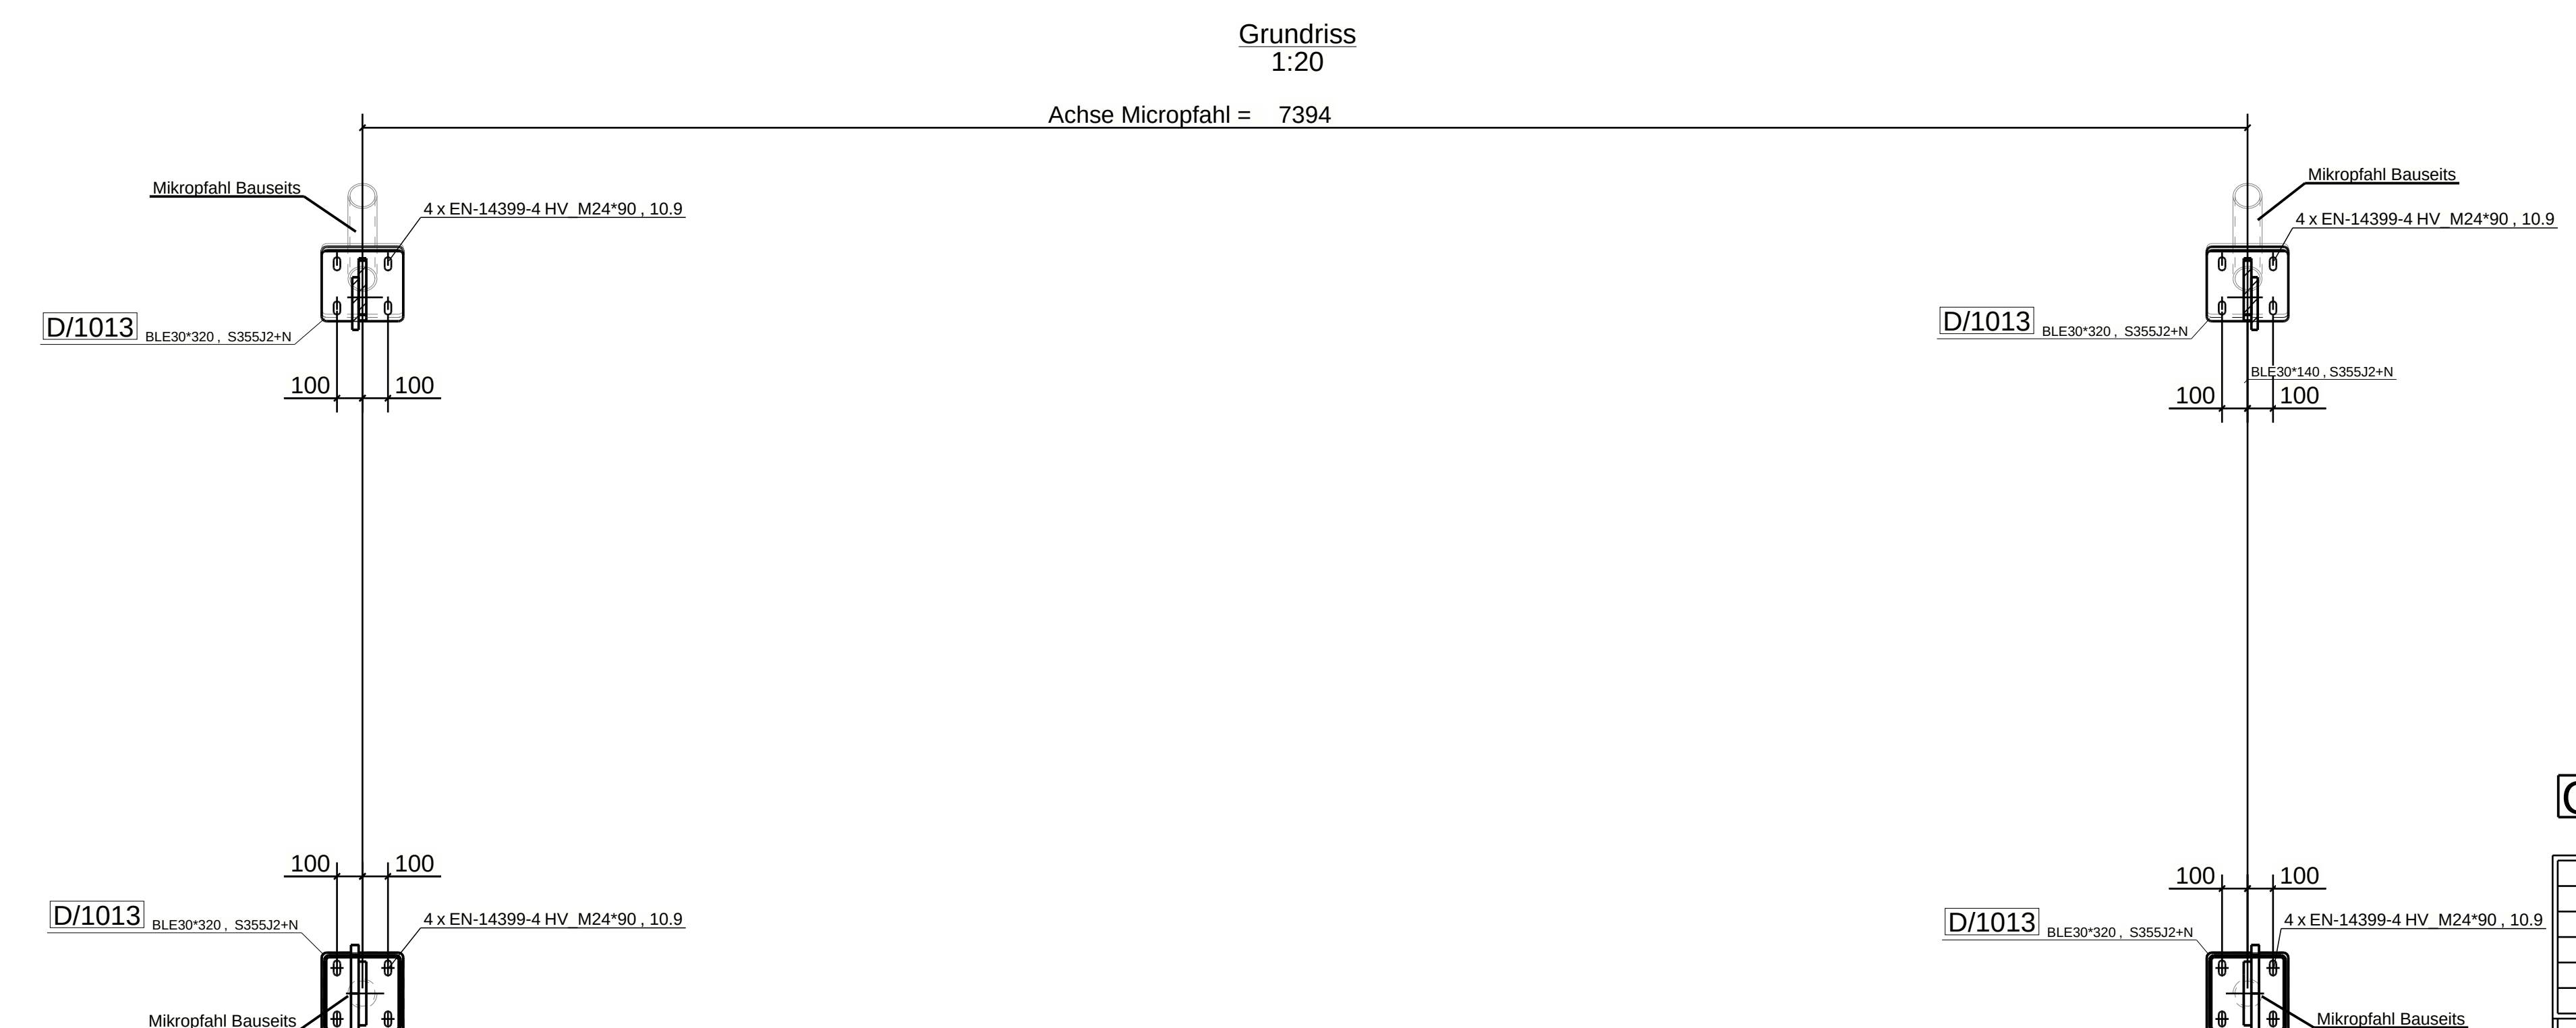
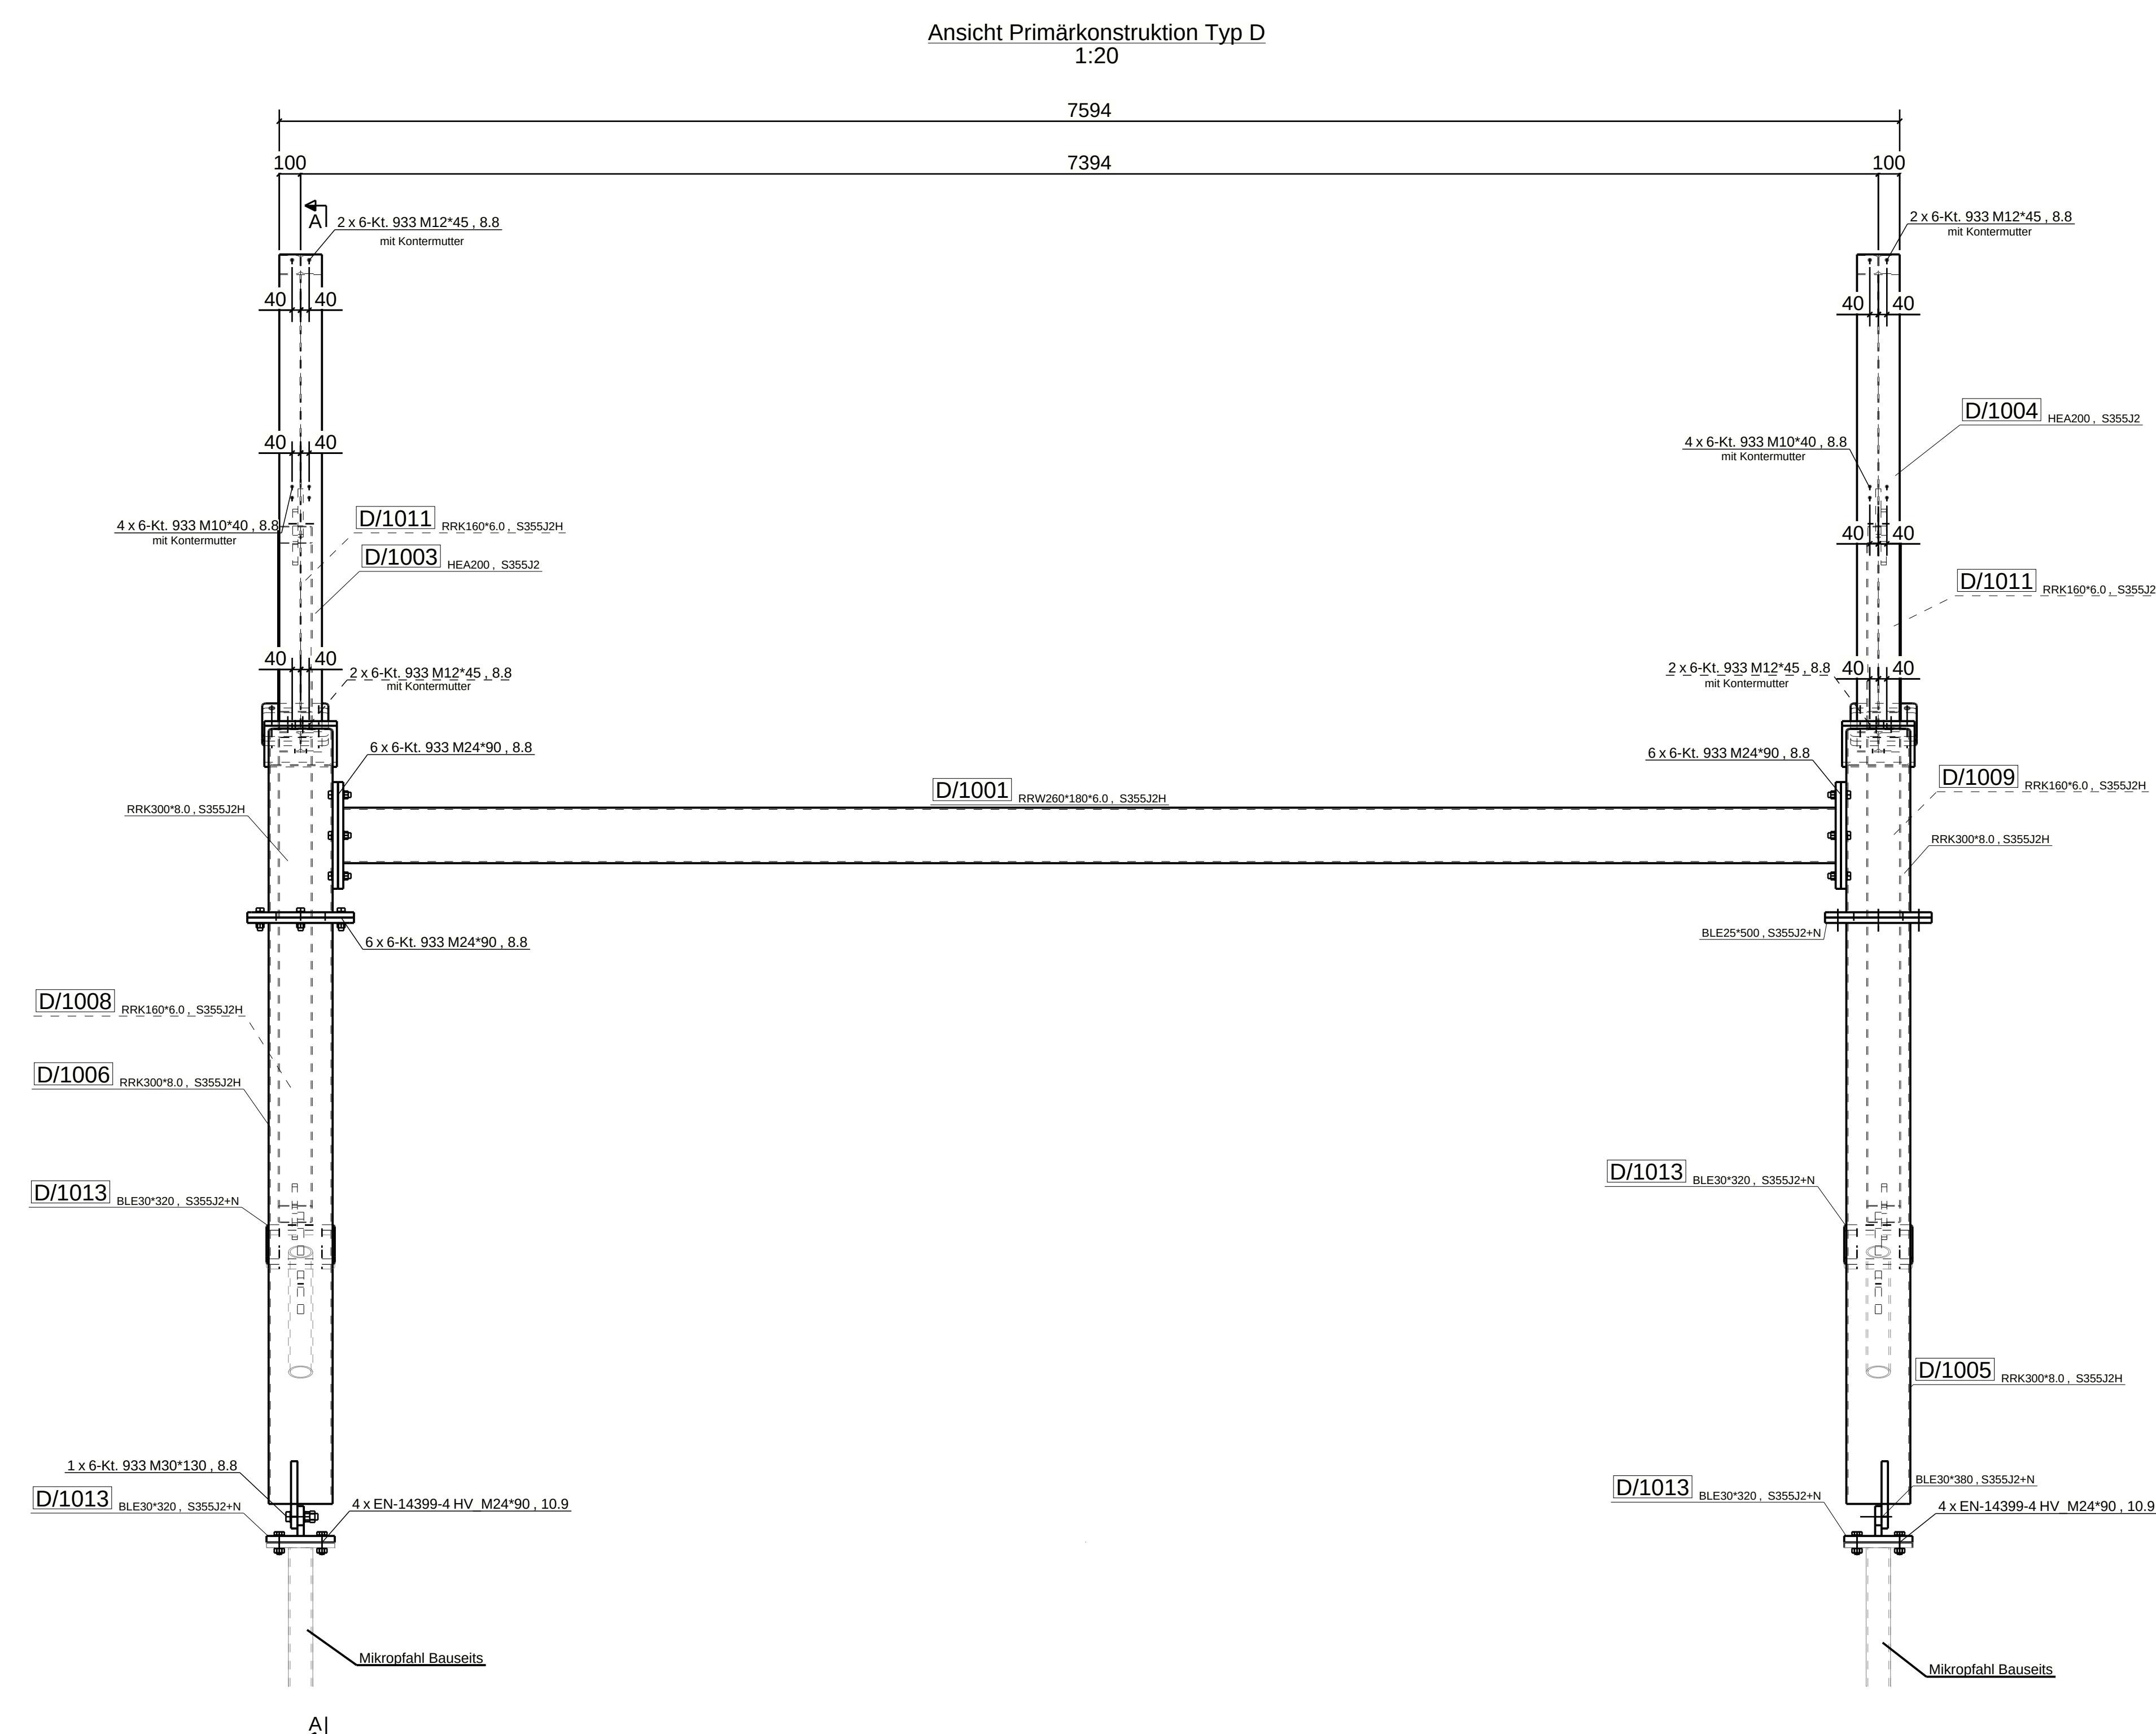
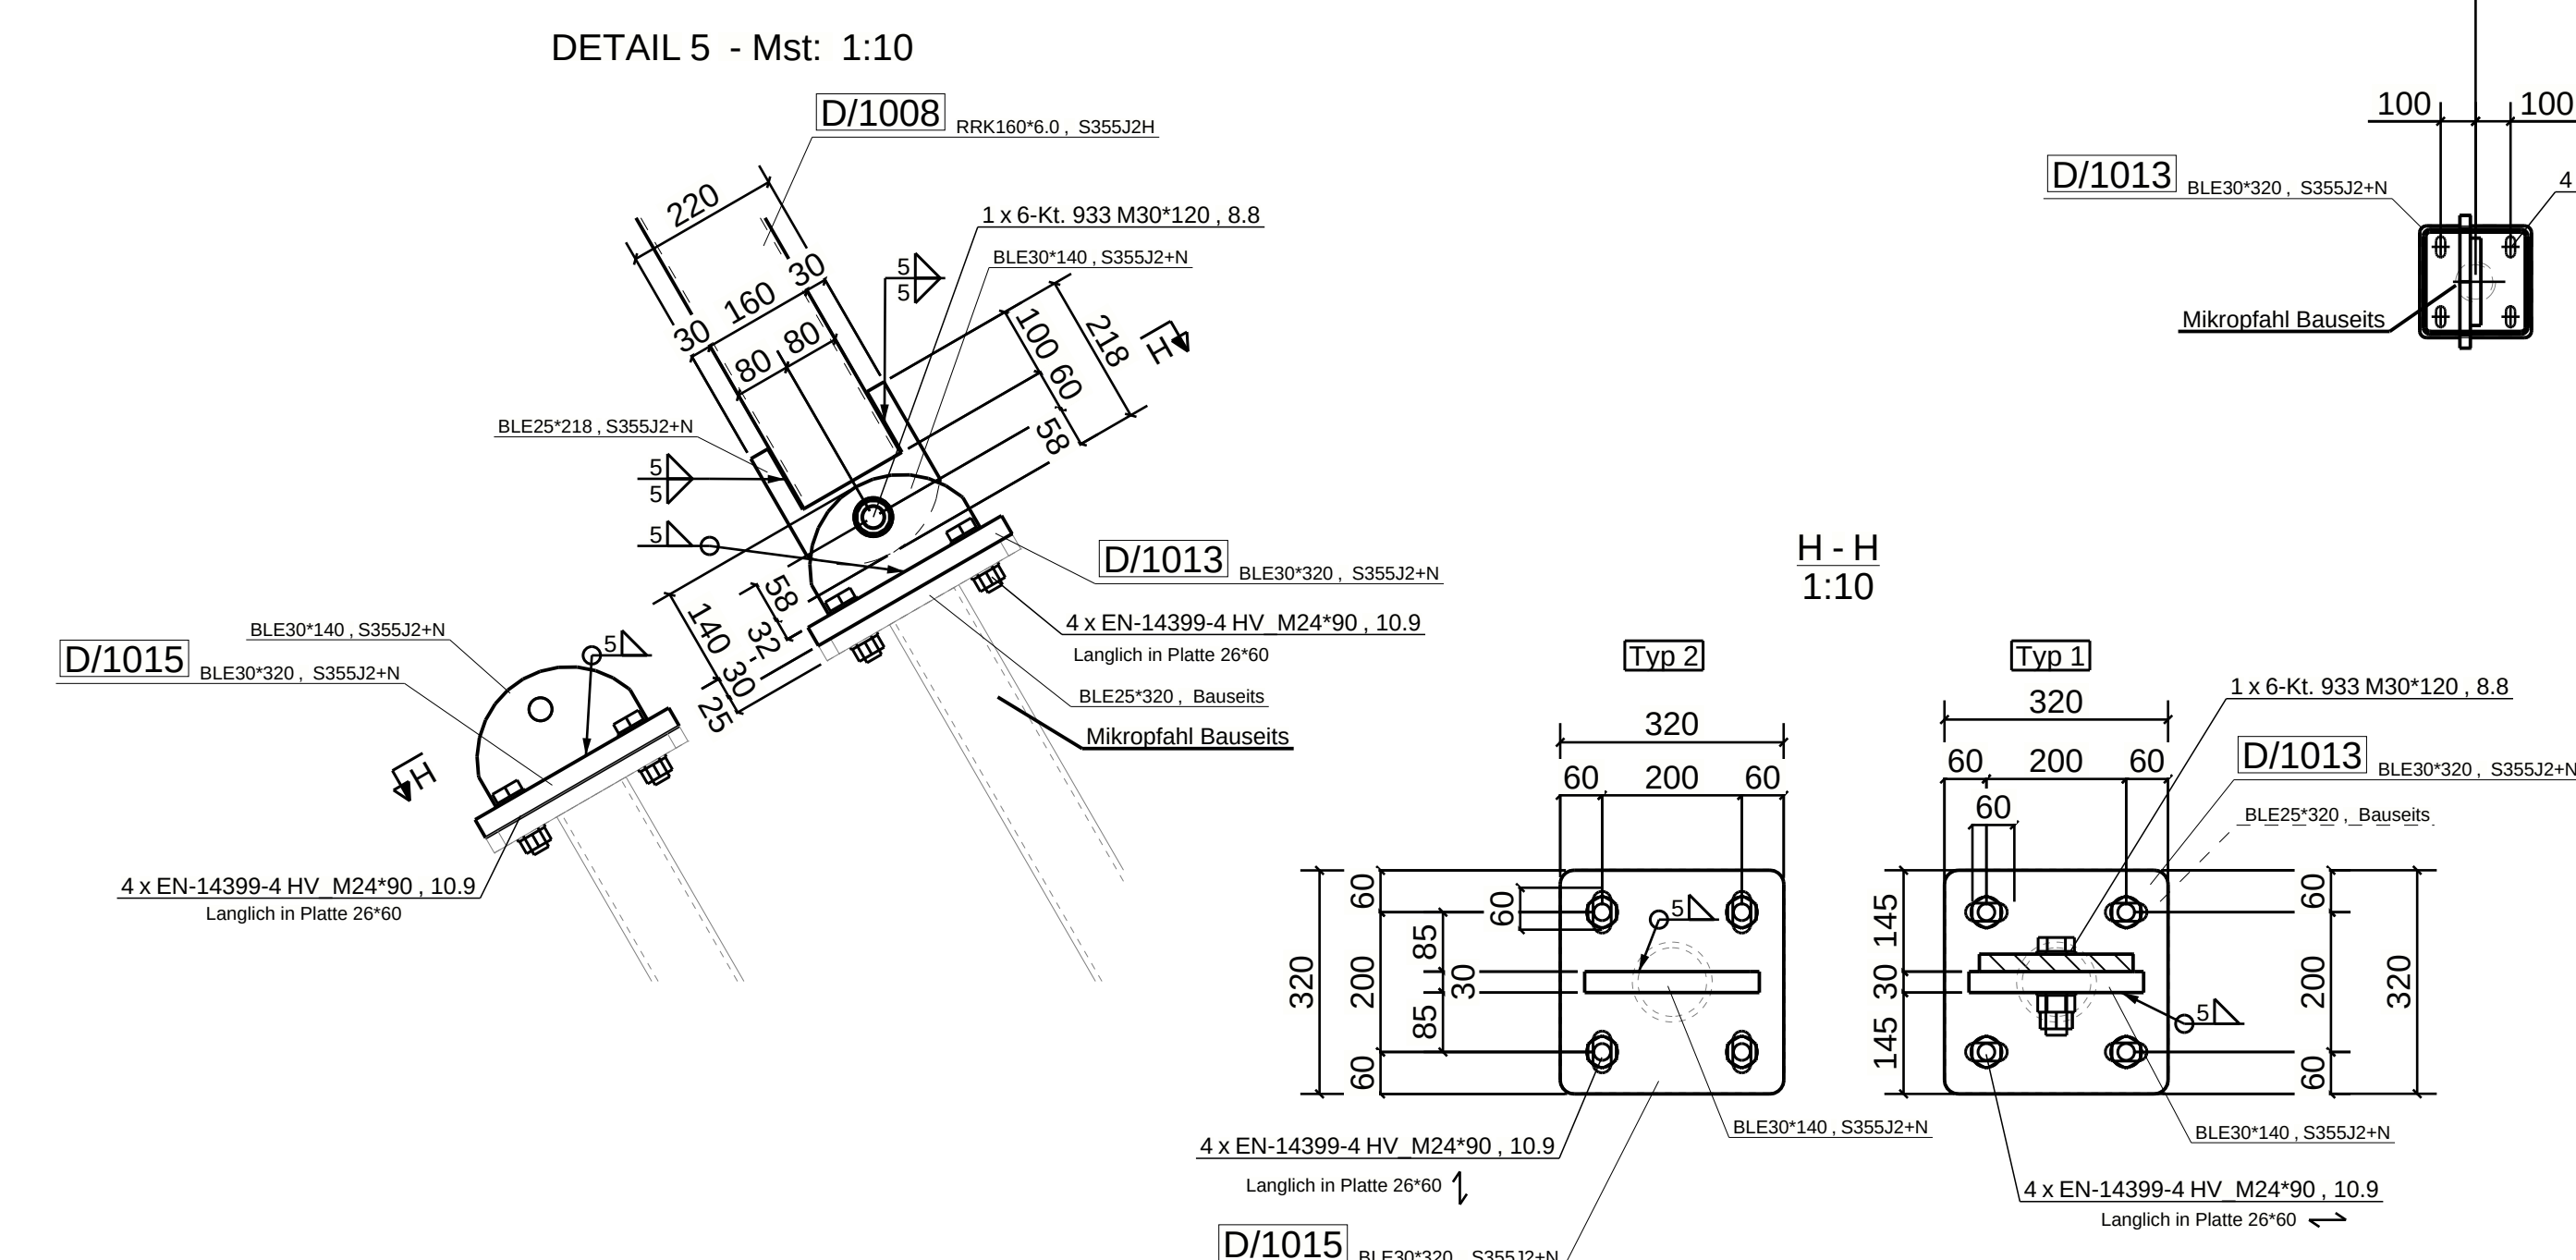
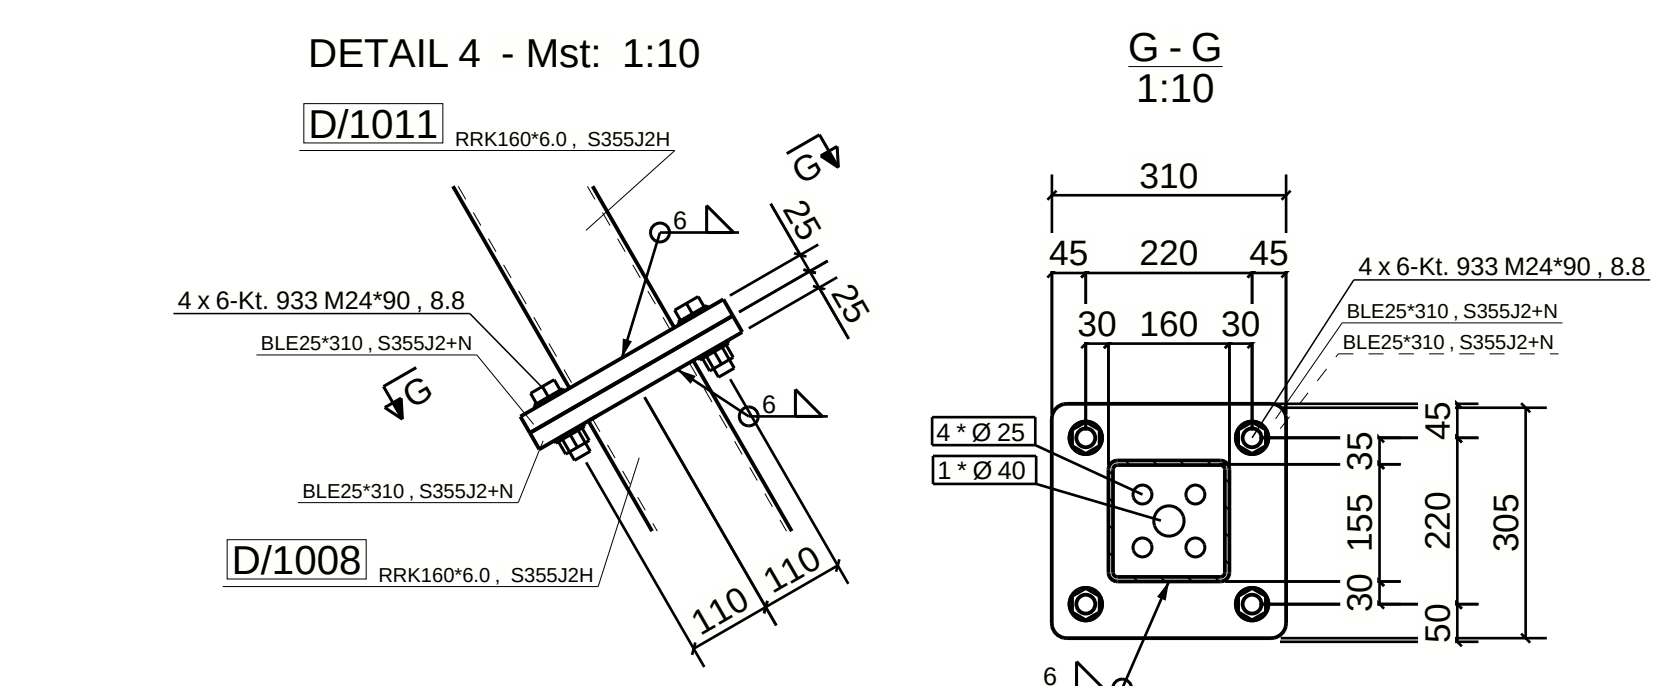
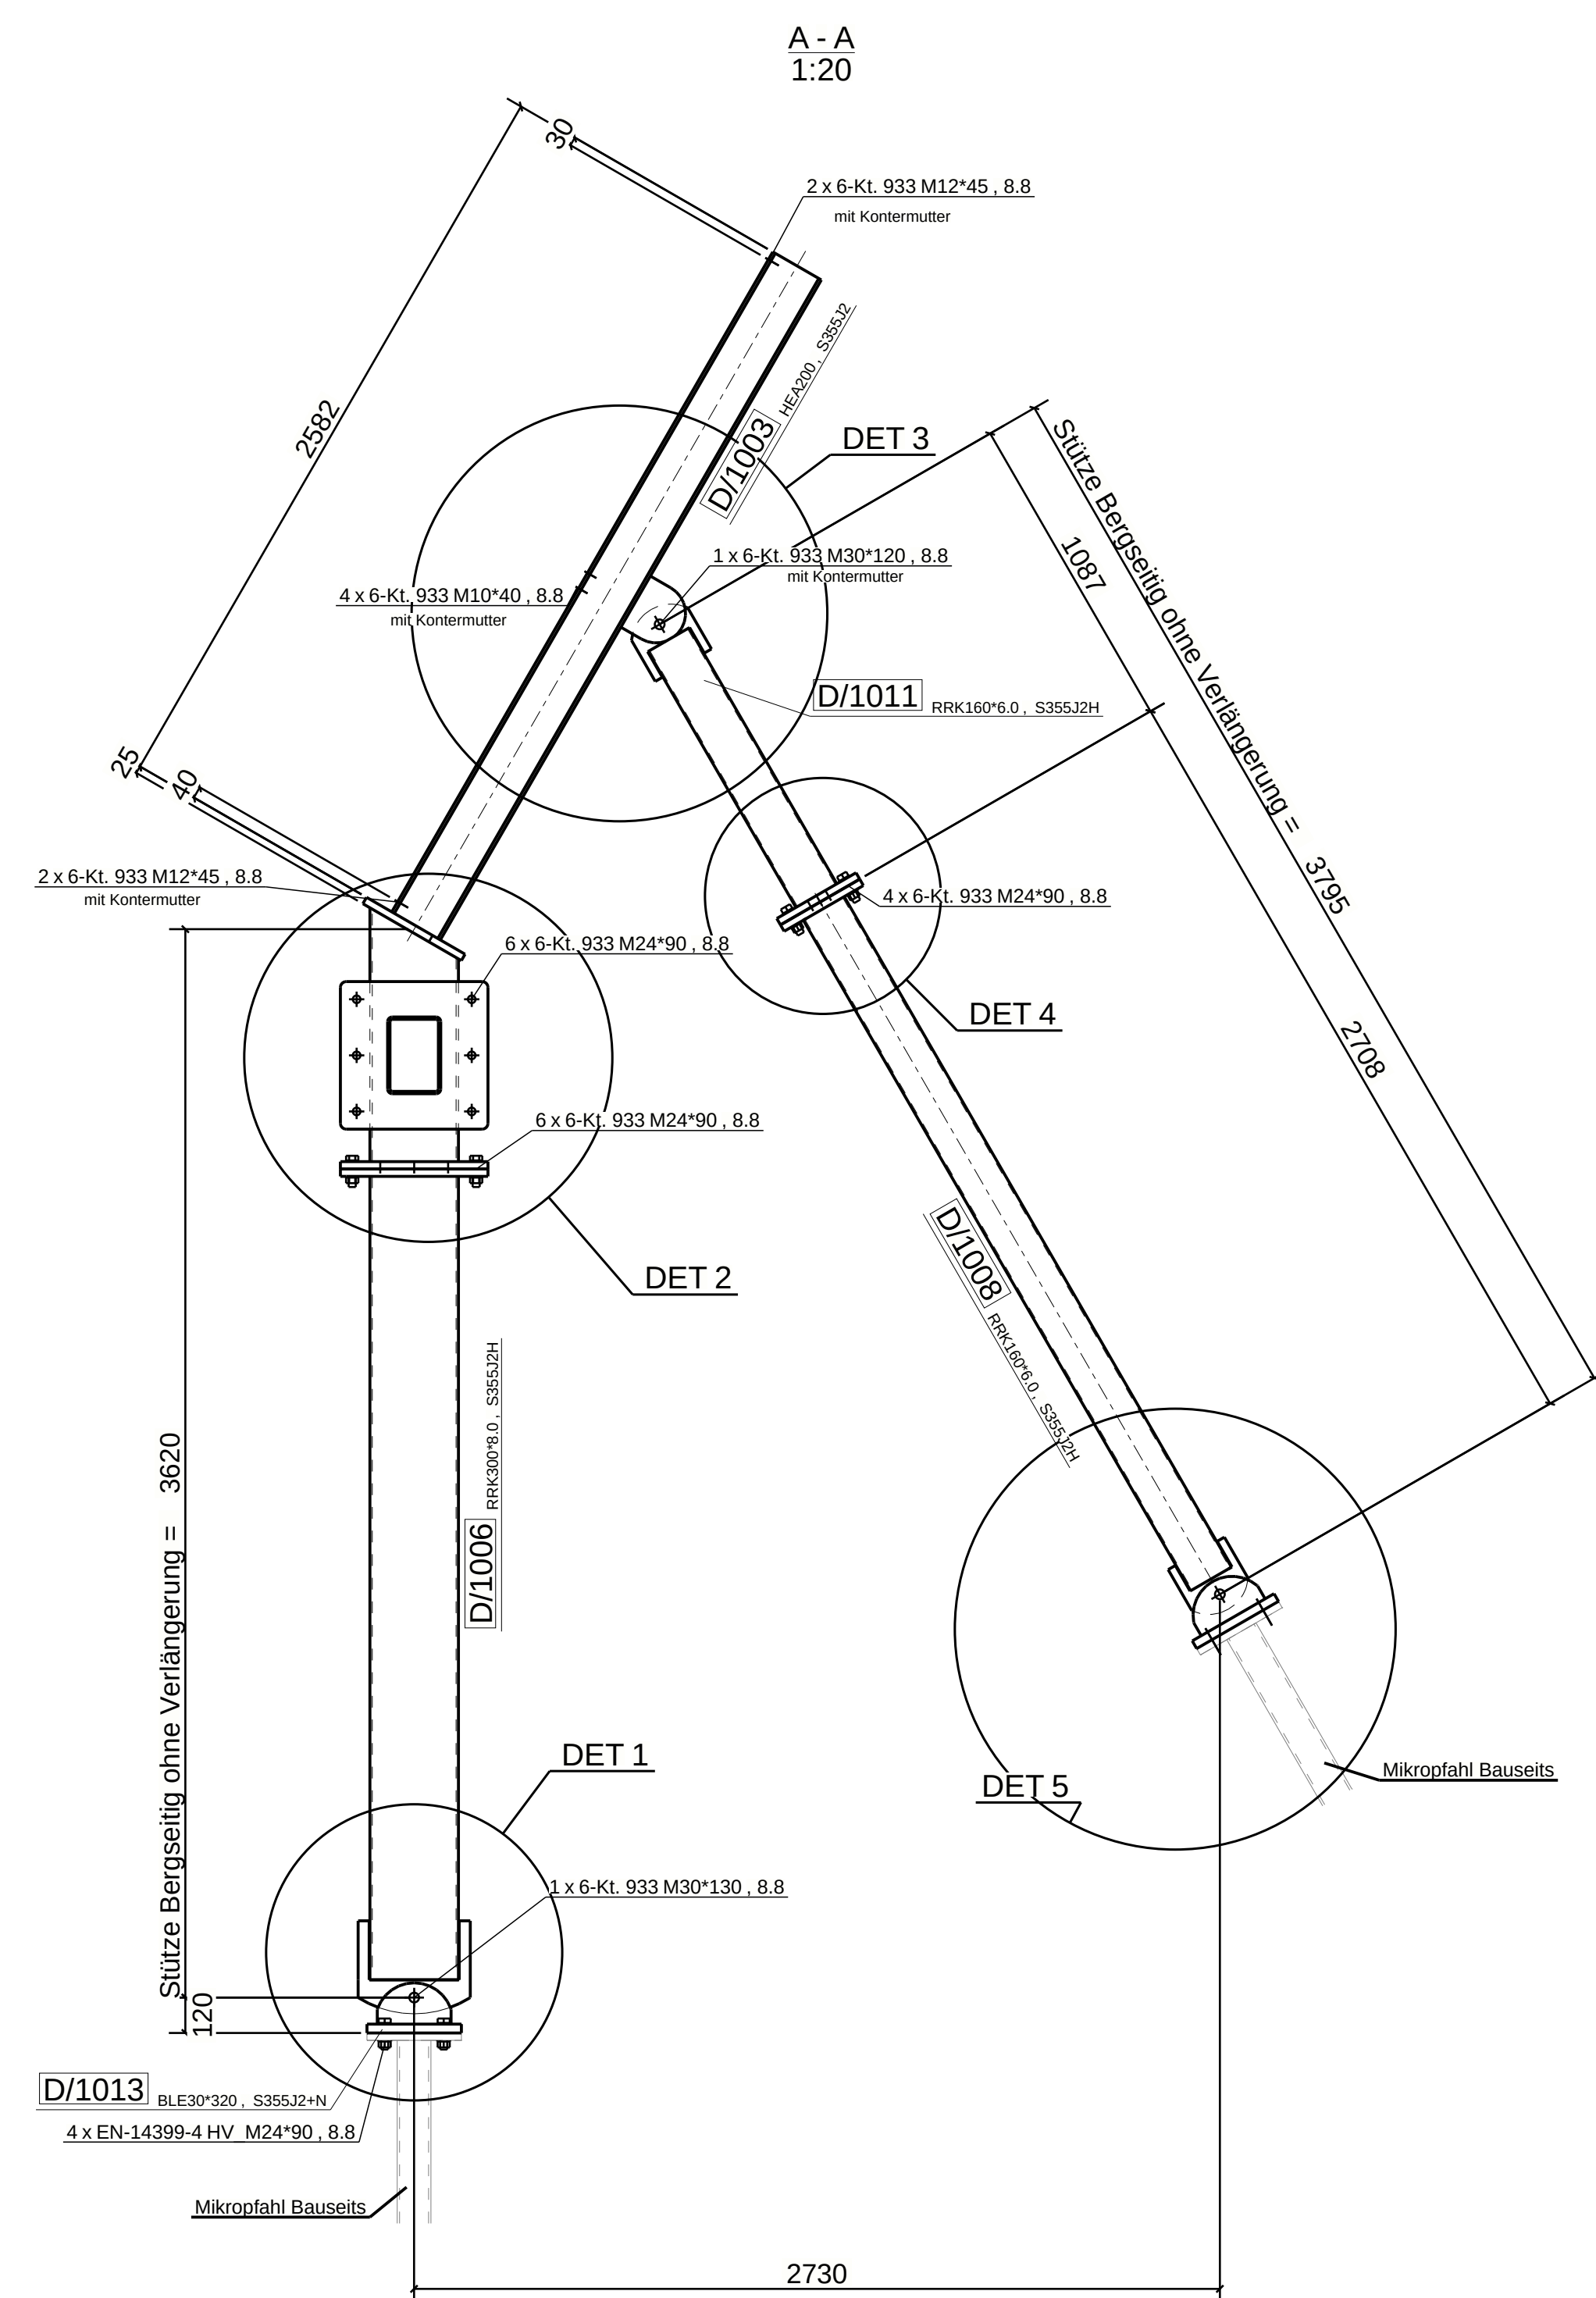
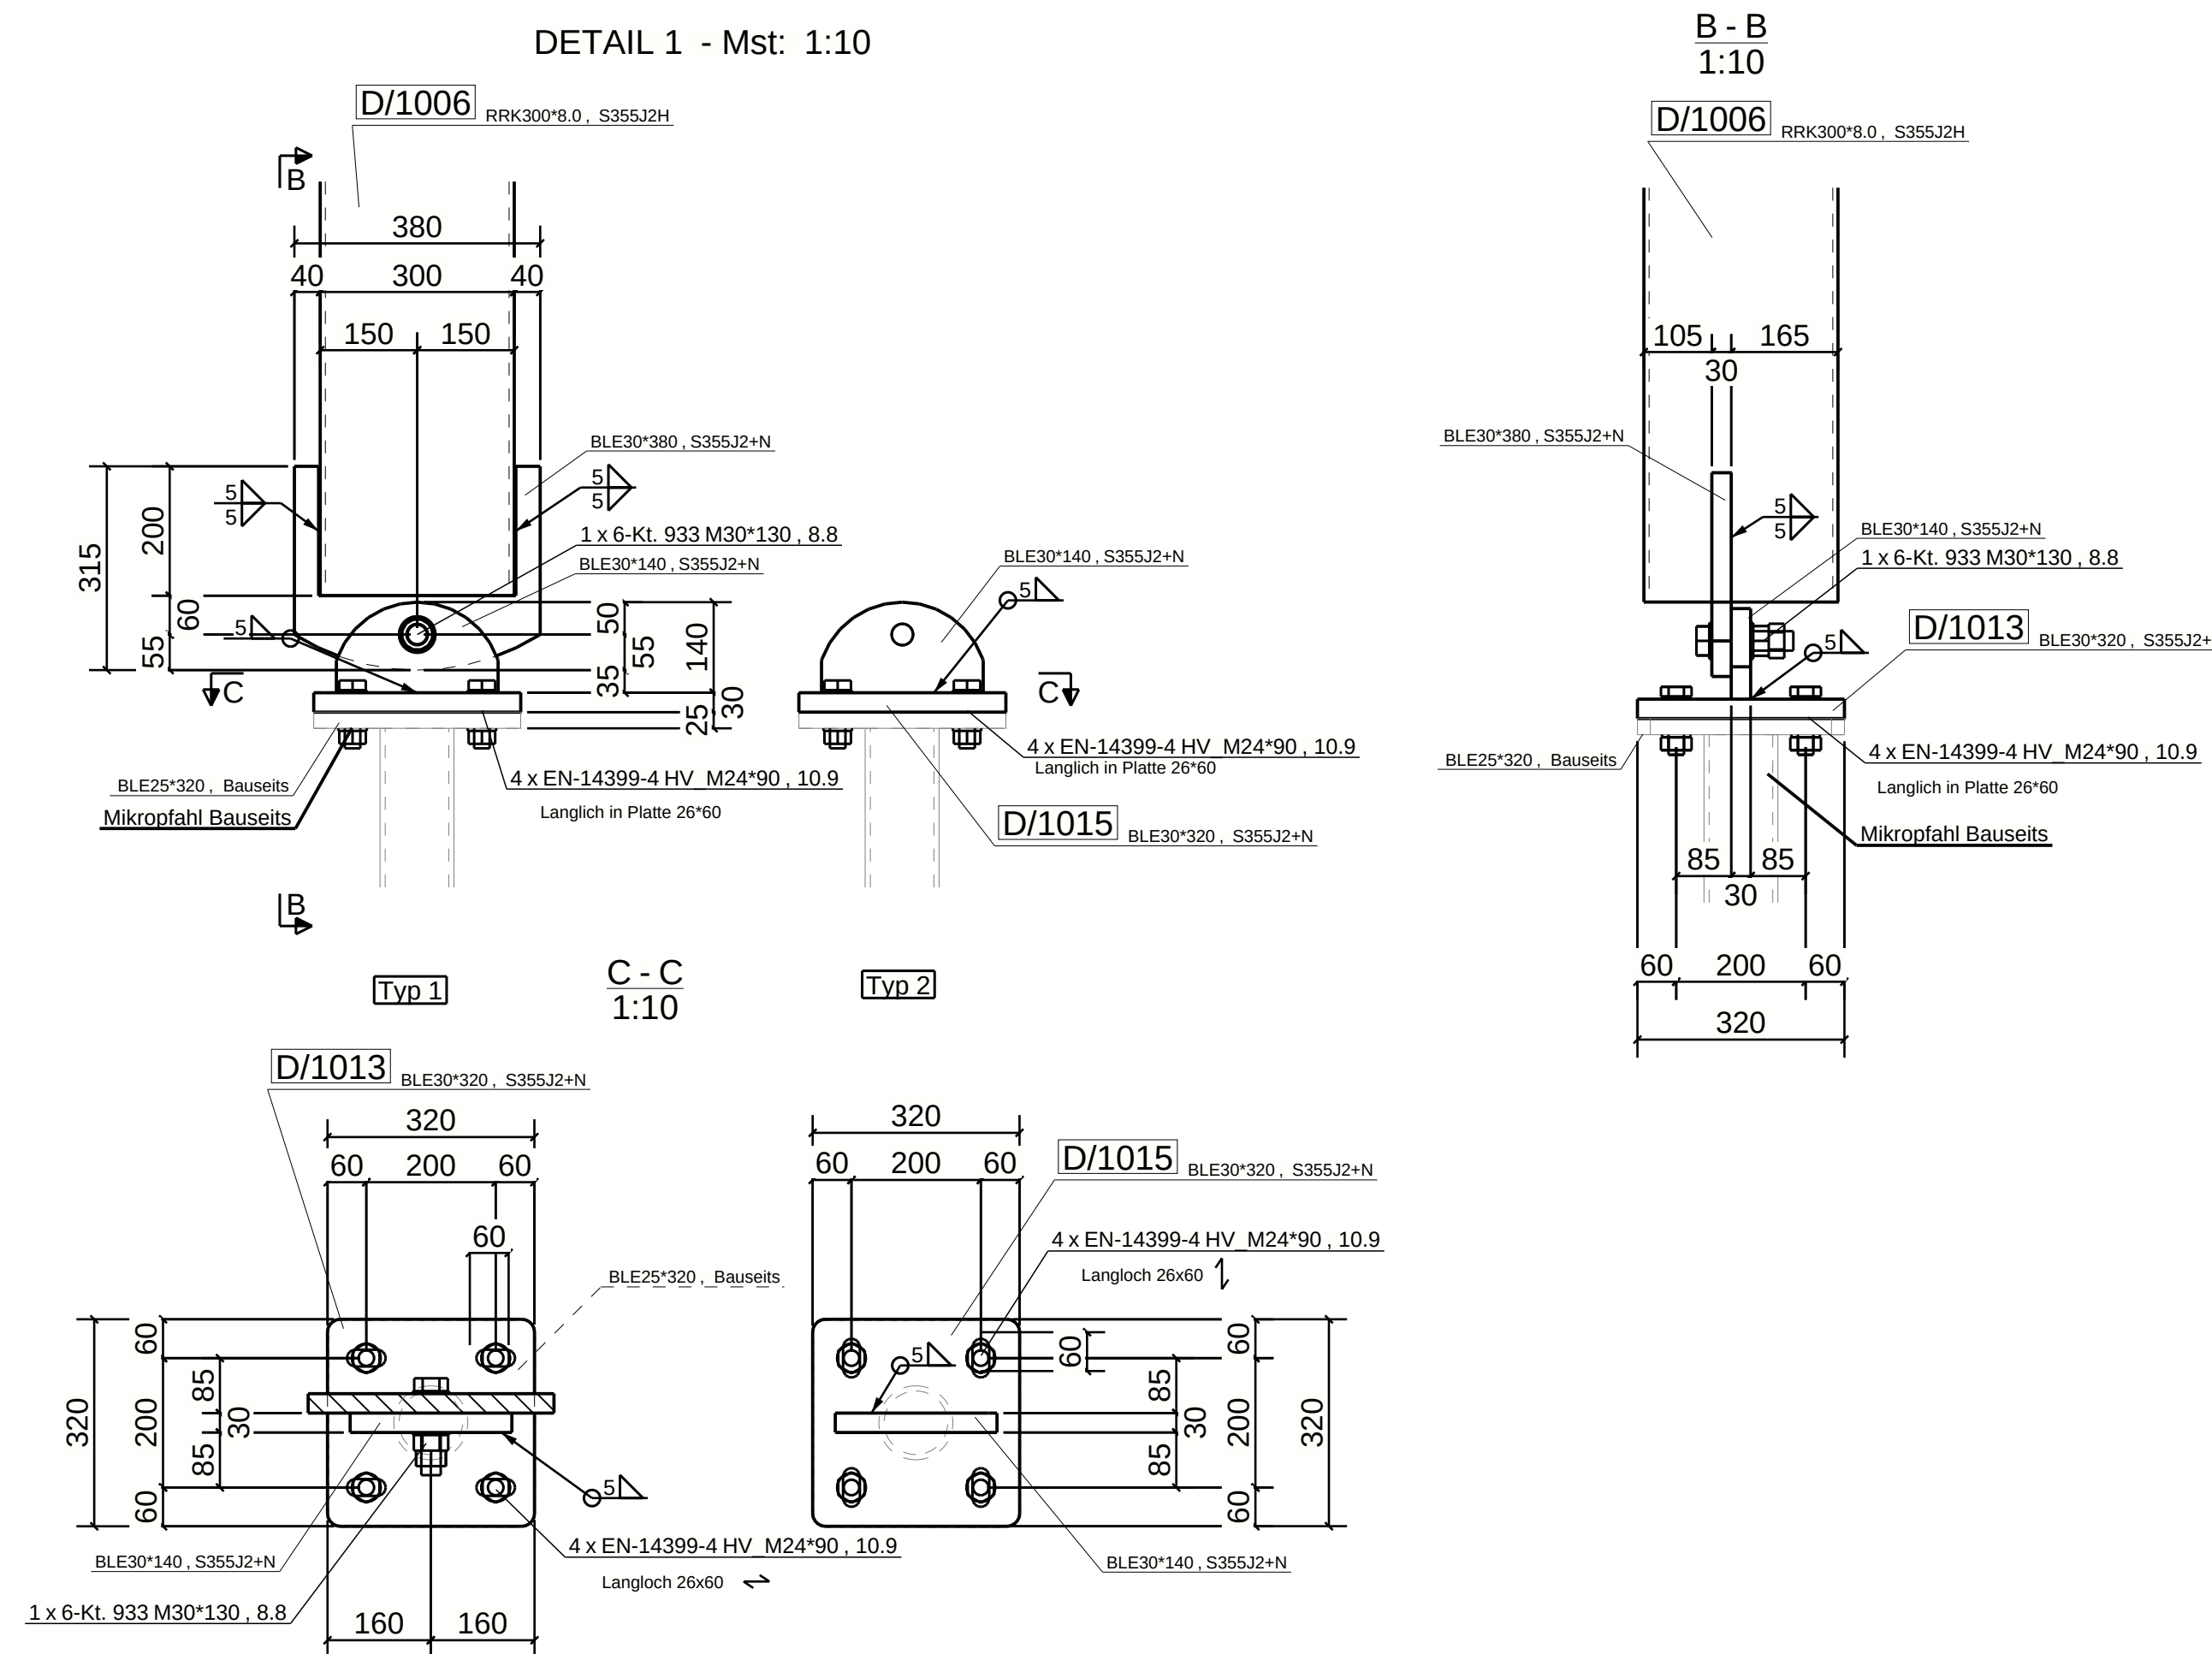


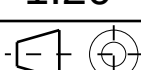

|   |            |                                                                                       |  |                                                                          |          |
|---|------------|---------------------------------------------------------------------------------------|--|--------------------------------------------------------------------------|----------|
| <b>Gesamte Konstruktion ist Roh</b>   |            |                                                                                       |  |                                                                          |          |
|   |            |                                                                                       |  |                                                                          |          |
| 9   |            |                                                                                       |  |                                                                          |          |
| B   | 07.08.2025 | Schraubenbeschriftung                                                                 |  |                                                                          | J. Mader |
| A   | 02.06.2025 | Detail 3 geändert                                                                     |  |                                                                          | P.Koch   |
| FREIEN   | KARLSTADT  | ANFORDERUNGSBEZEICHNUNG                                                               |  |                                                                          | WEGE     |
| <div style="text-align: center;">  <p><b>MAUCHLE STAHLBAU AG</b><br/>Industriestrasse 9    Tel. 041 925 12 51<br/>6210 SURSEE    info@mauchlestahlbau.ch</p> </div> |            |                                                                                       |  |                                                                          |          |
| Auftraggeber:   |            | 24027                                                                                 |  | BAUHERR                                                                  |          |
| Zeichner:   |            | PK                                                                                    |  | Axplo Solutions AG                                                       |          |
|   |            | interne Kontrolle                                                                     |  | BAUSTELLE                                                                |          |
| ABTEILUNG:   |            | UNTERSCHRIFT                                                                          |  | NapSolar                                                                 |          |
|   |            |                                                                                       |  | BENENNUNG                                                                |          |
|   |            |                                                                                       |  | Primärkonstruktion Typ D                                                 |          |
|   |            |                                                                                       |  | Ansicht, Schnitte & Details                                              |          |
| PL   |            | L. Durrer                                                                             |  |                                                                          |          |
| MAISTAB   |            | 1:10    1:20    1:55                                                                  |  | ZEICHNUNGSNUMMER                                                         |          |
| ANSICHT   |            |  |  | S O M 004 B                                                              |          |
|   |            |                                                                                       |  | PROJEKTANT    KONT.    VERIFIED    VERGEBER/BAUBEREITUNG-NET    REVISION |          |