
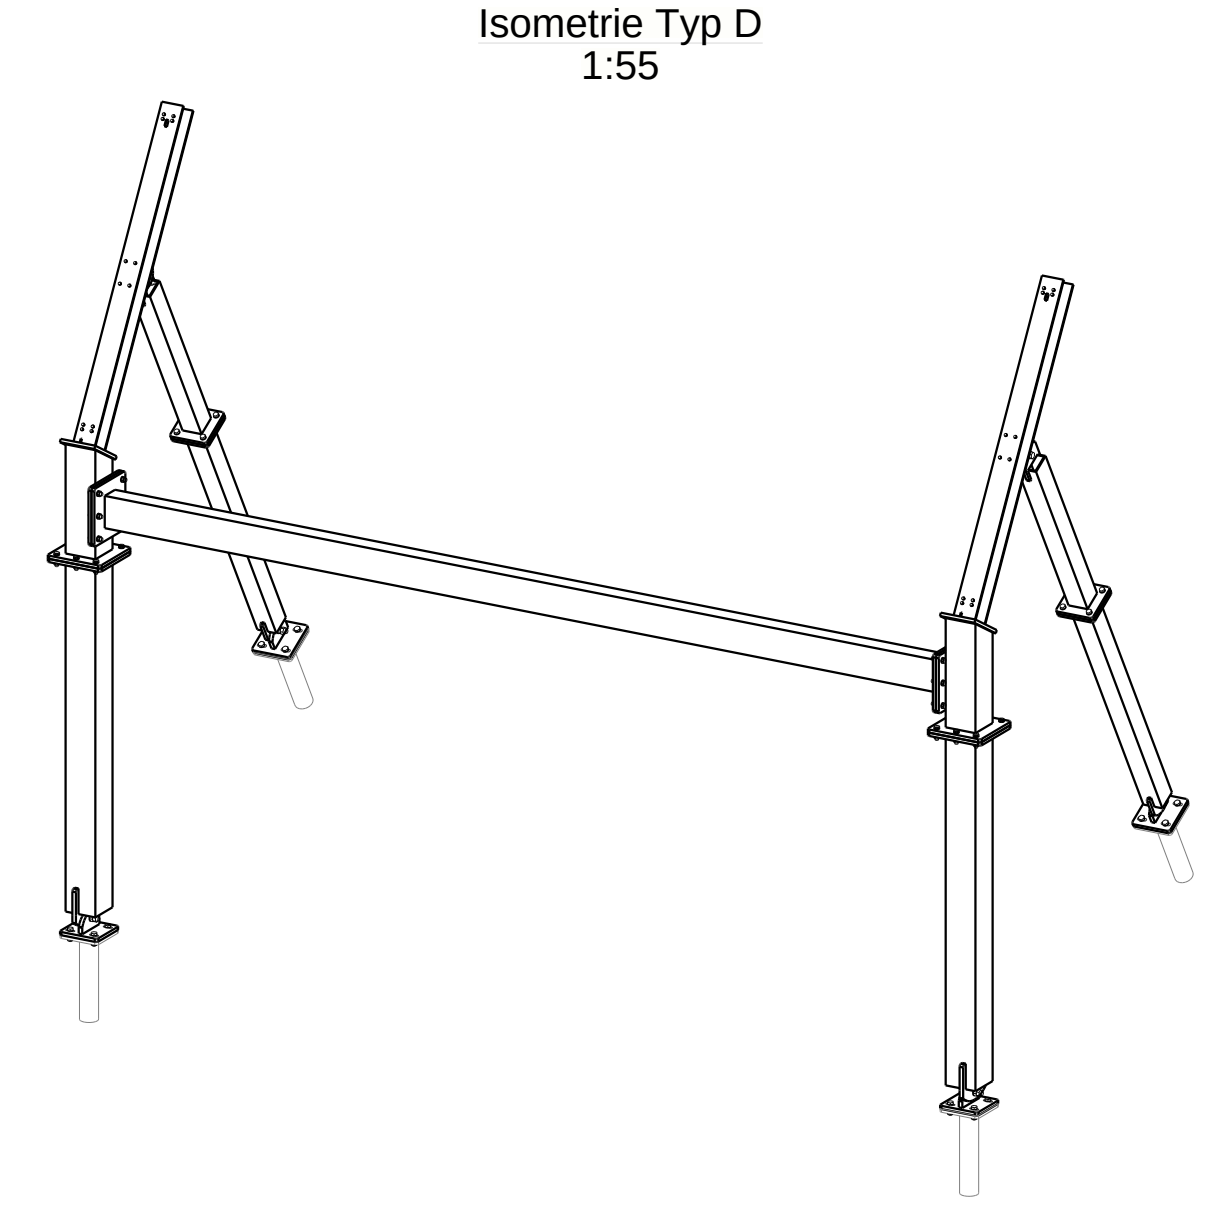
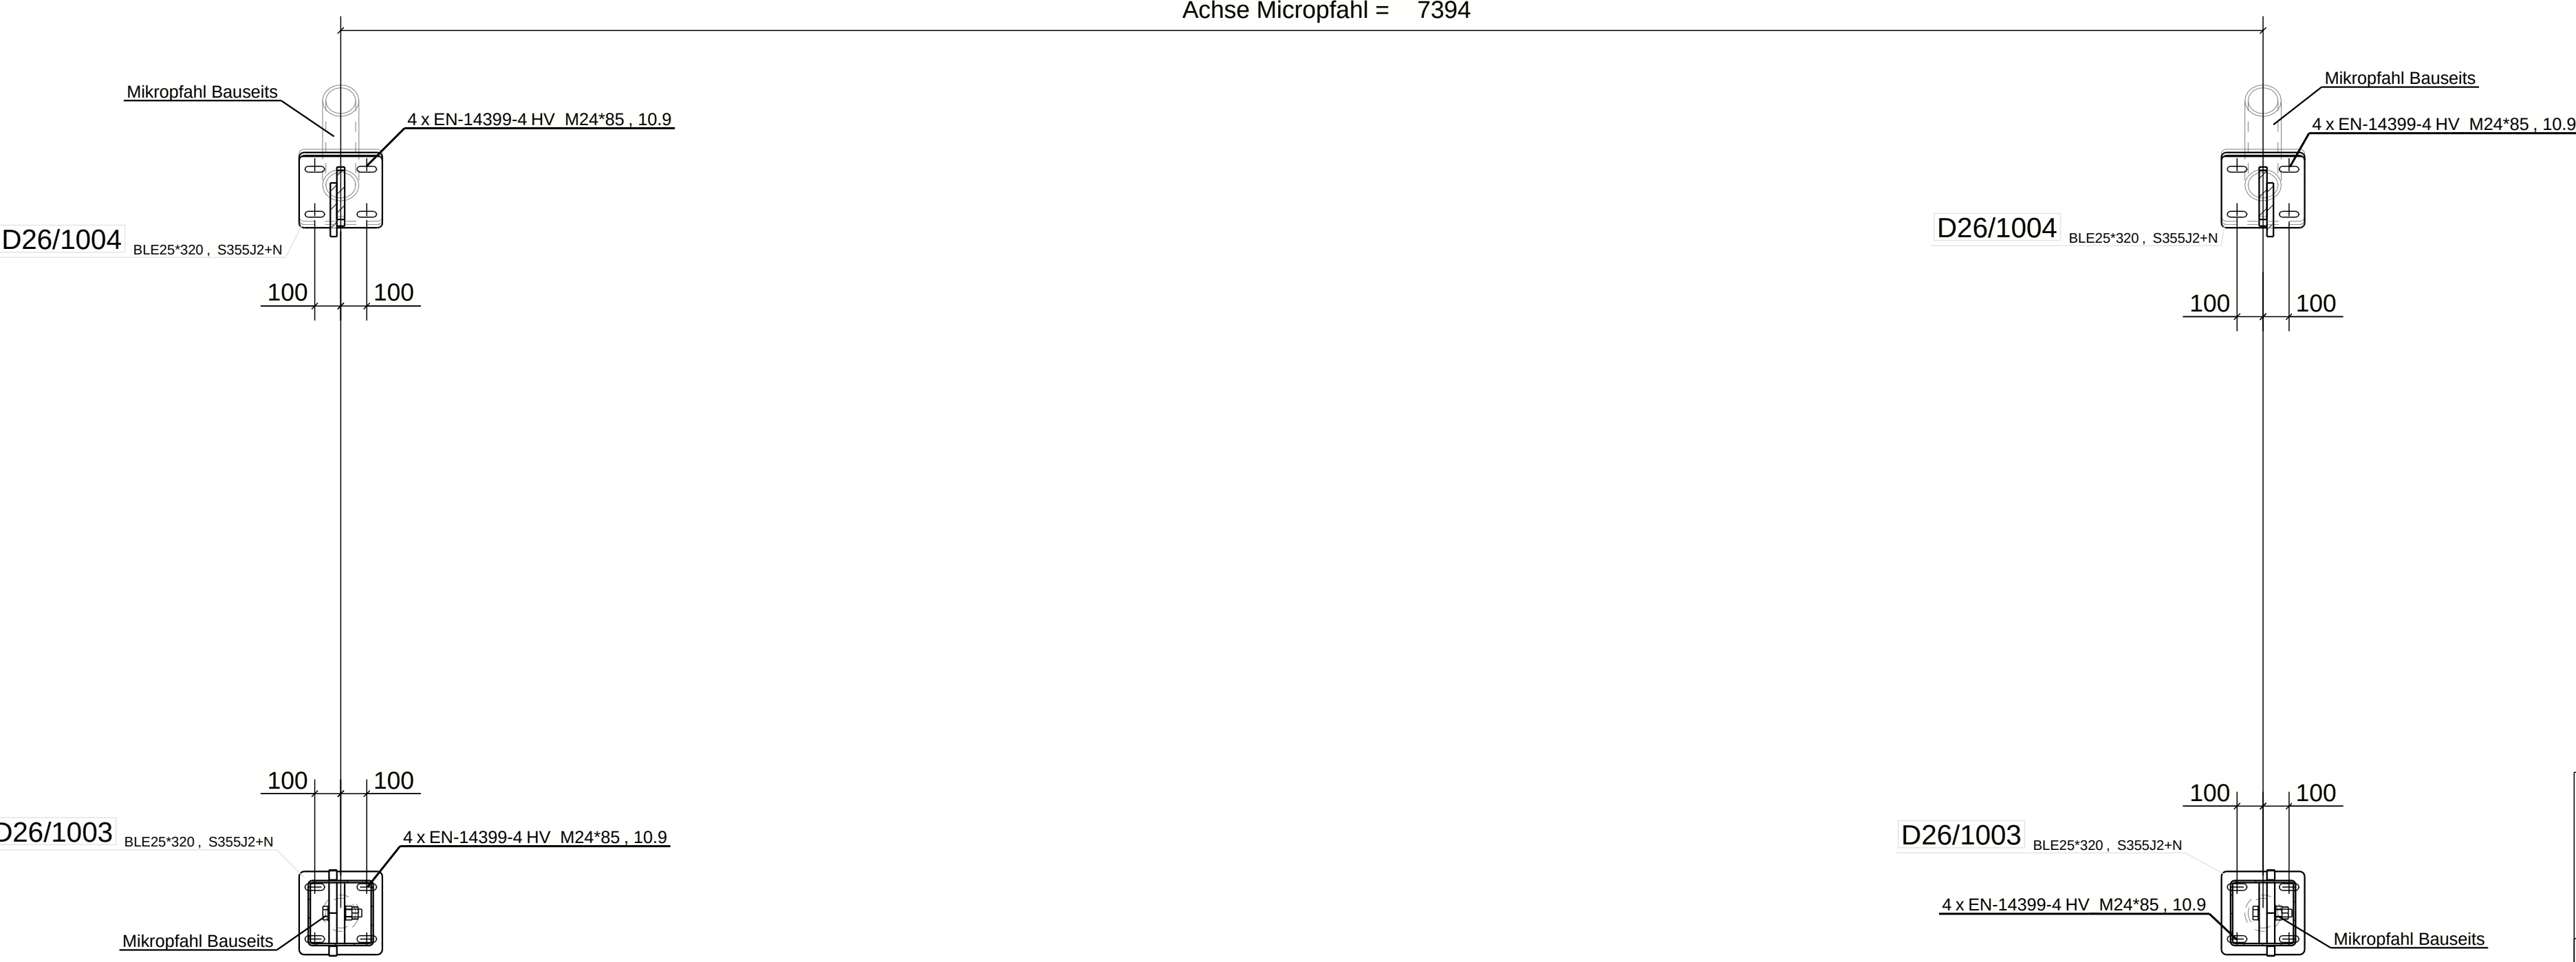
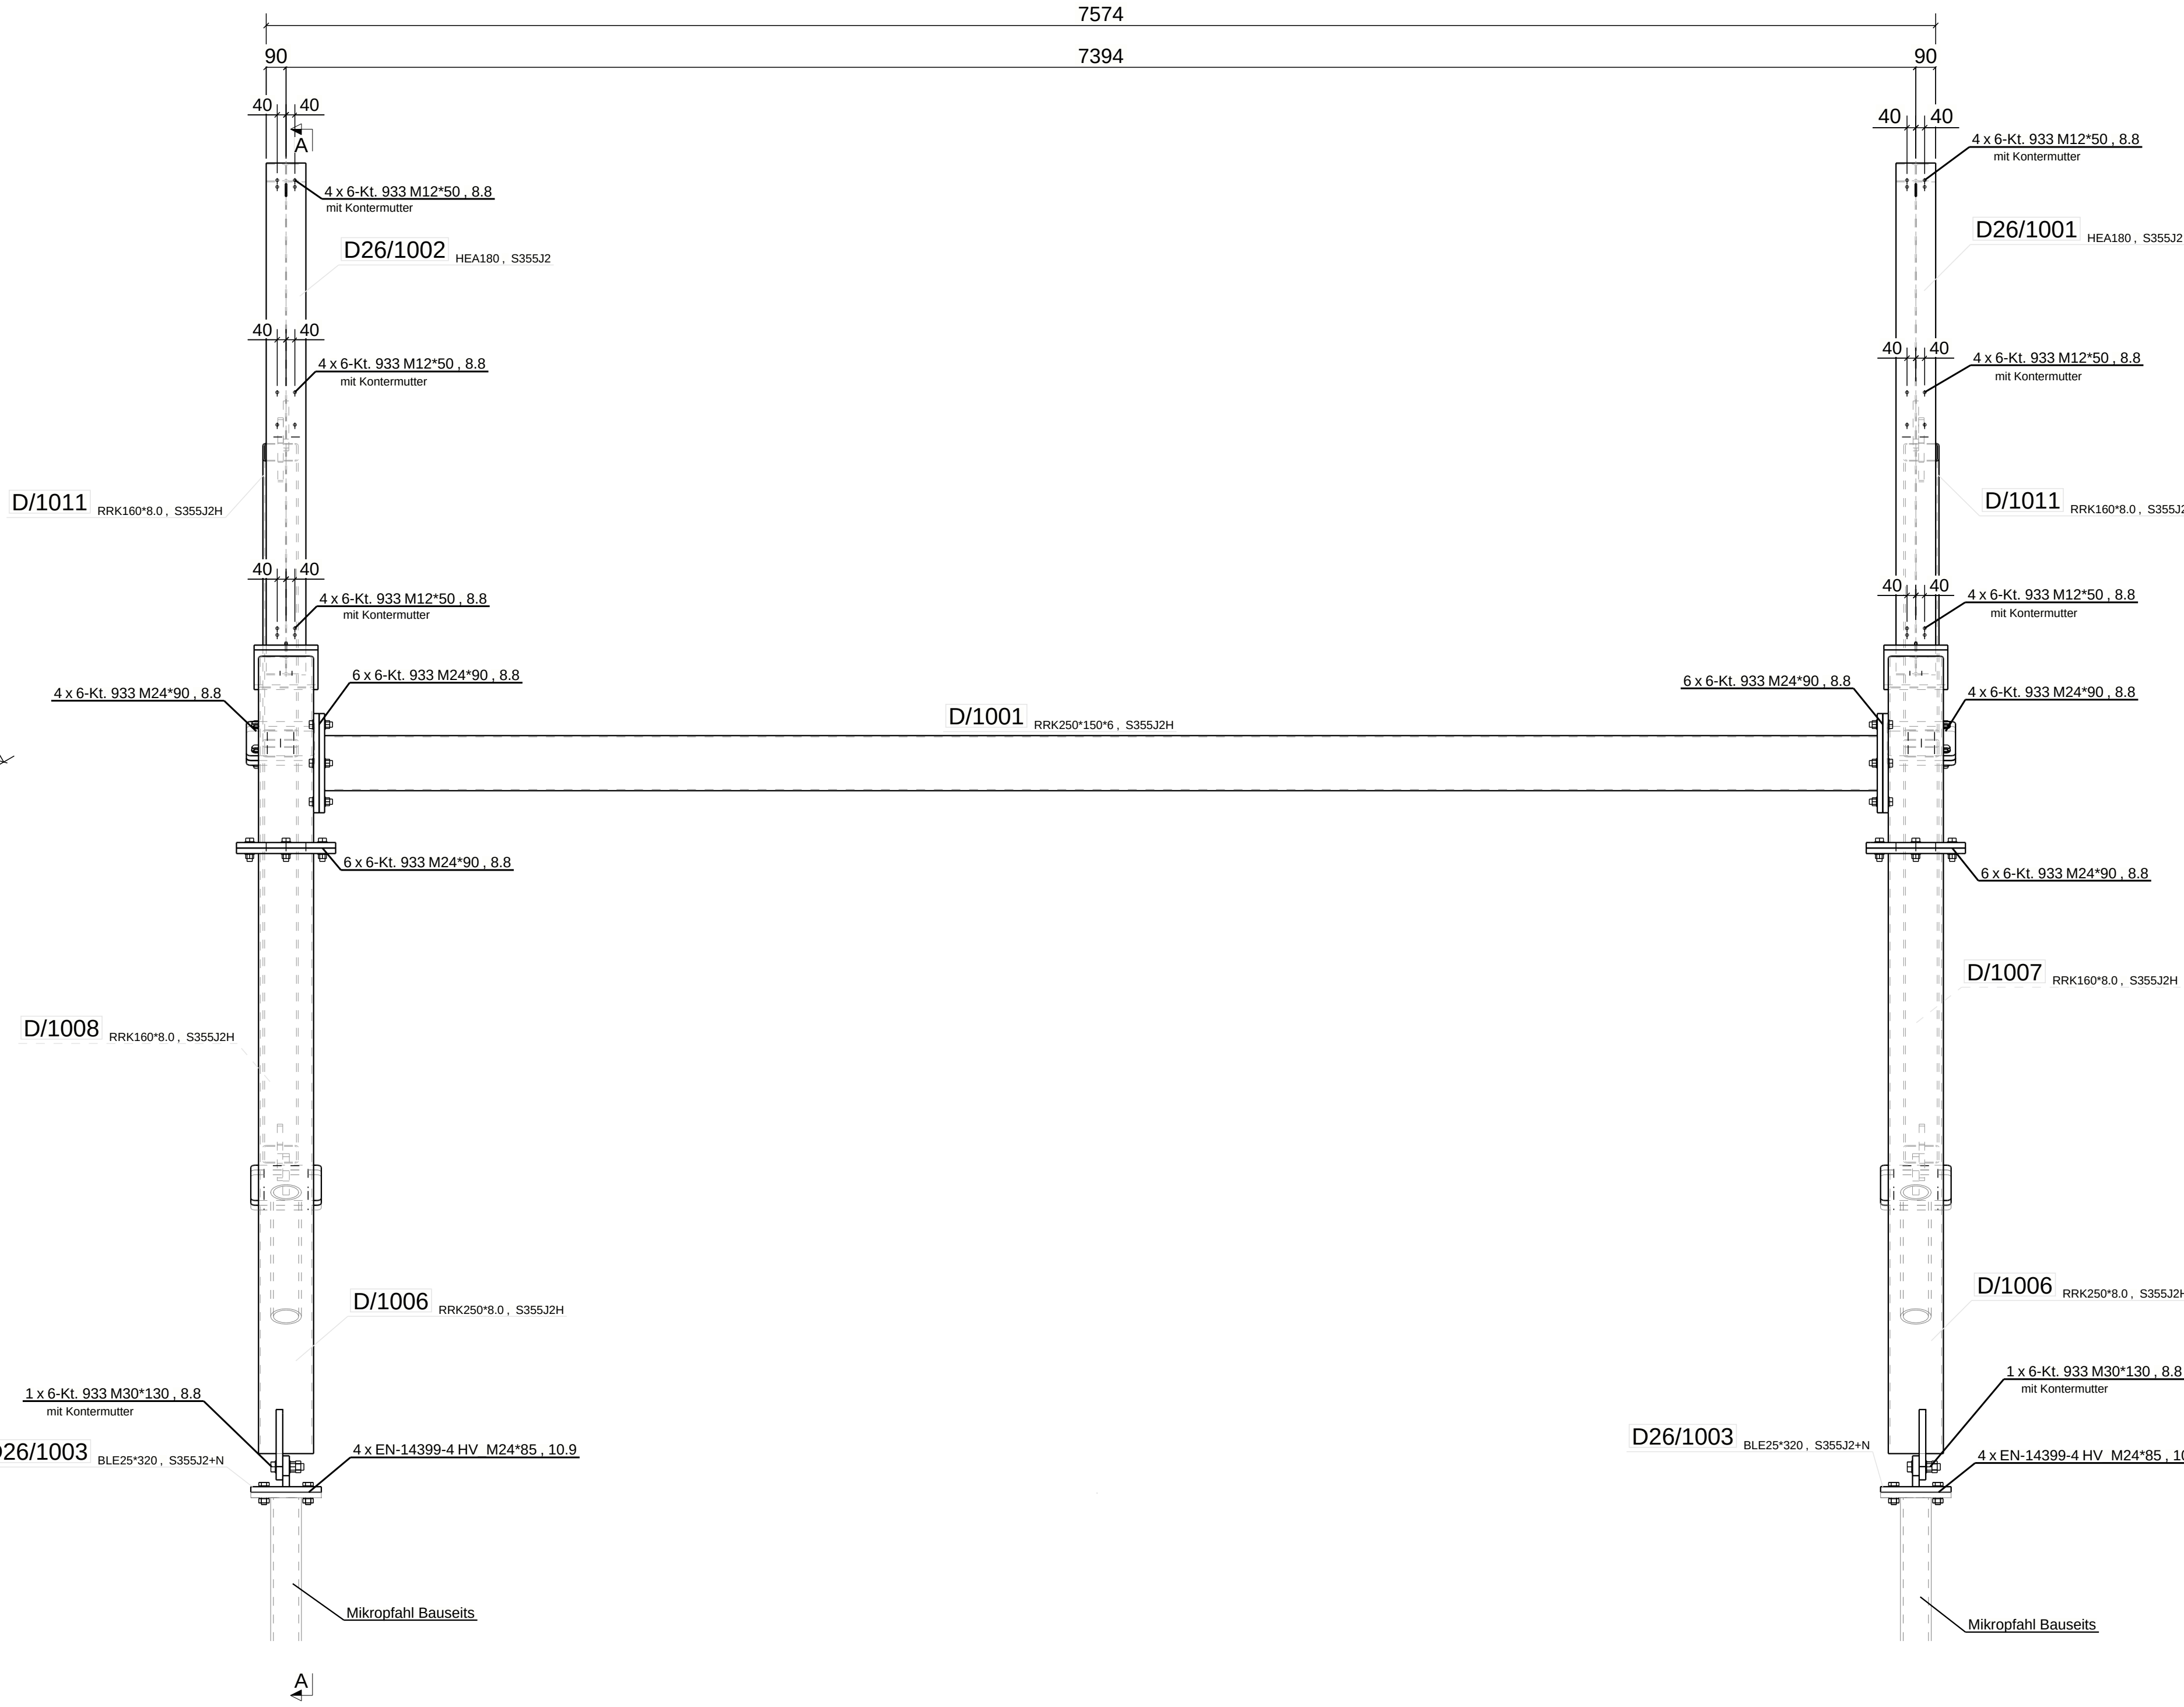
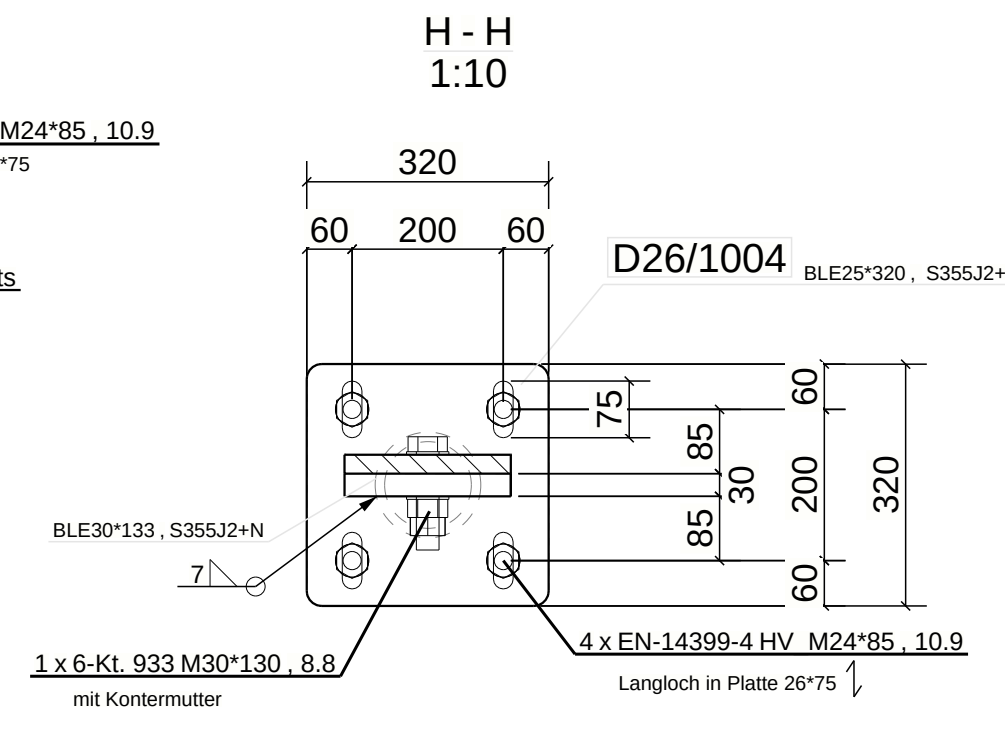
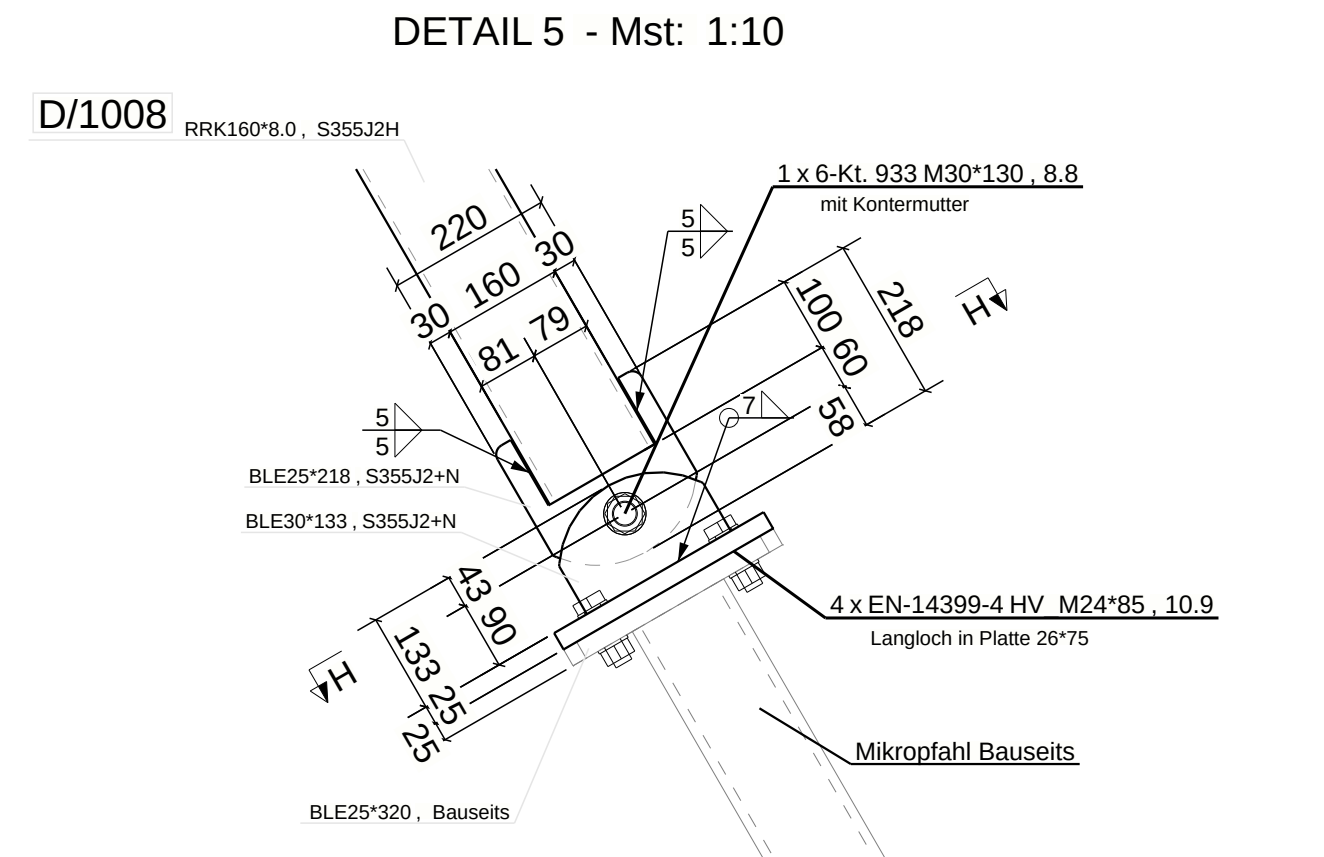
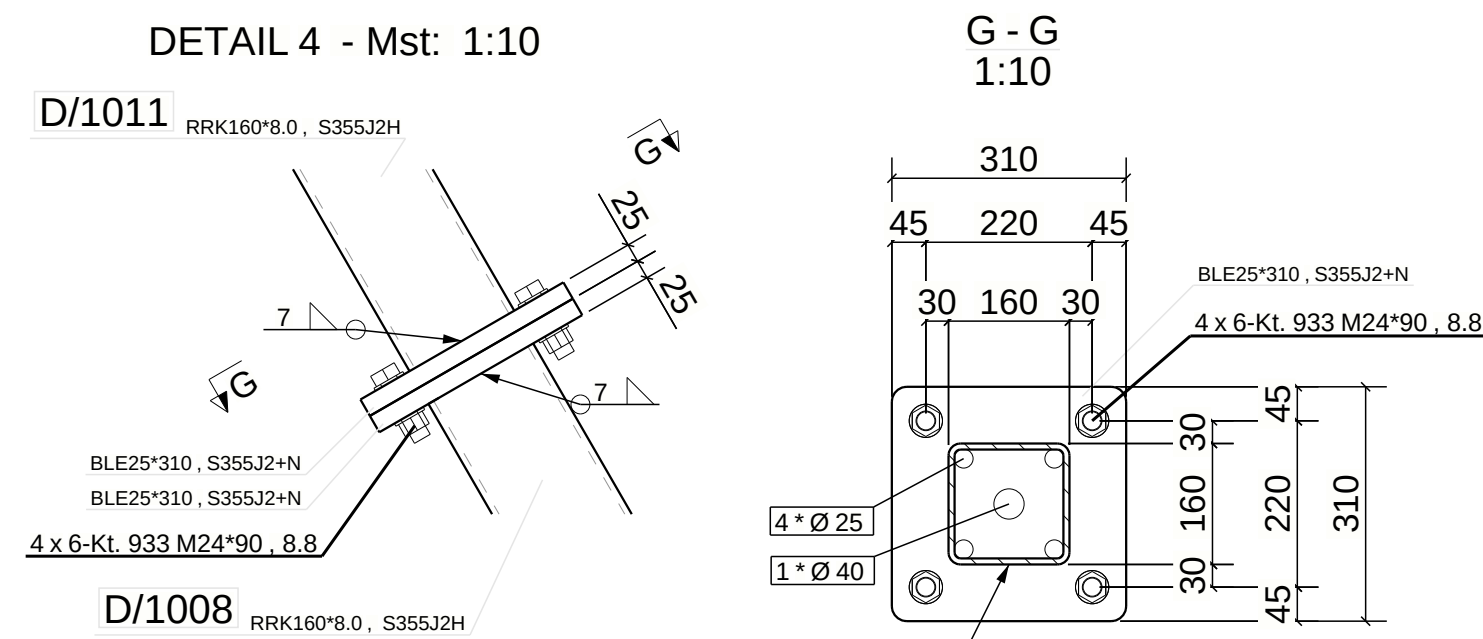
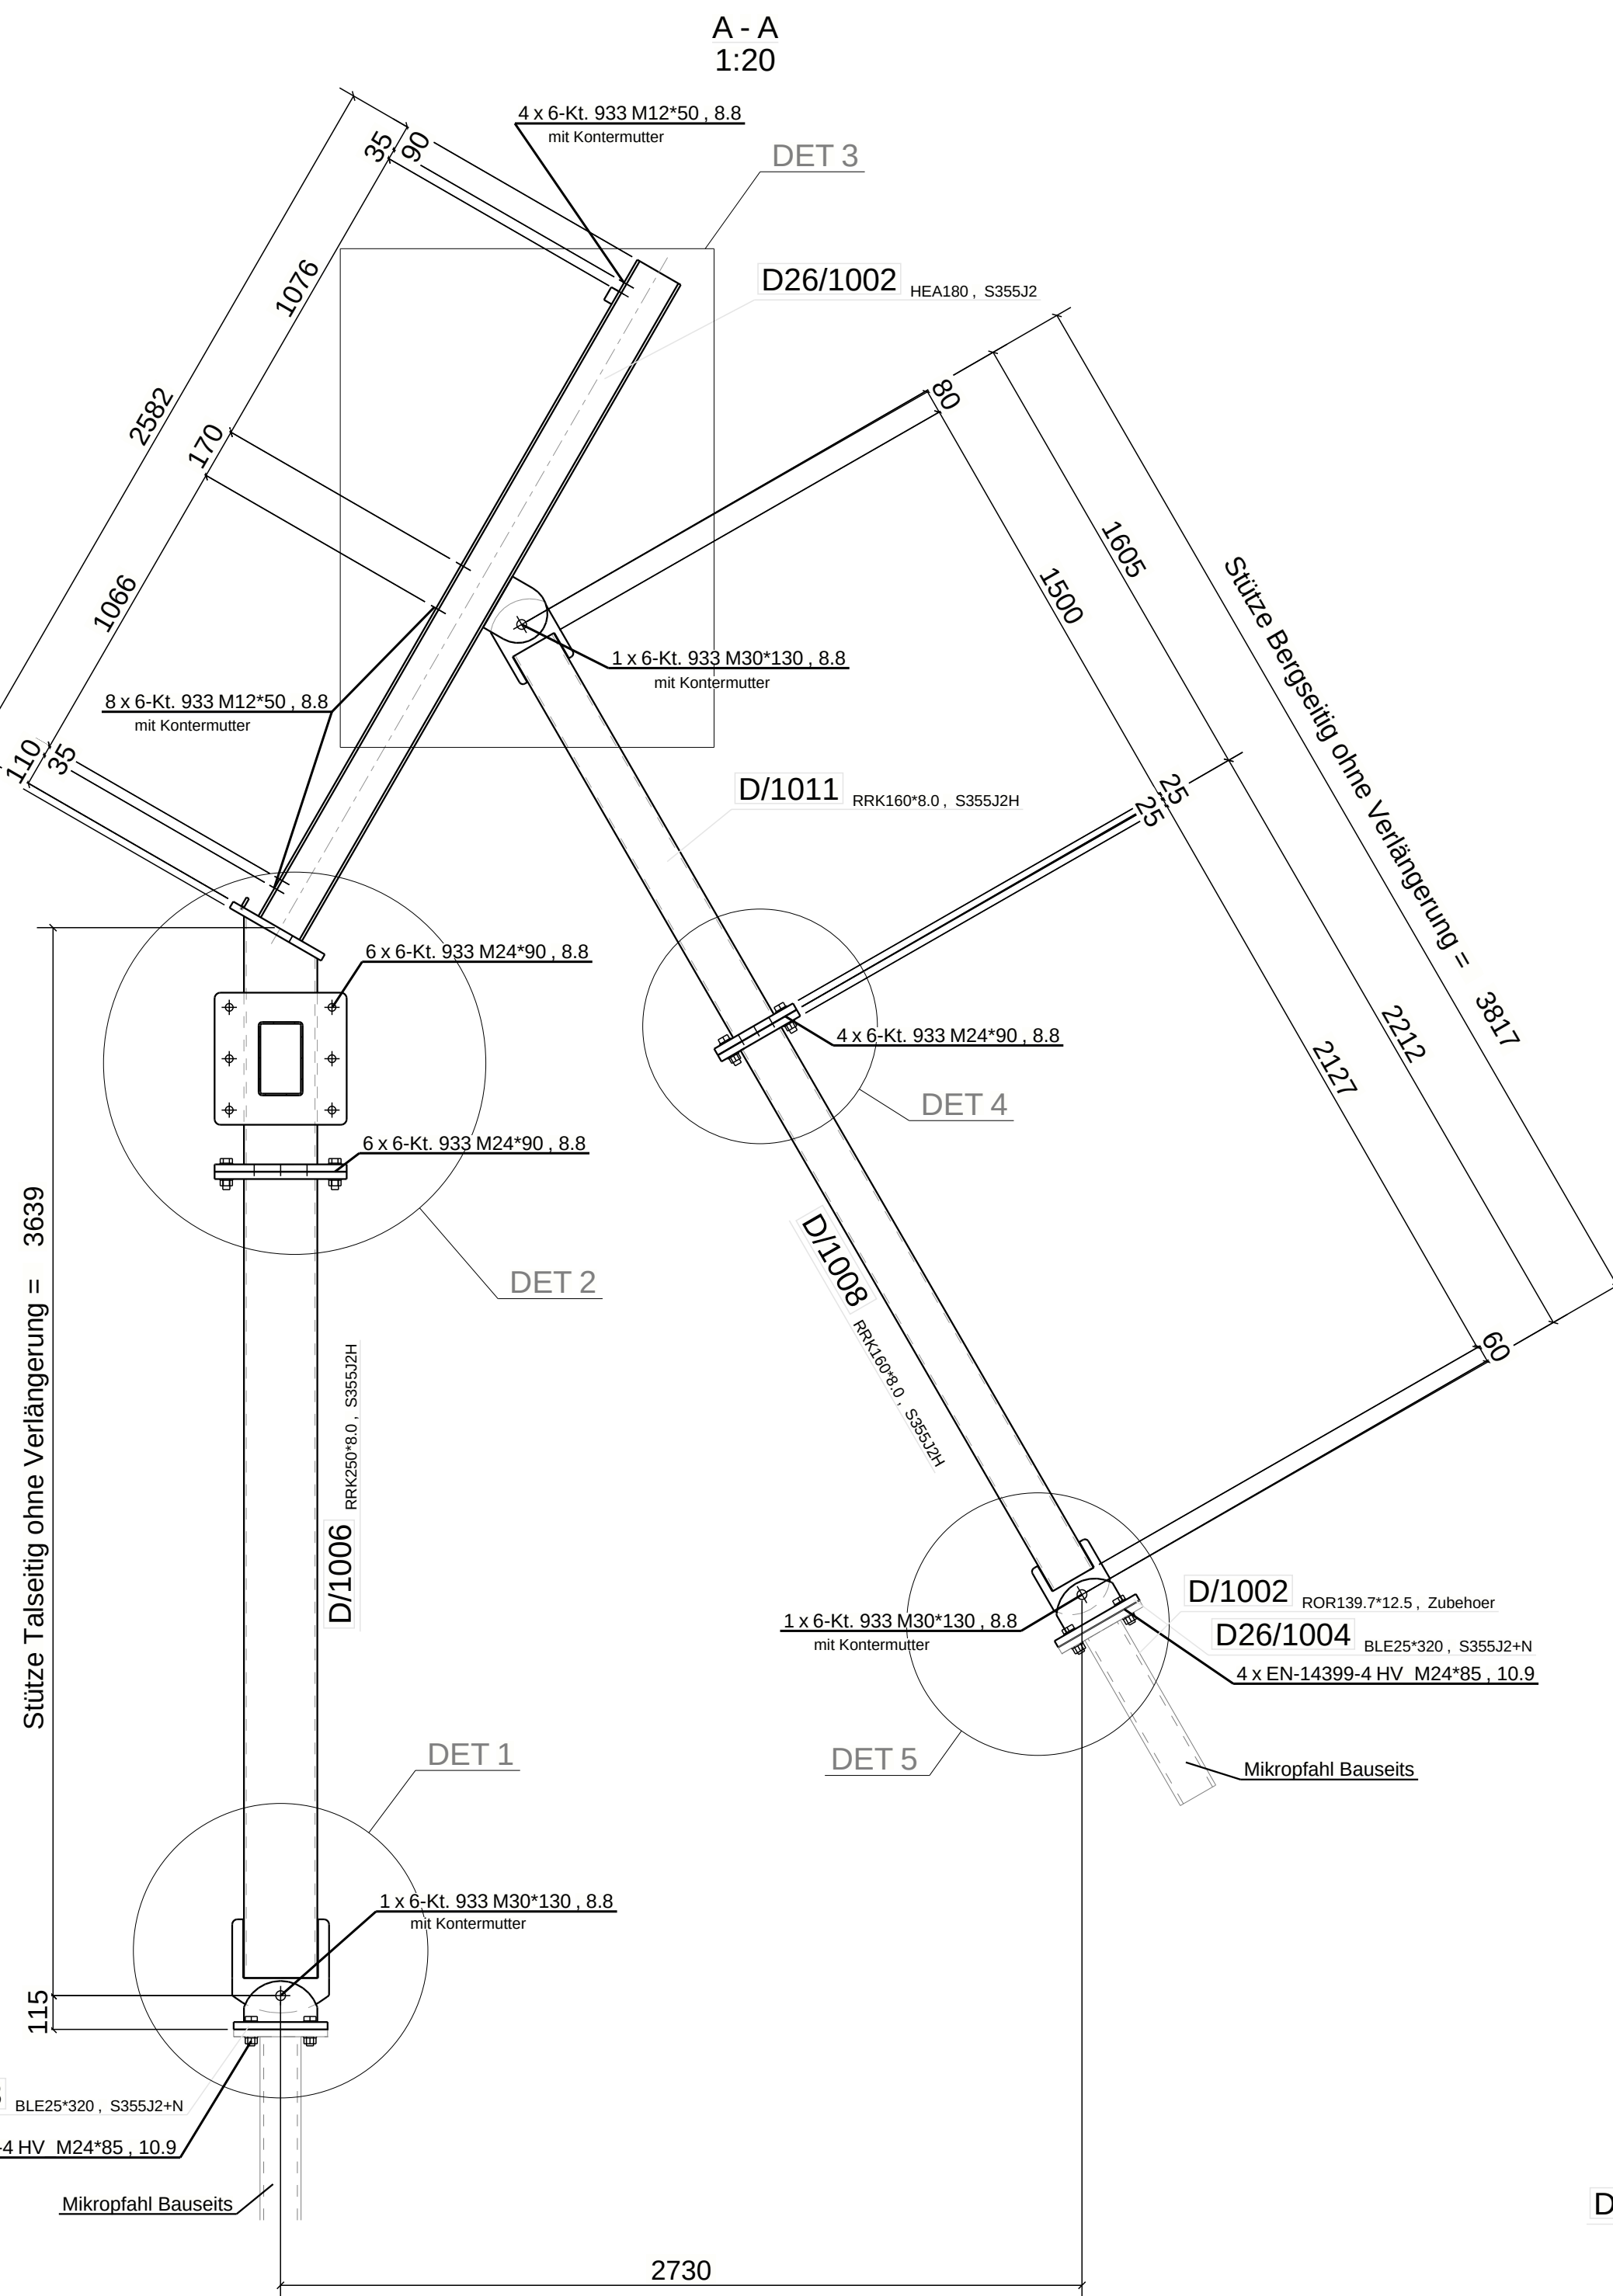
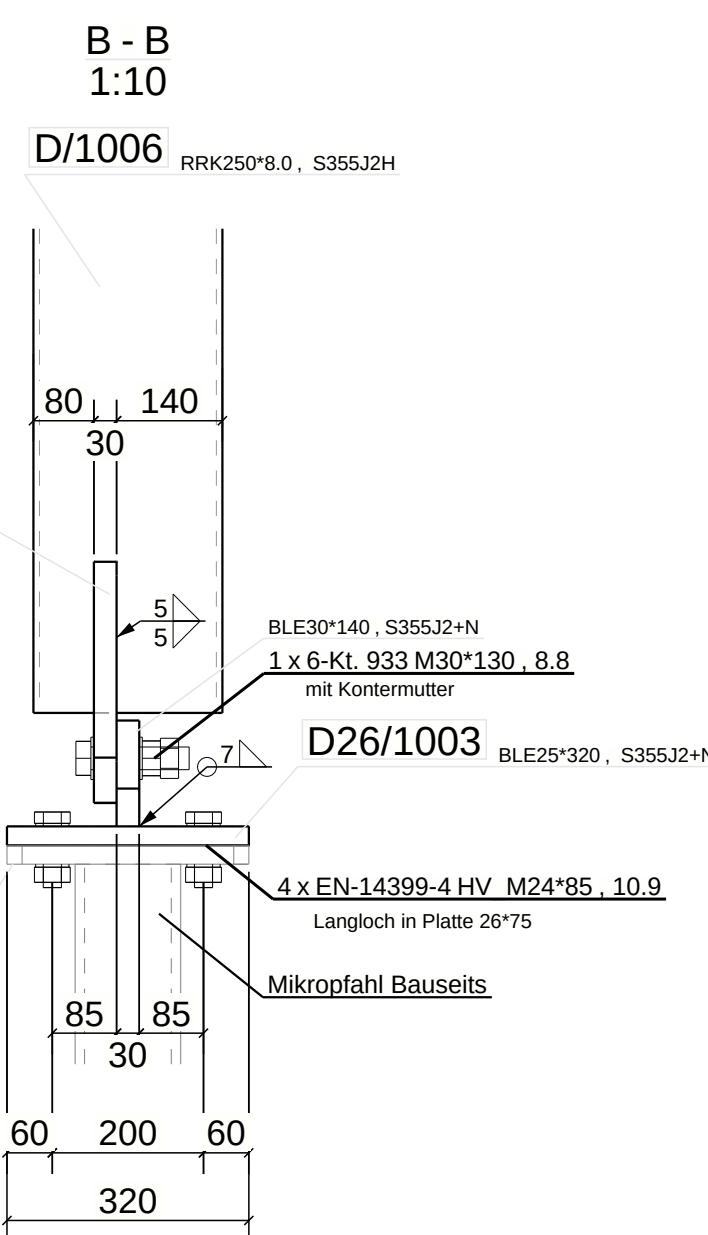
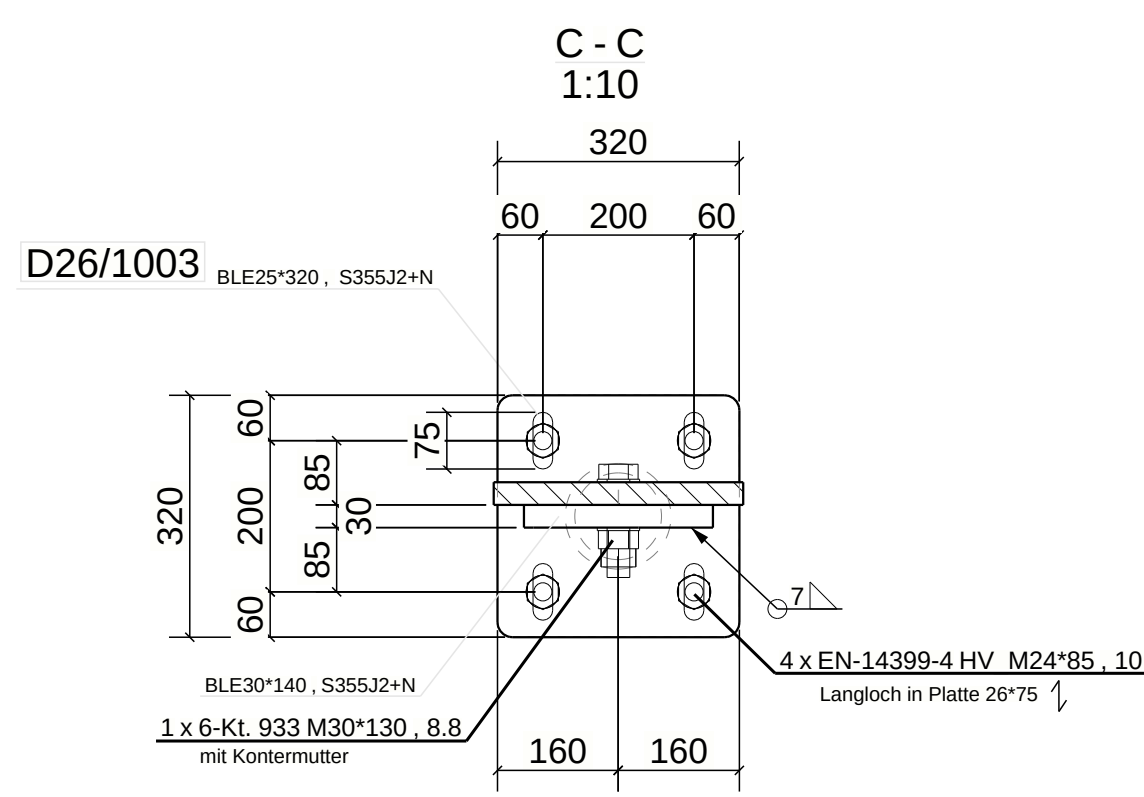
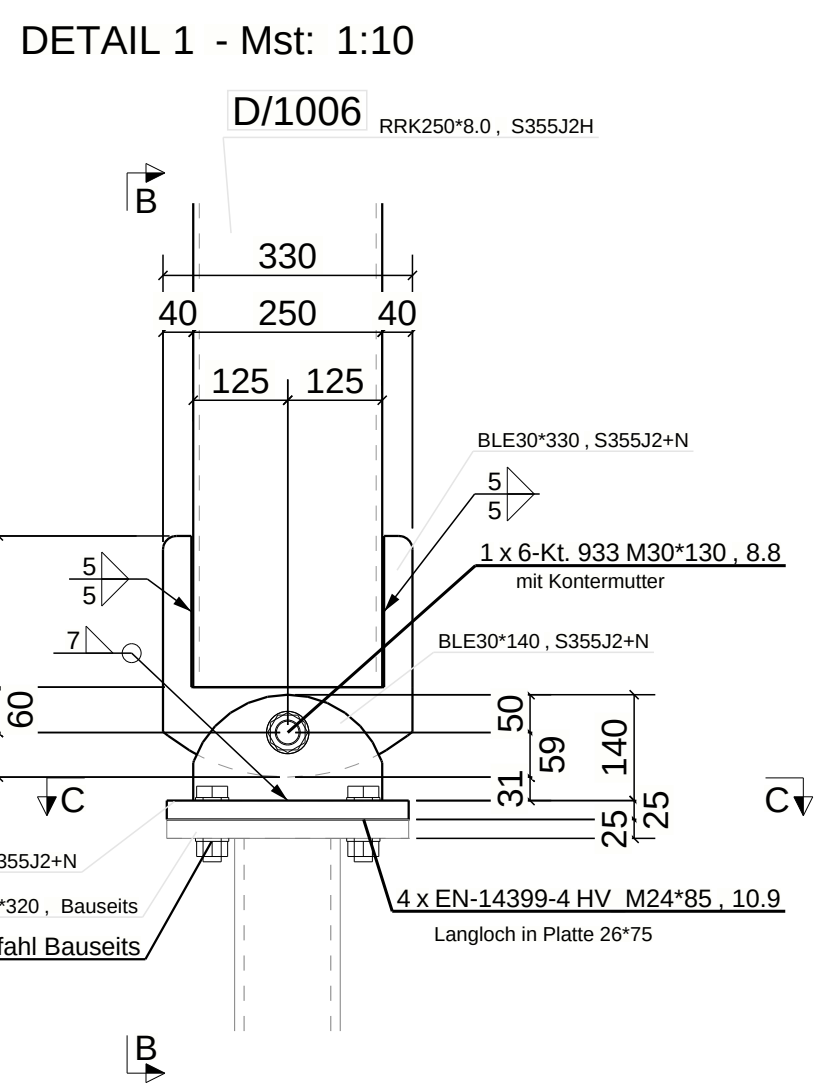
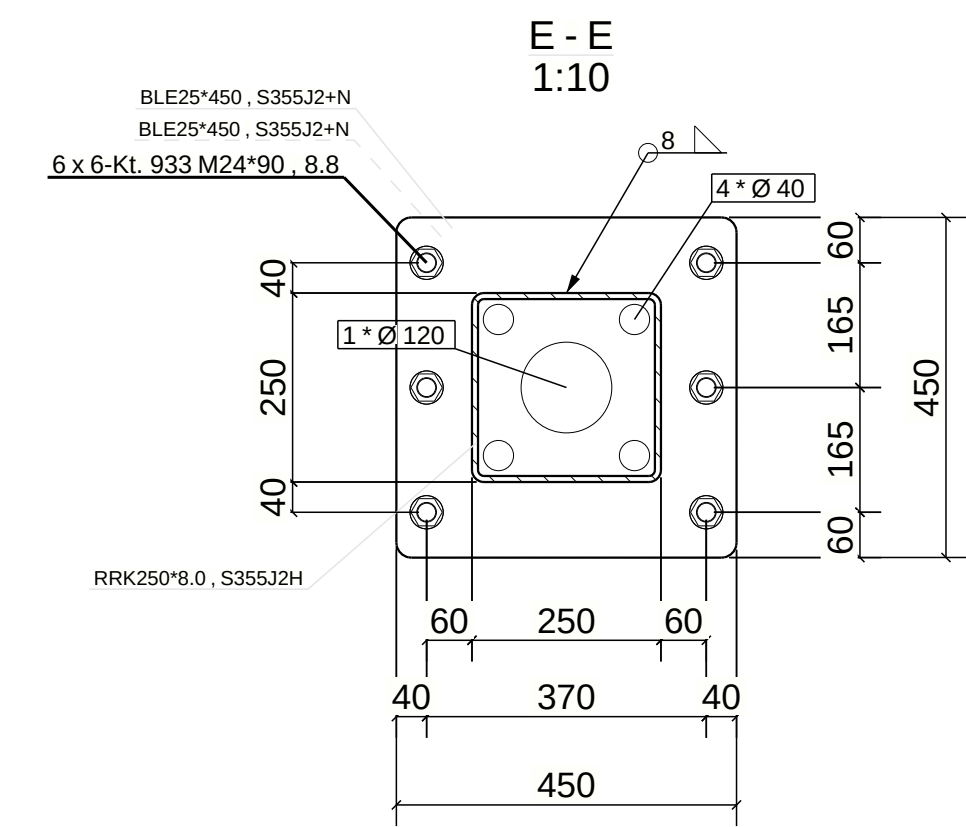
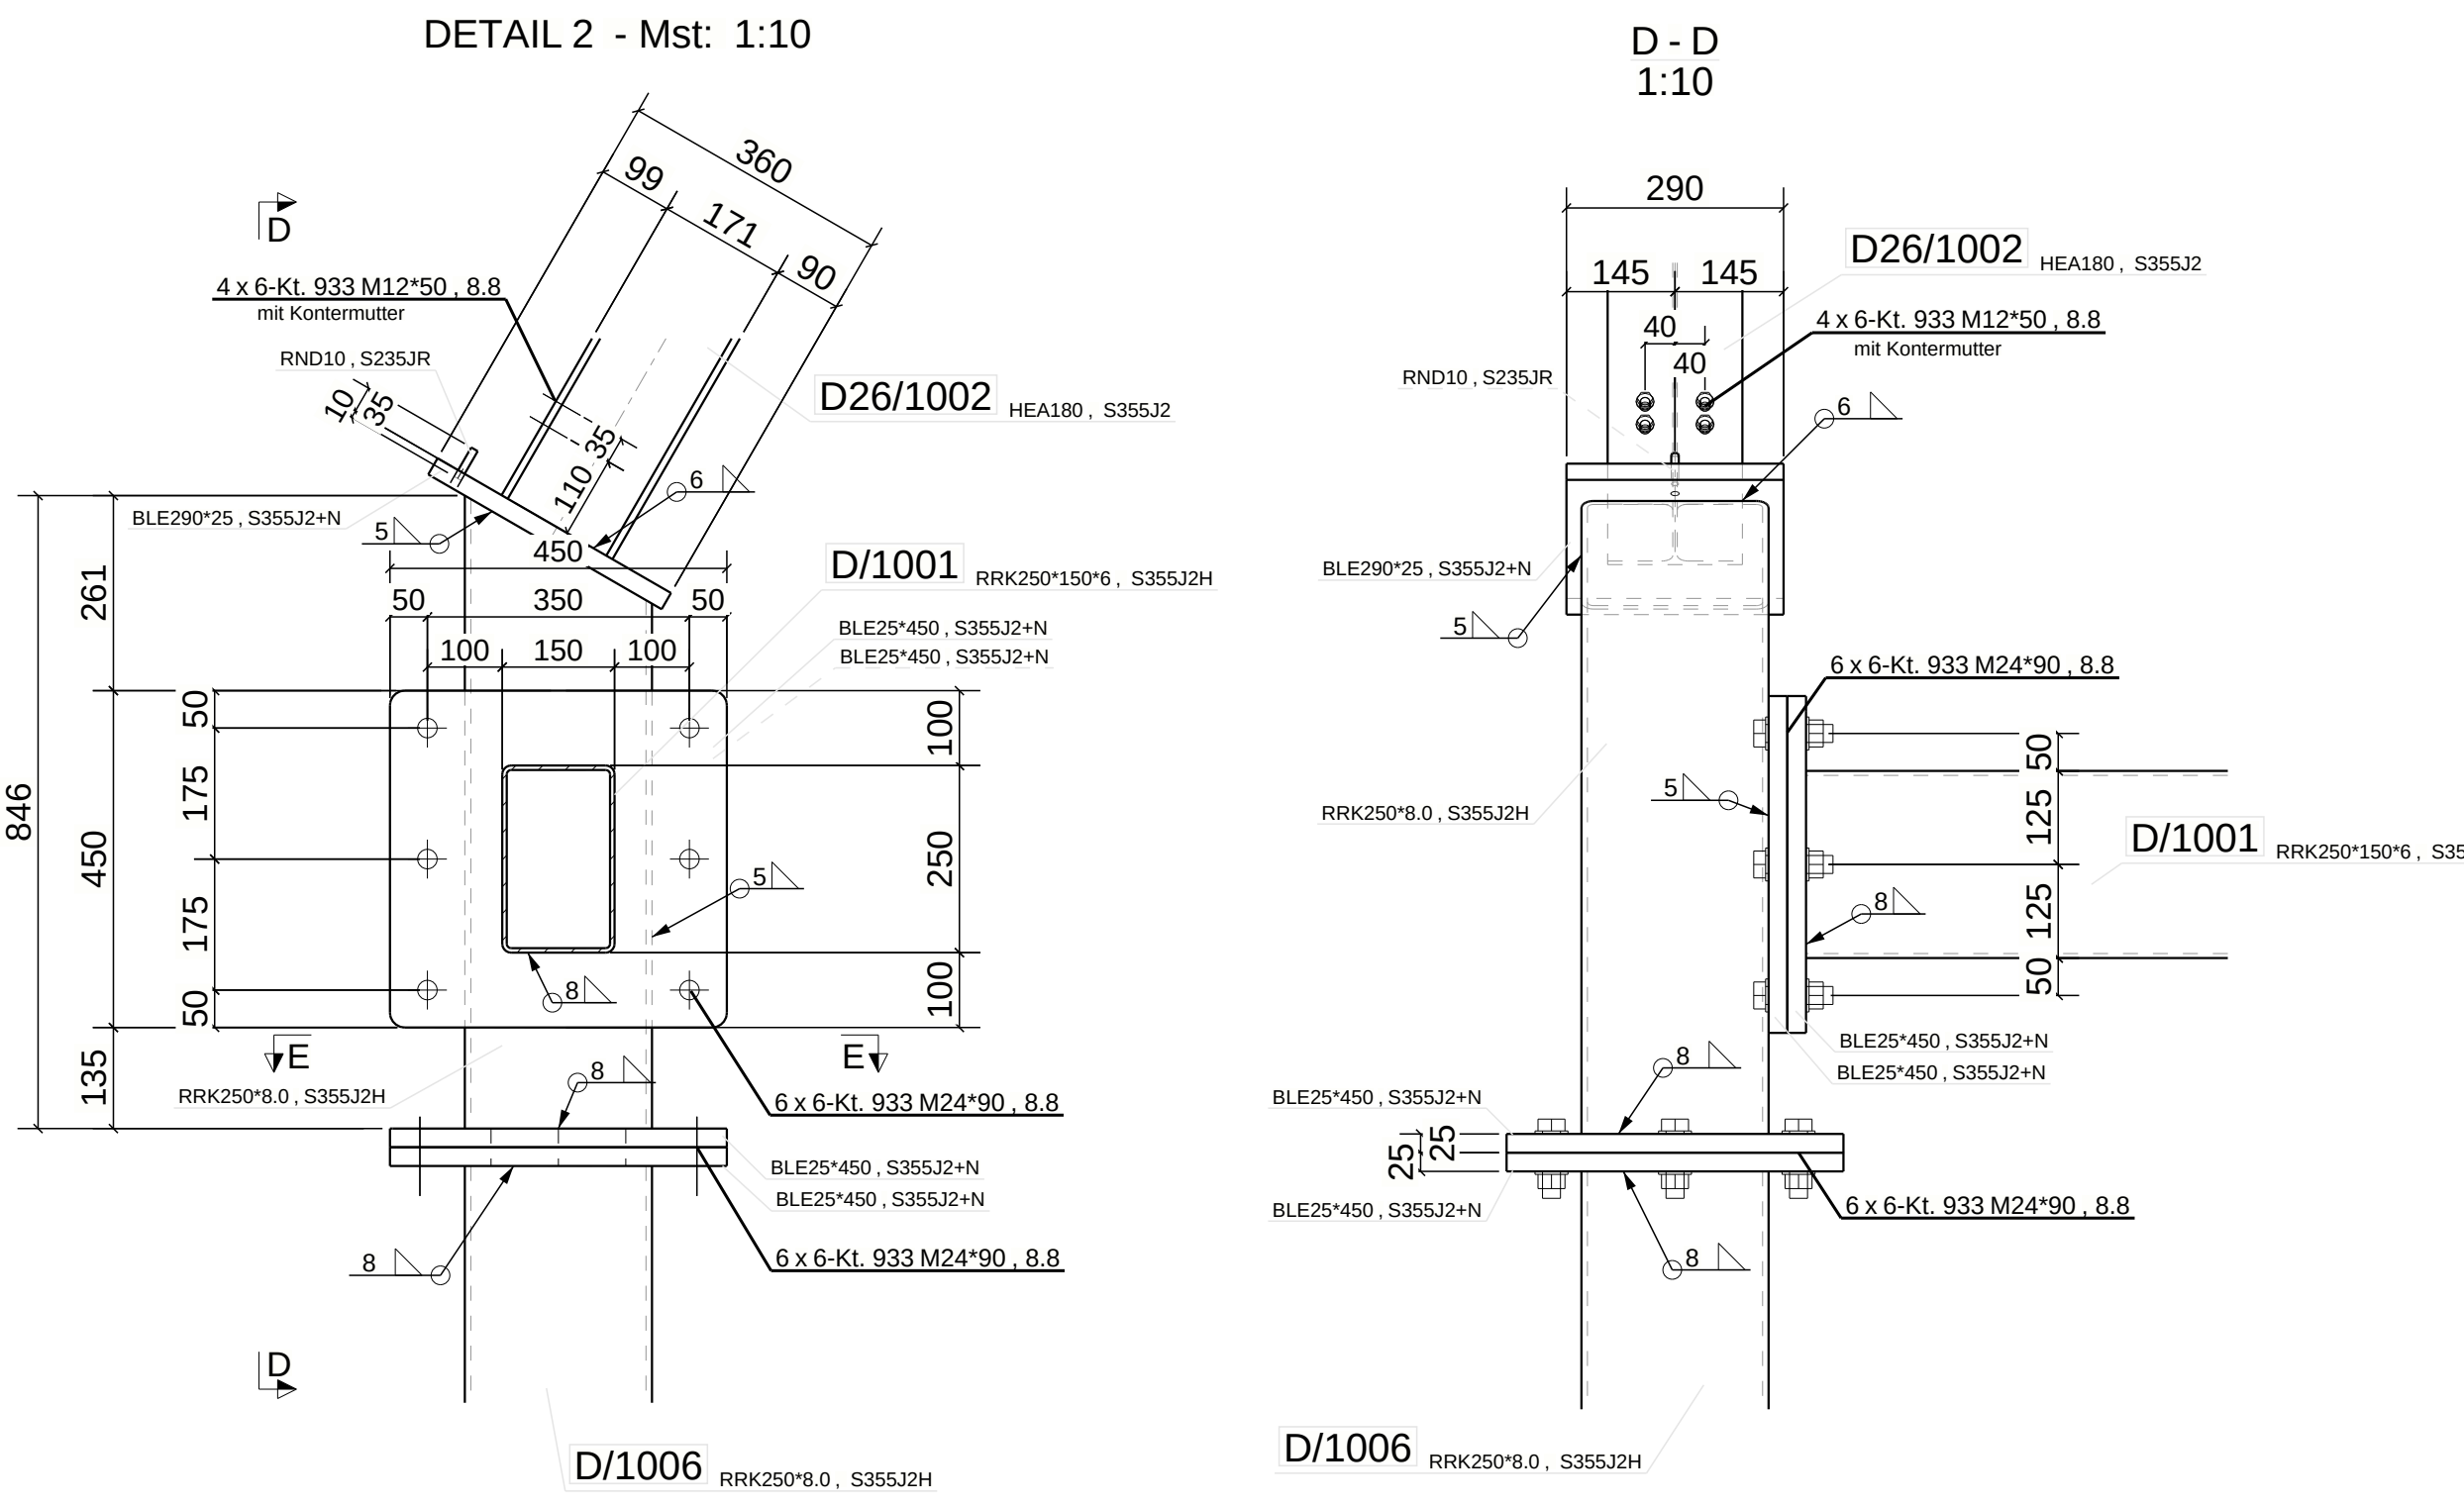


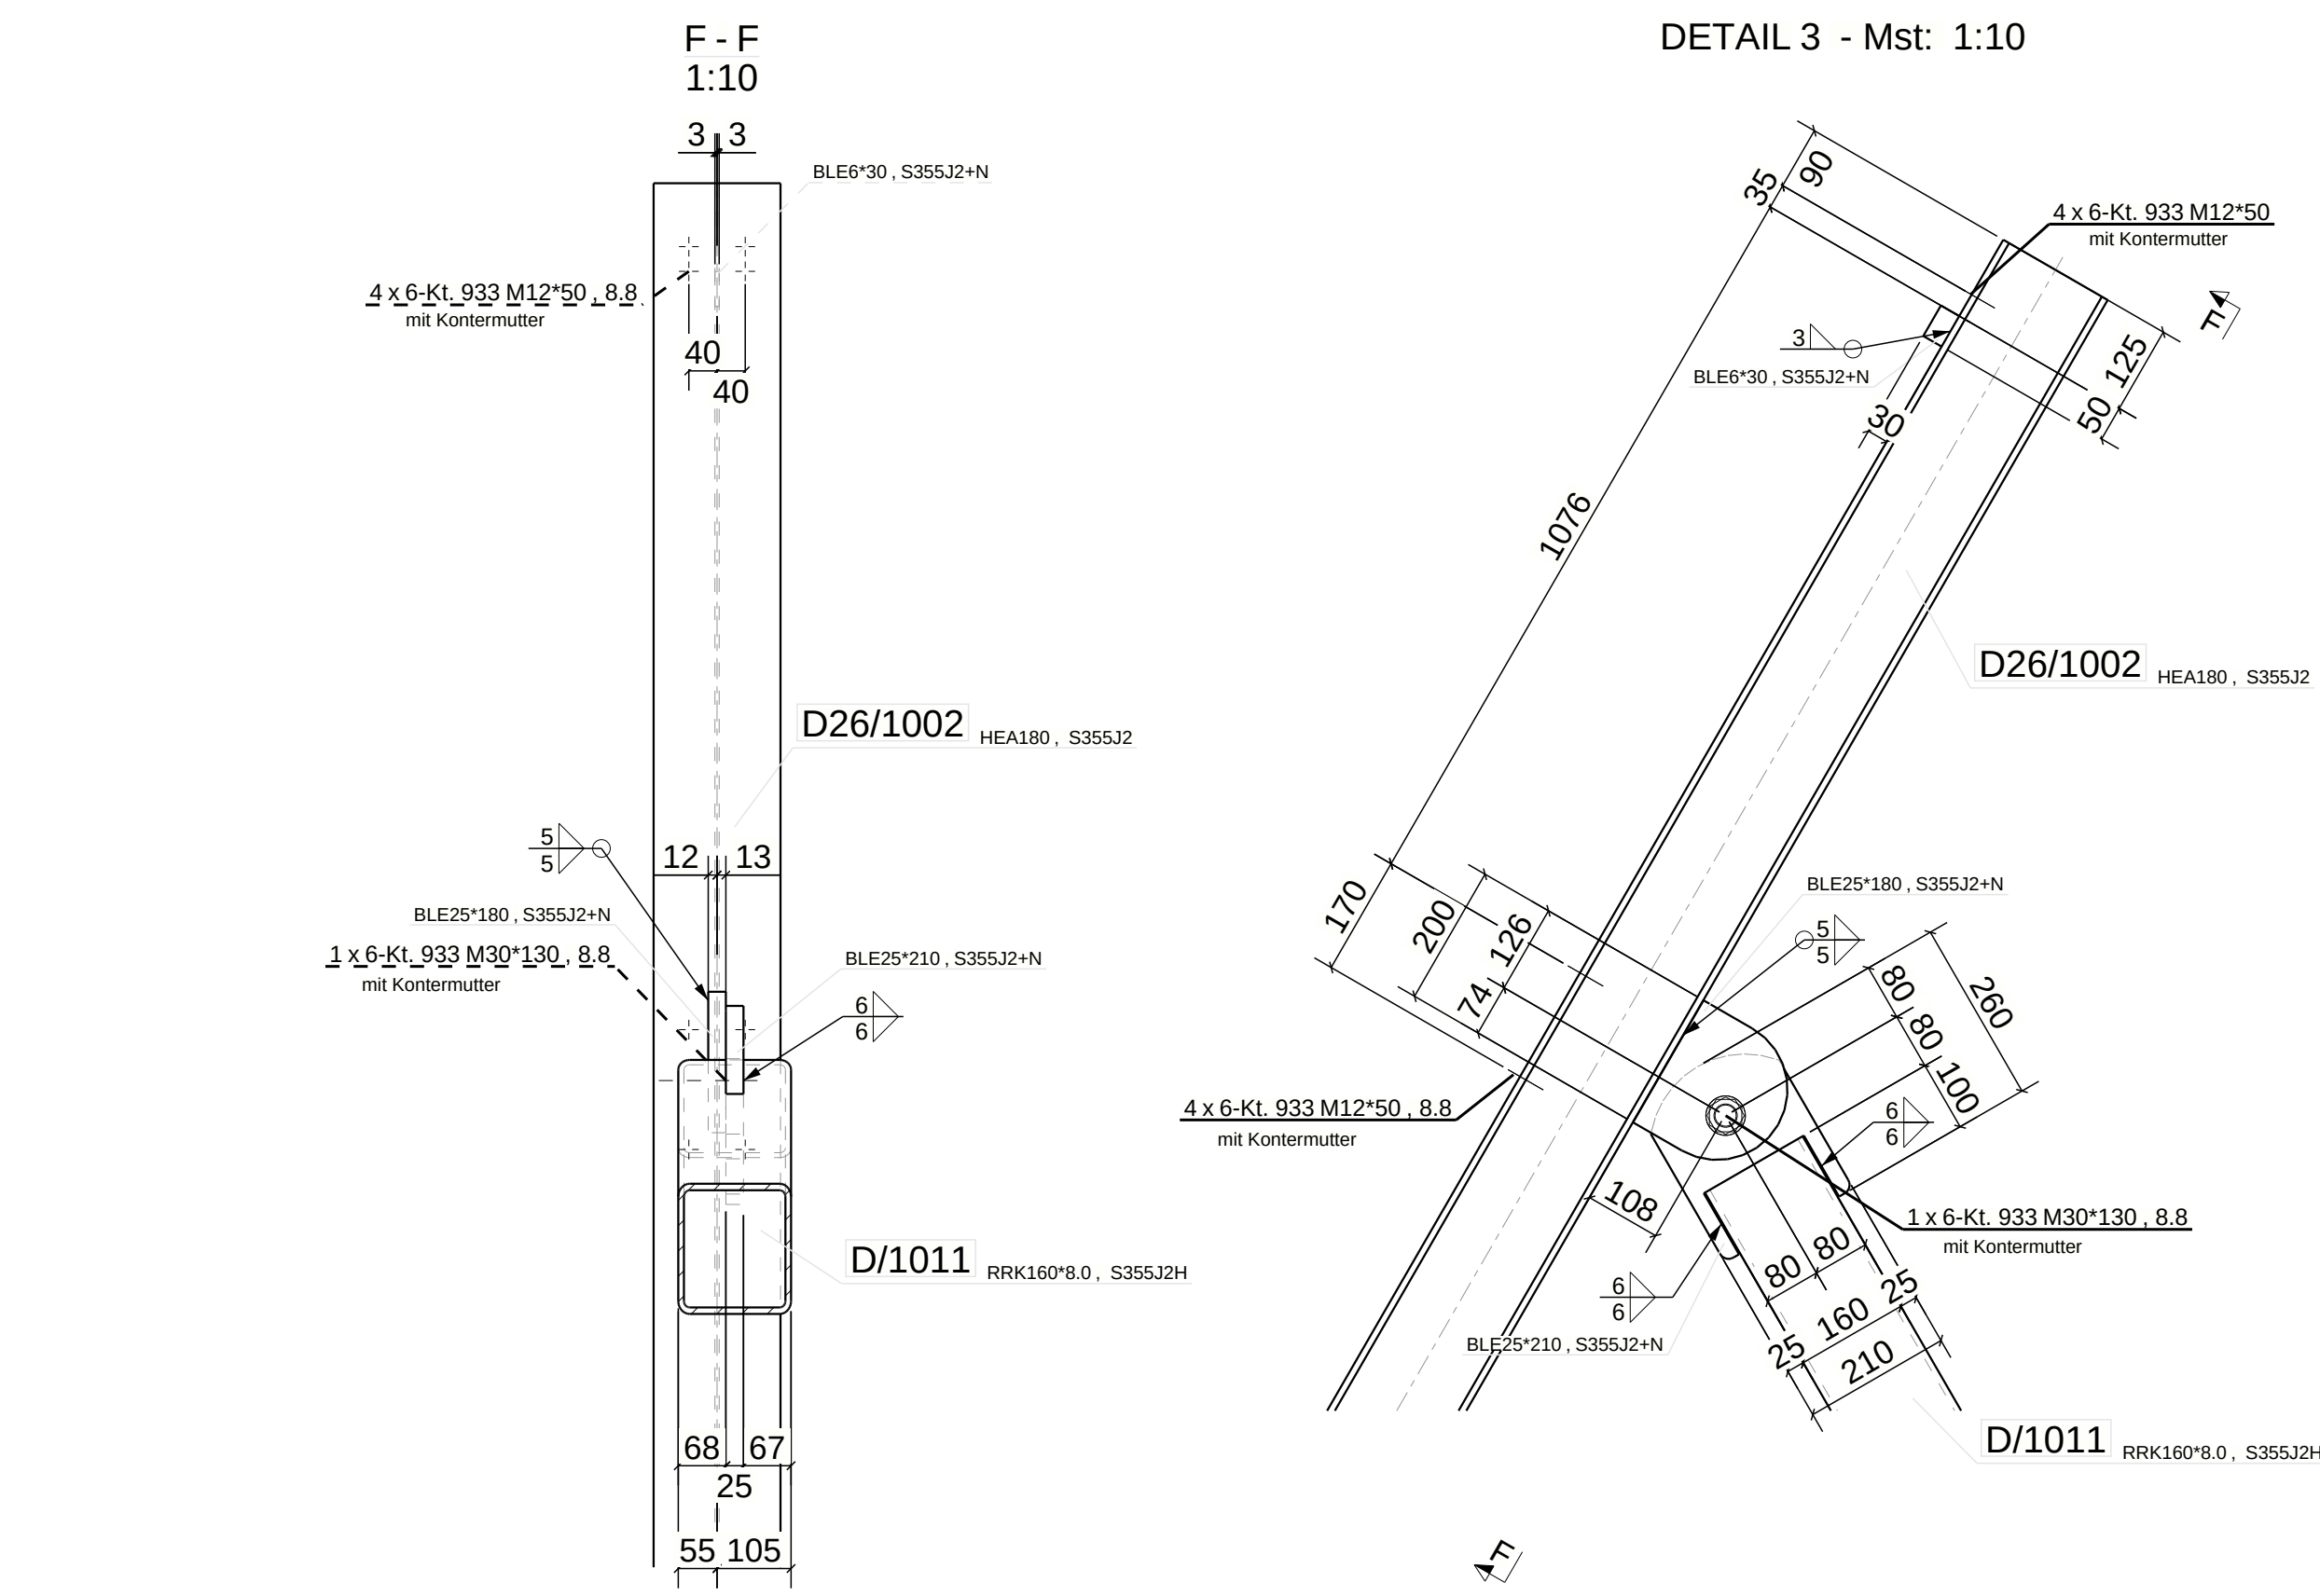

Gesamte Konstruktion ist Roh

Industriestrasse 9 - CH-6210 Sursee - T +41 41 925 12 51 - info@mauchle Stahlbau.ch			
Auftrag: 24027			
Zeichner: P.Koch			
Interne Kontrolle			
ABTEILUNG: UNTERSCHRIFT			
PL: J. Mäder			
MAßSTAB: 1:10 1:20 1:55			
ANSICHT: 1:20 1:55			
ZEICHNUNGNUMMER: 24027 S O M 006 B			
BAUHER: Axpo Solutions AG			
BAUSTELLE: NalpSolar			
BENENNUNG: Primärkonstruktion Typ D			
Typ 2026			
Ansicht, Schnitte & Details			
P.Koch			
NAME			