
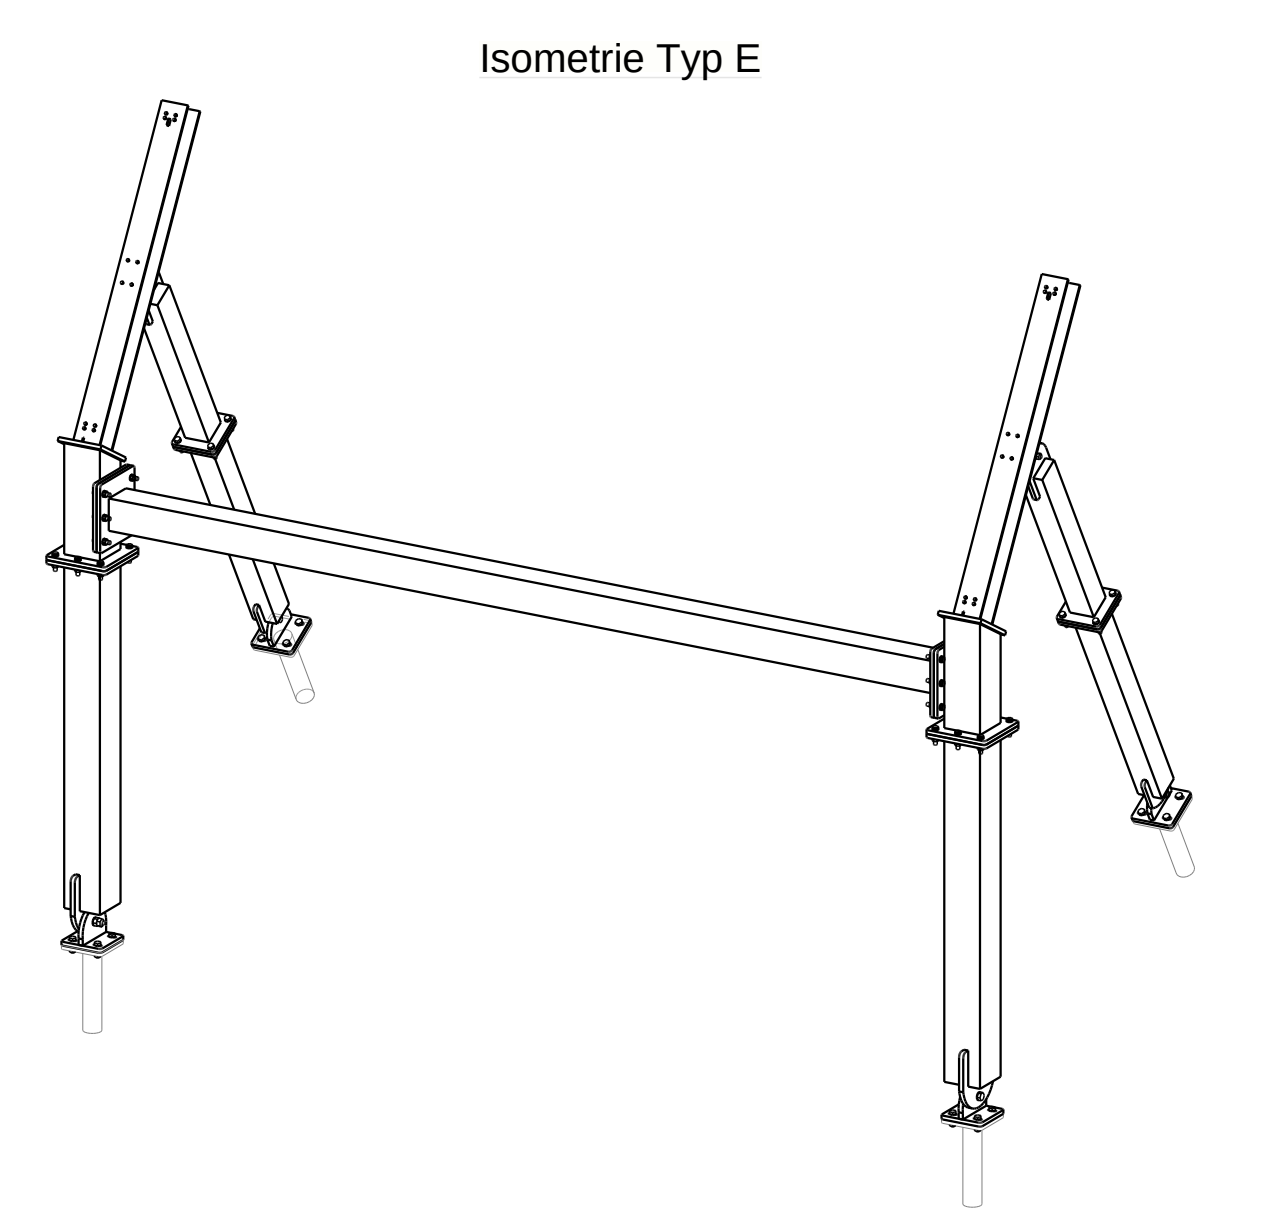
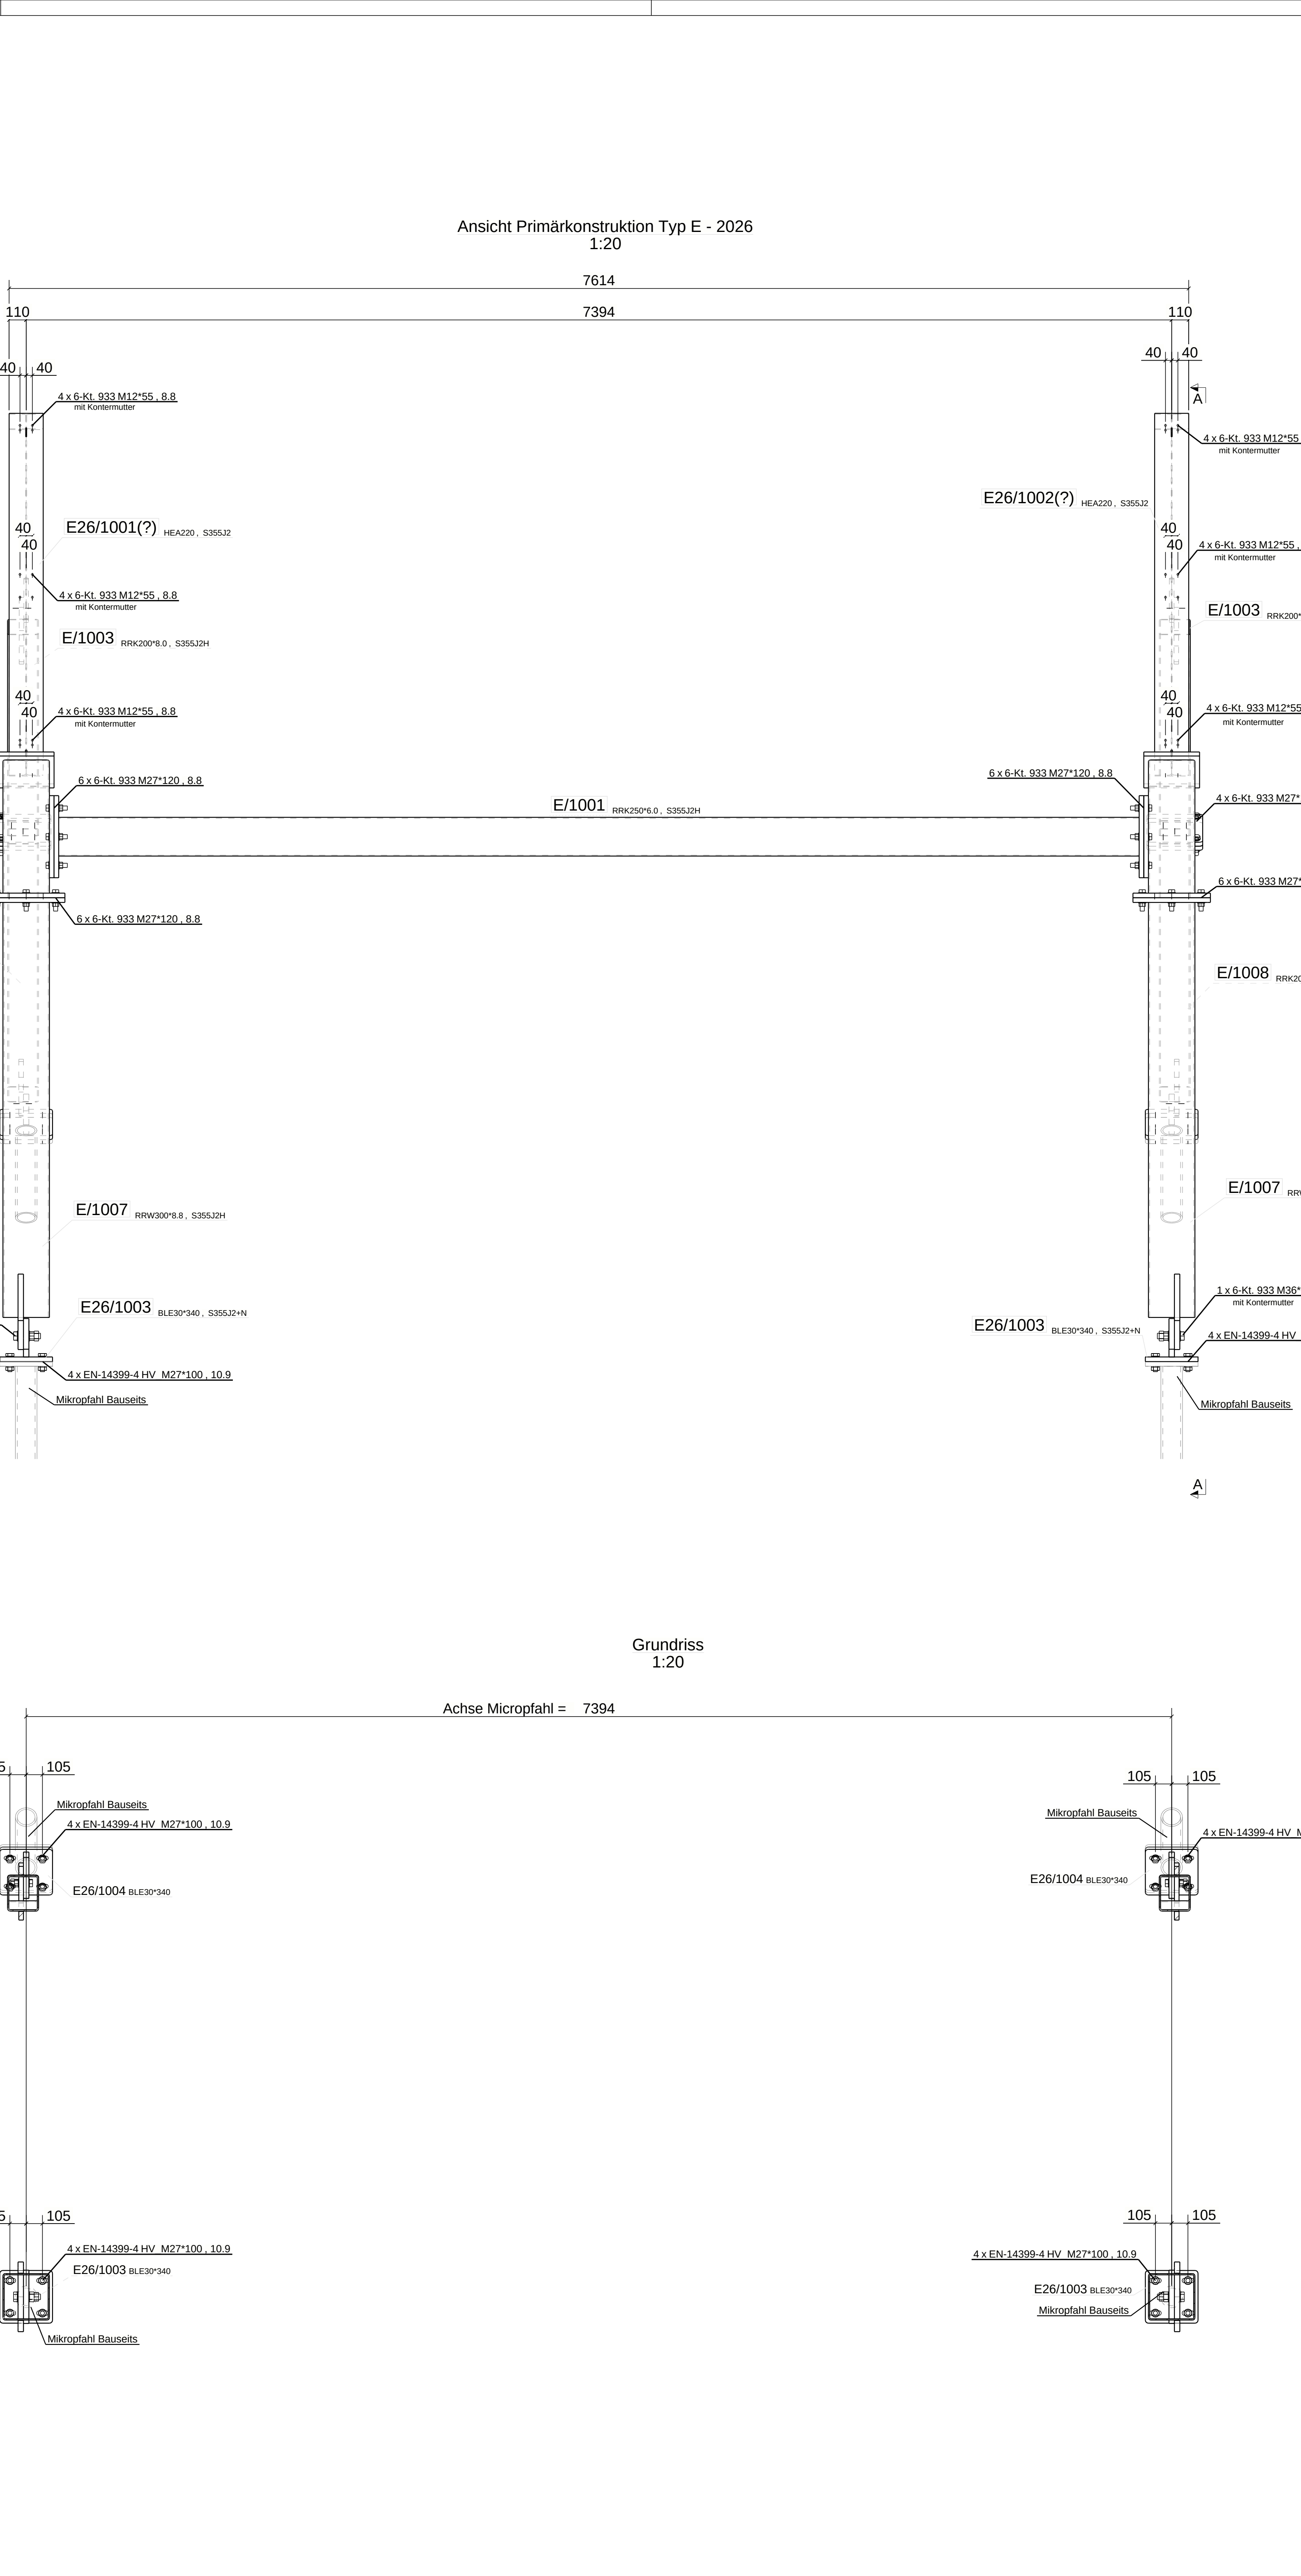
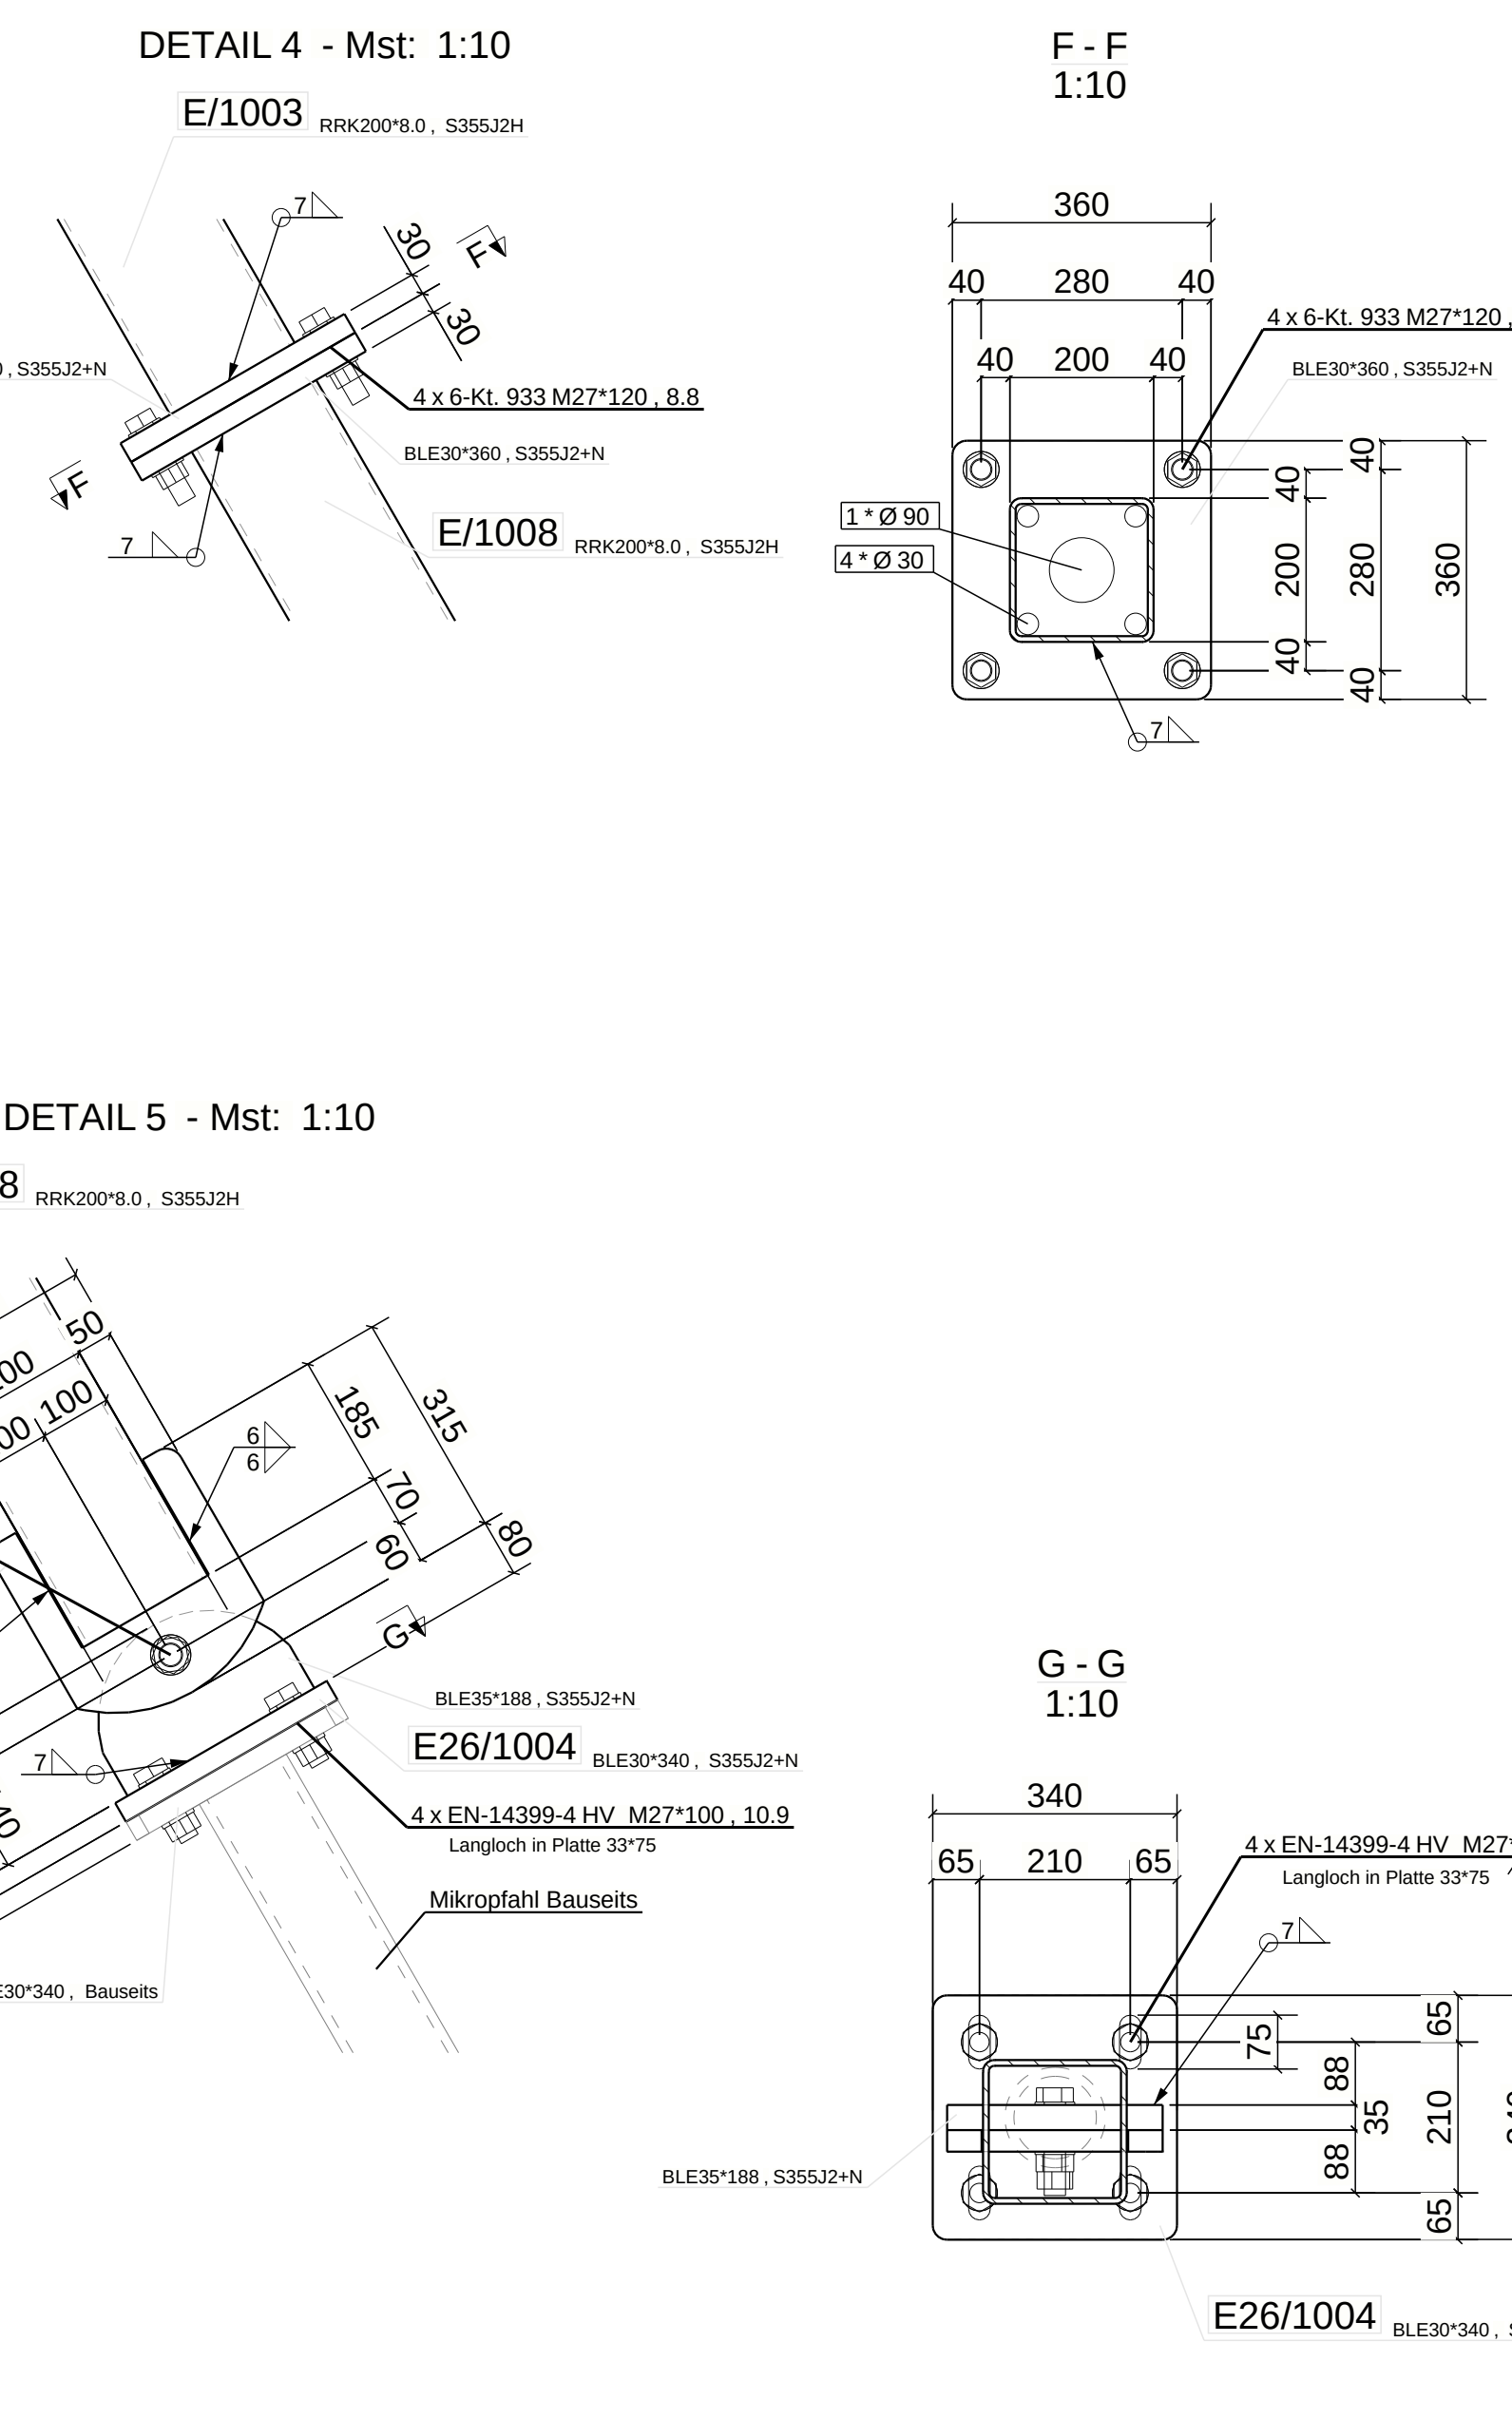
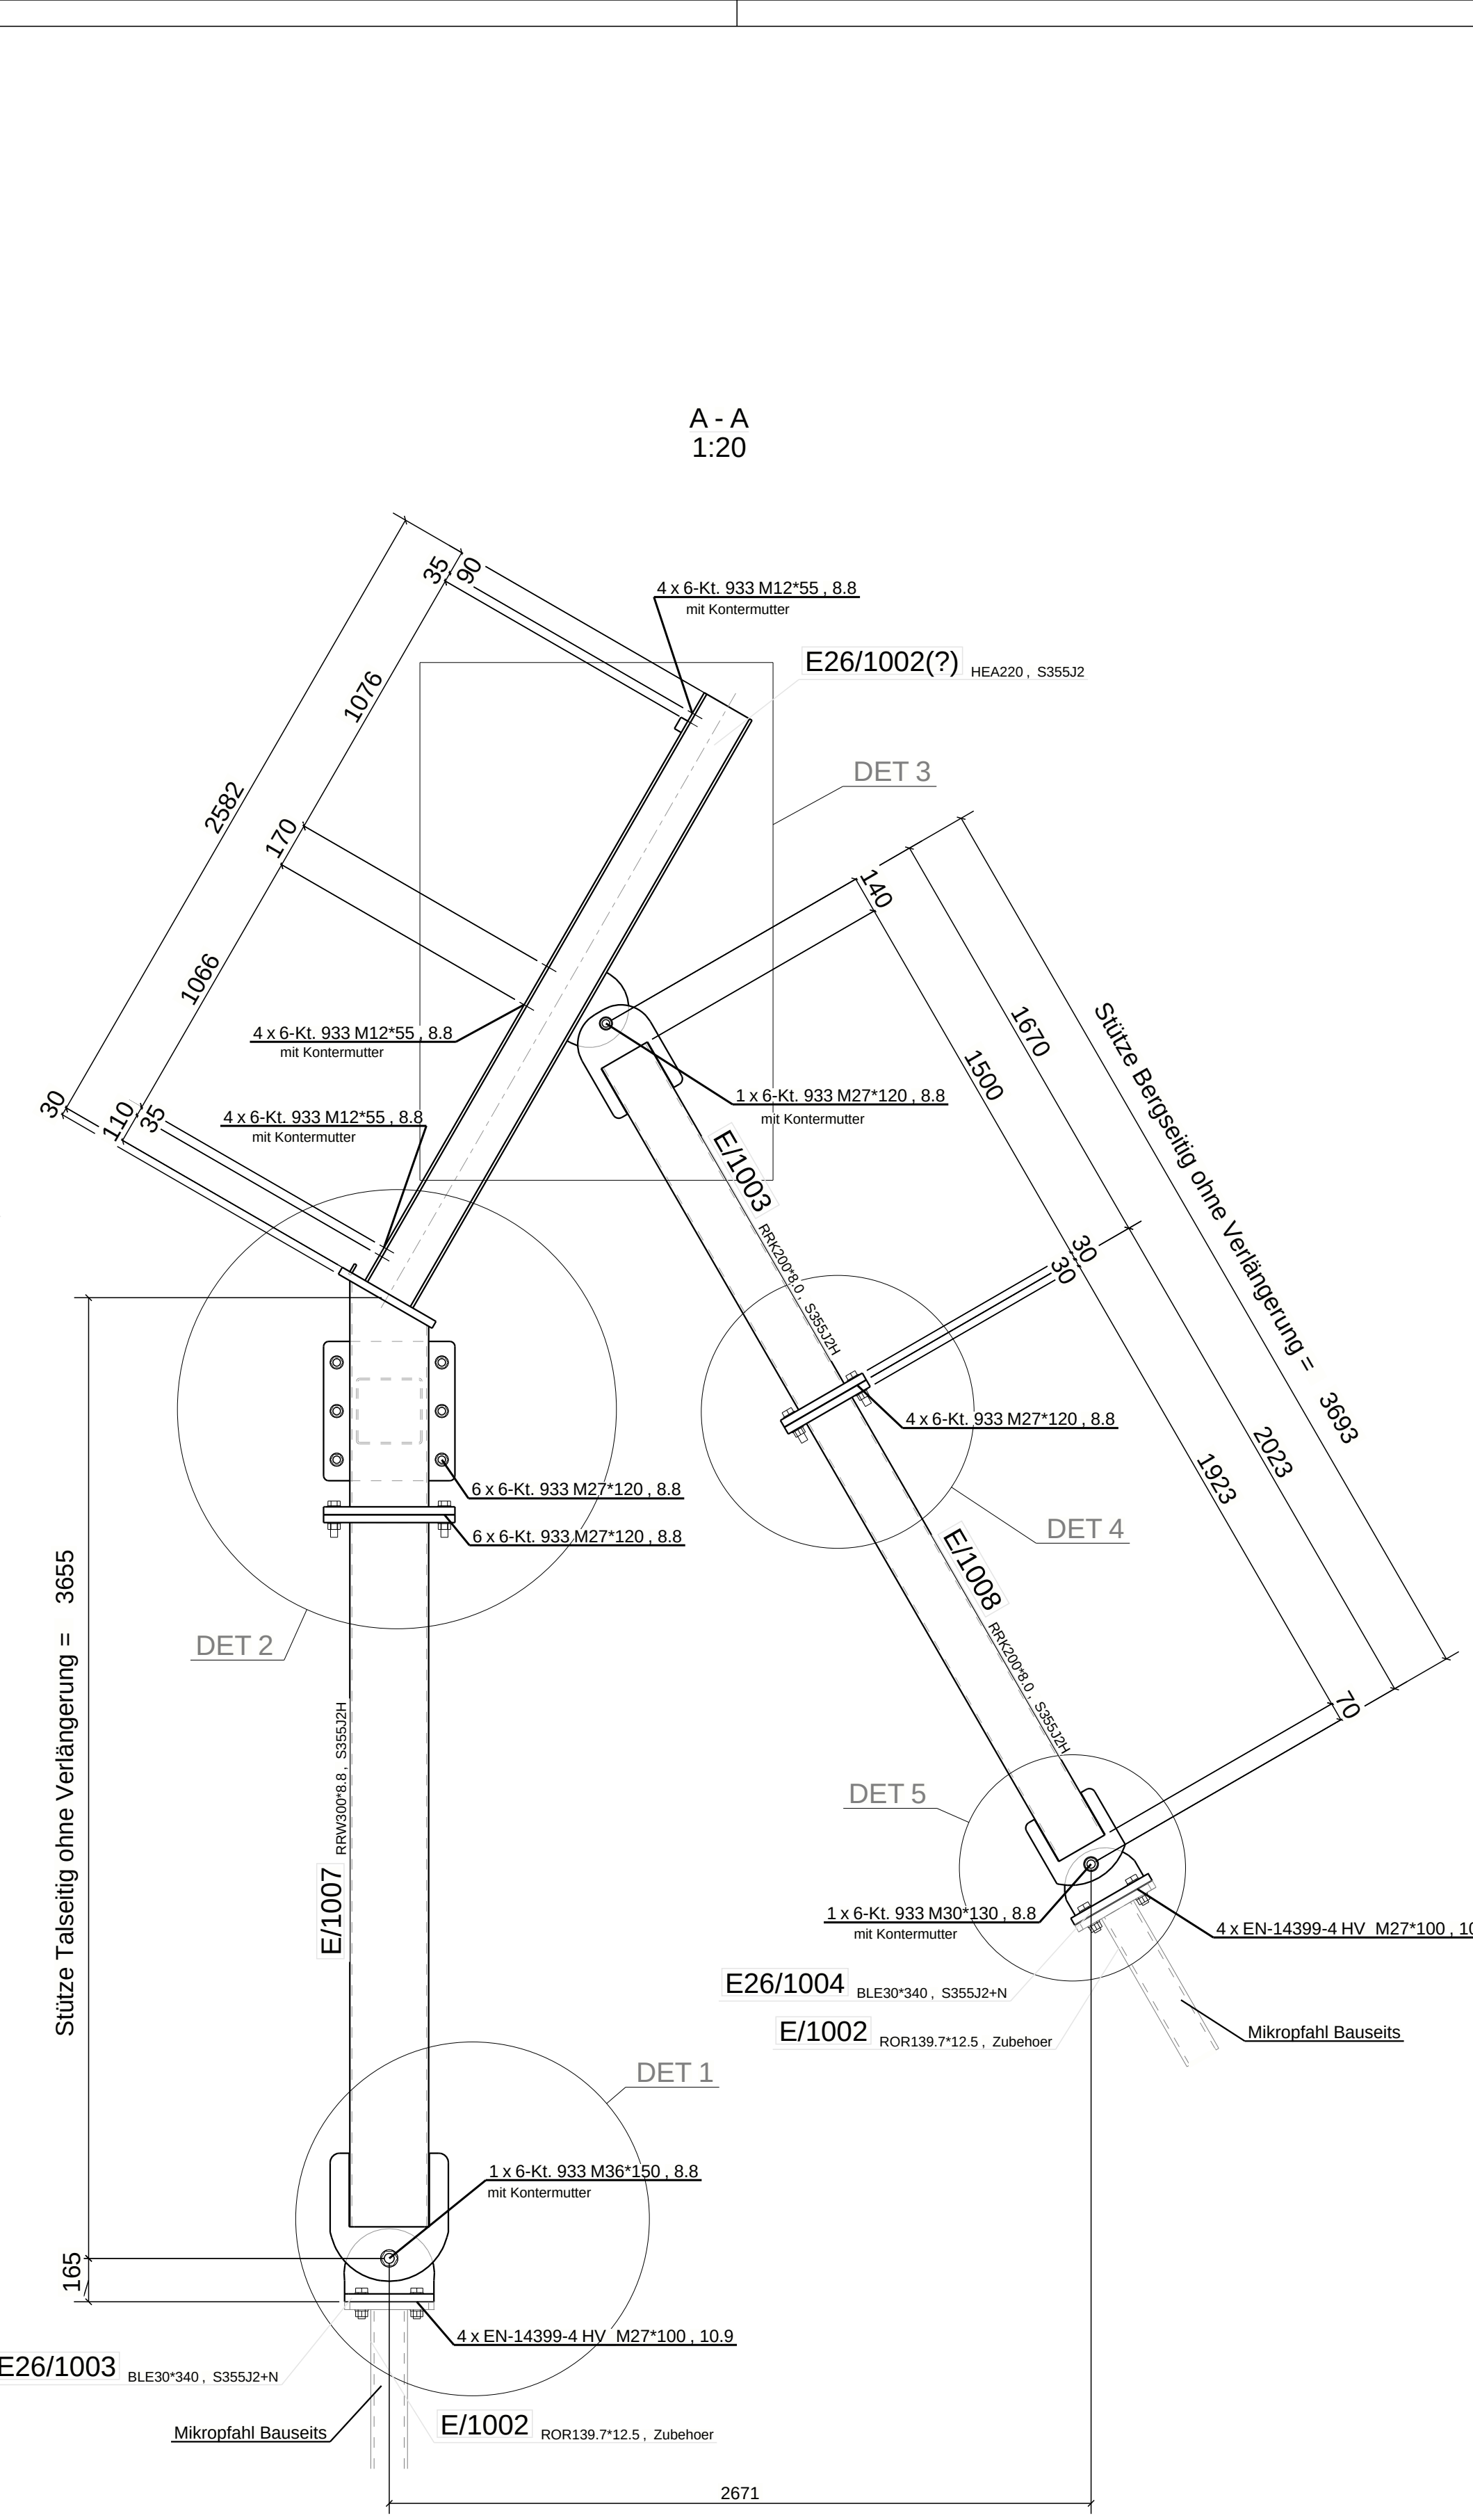
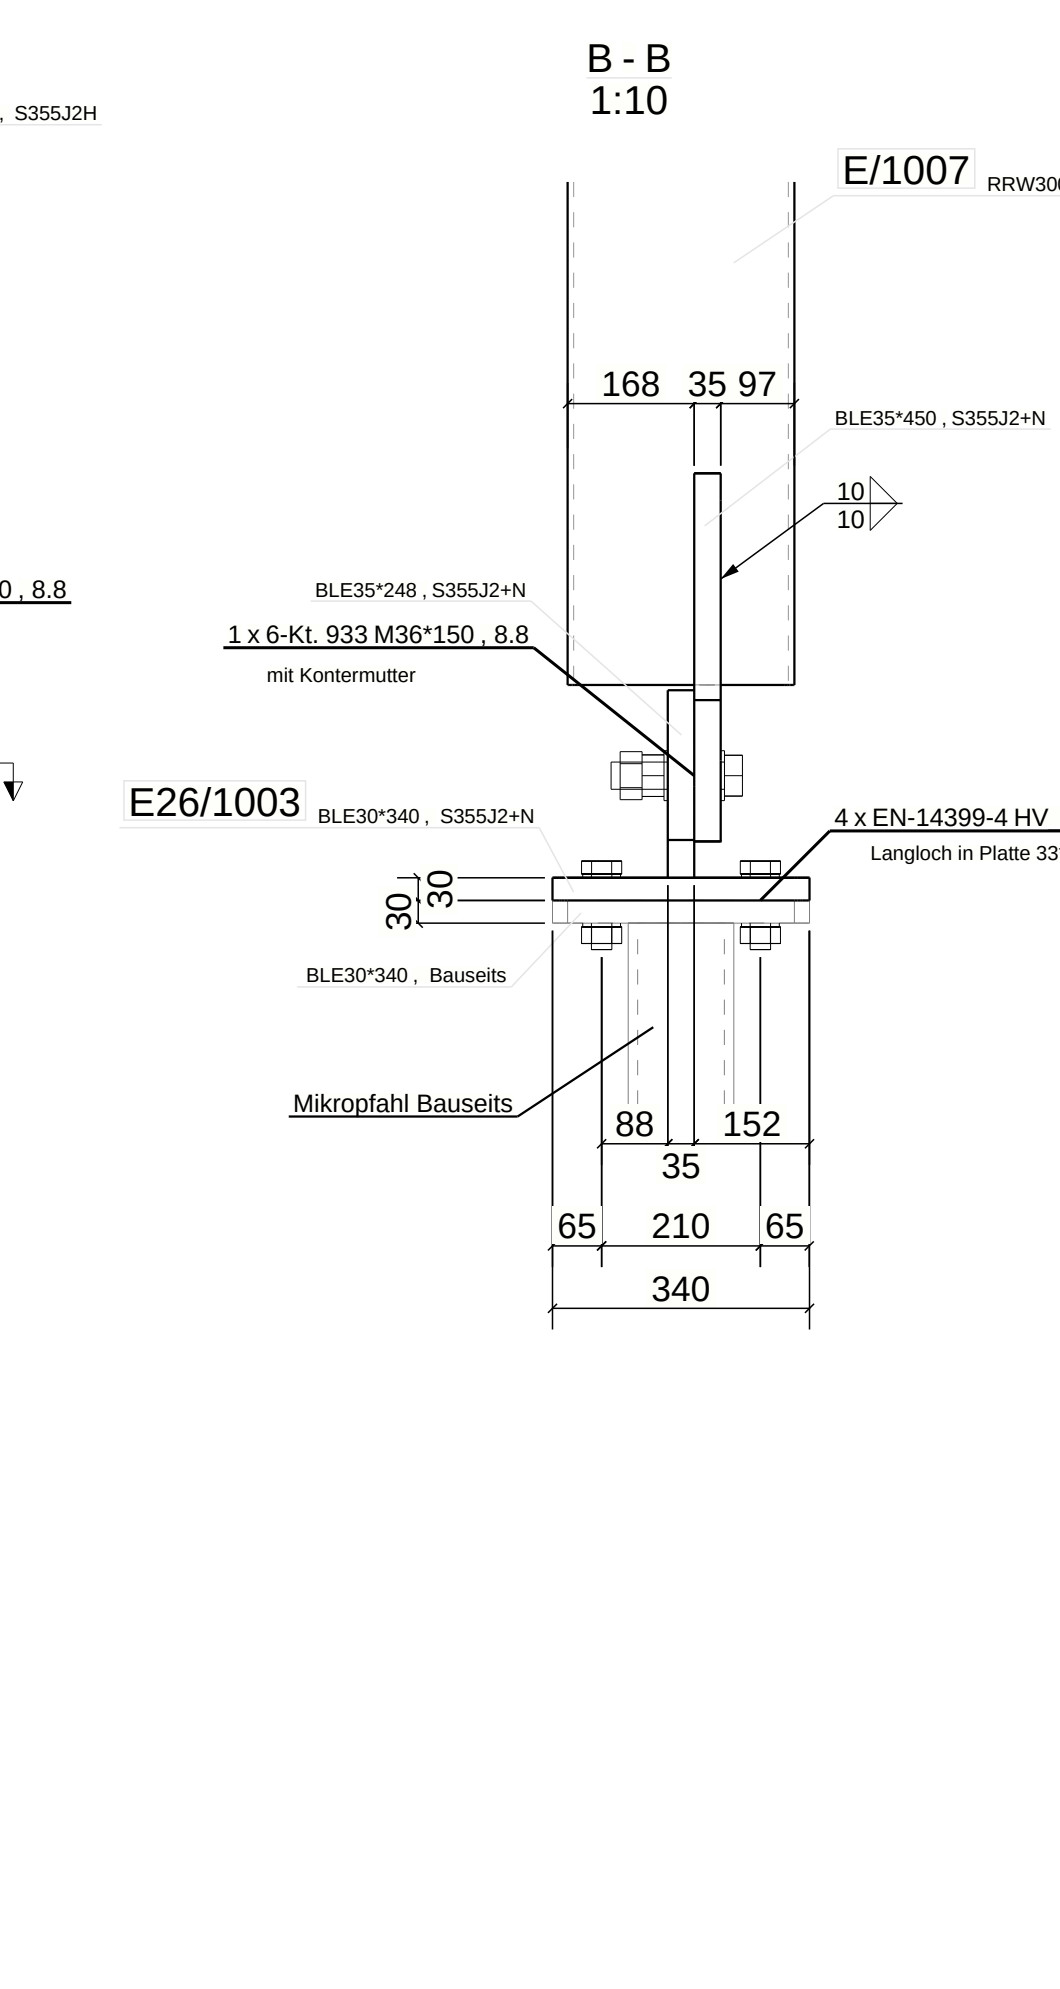
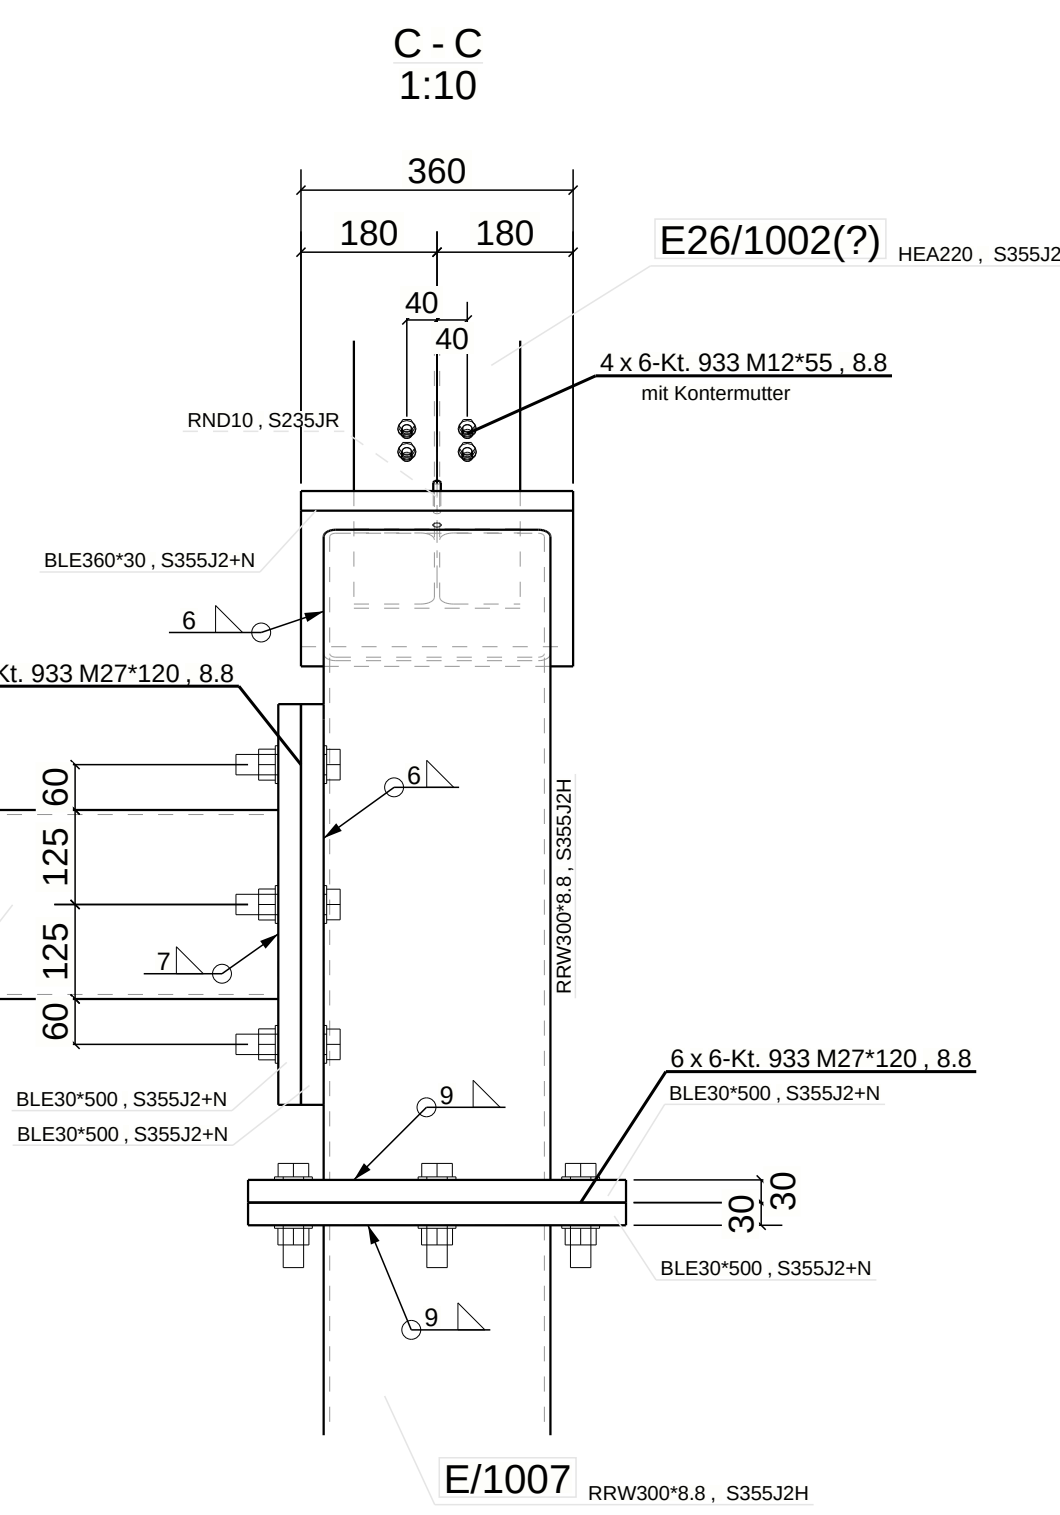
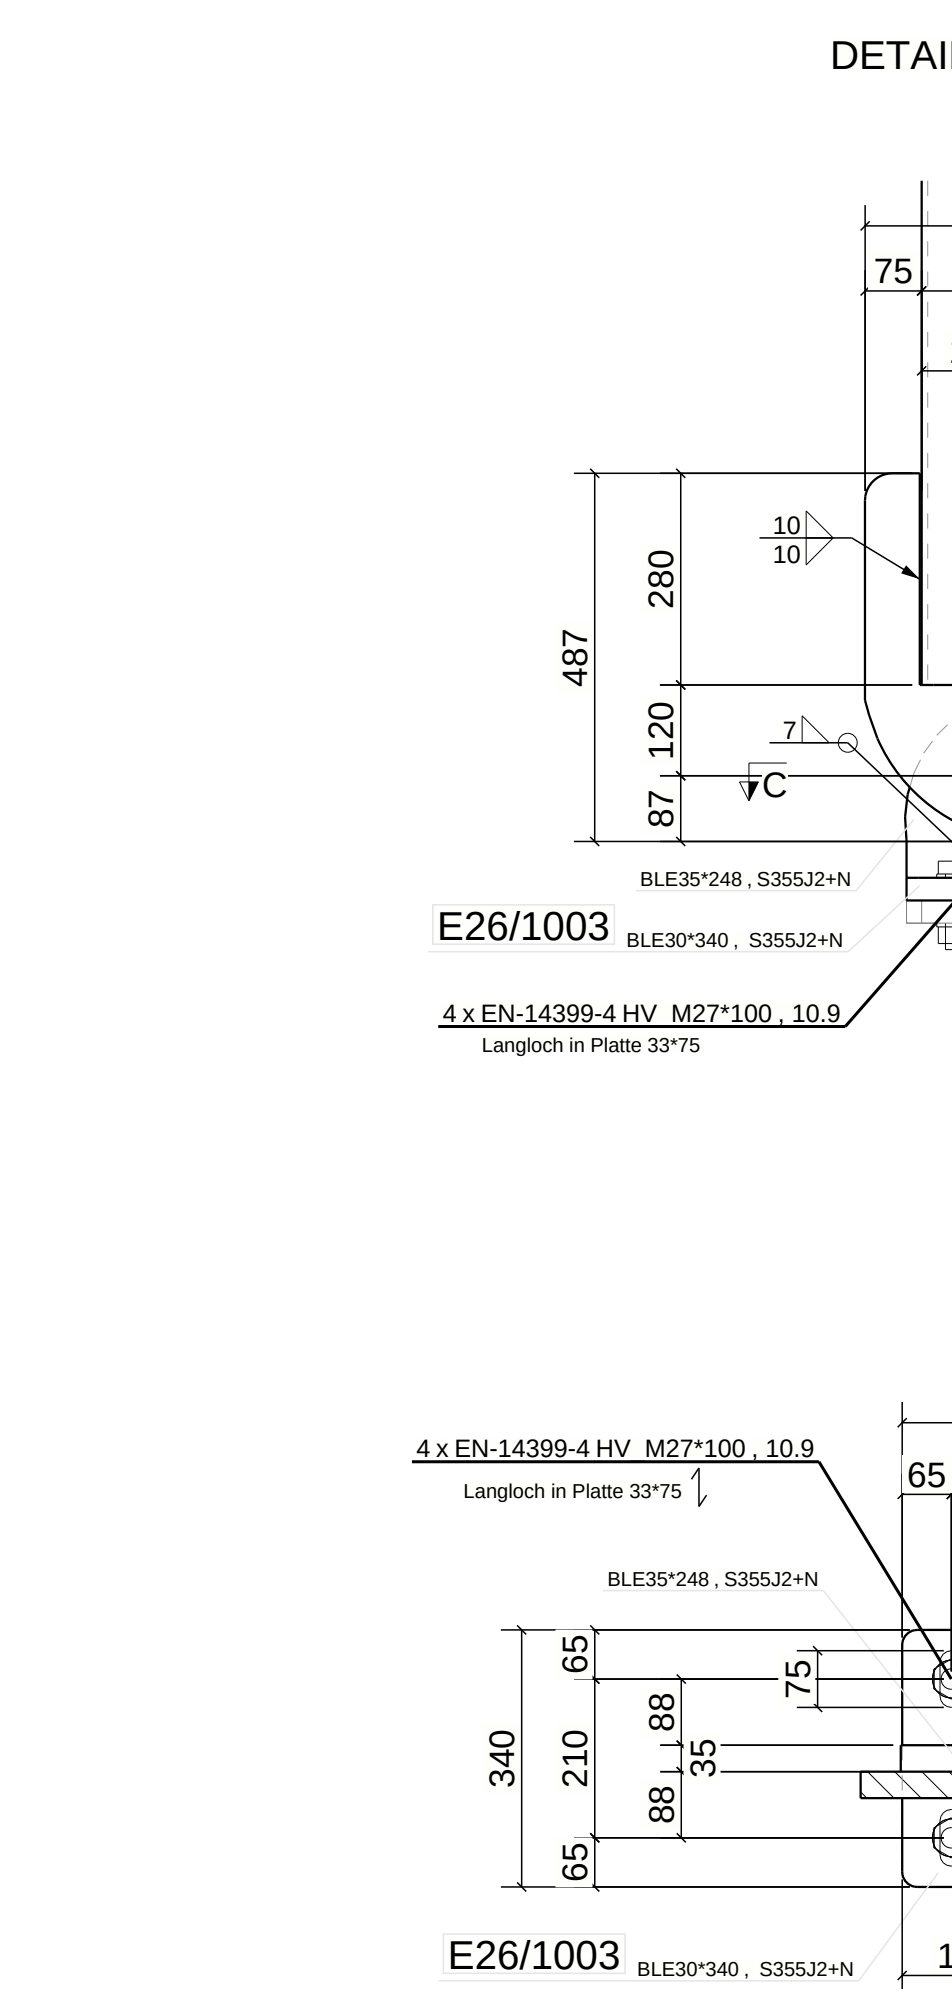
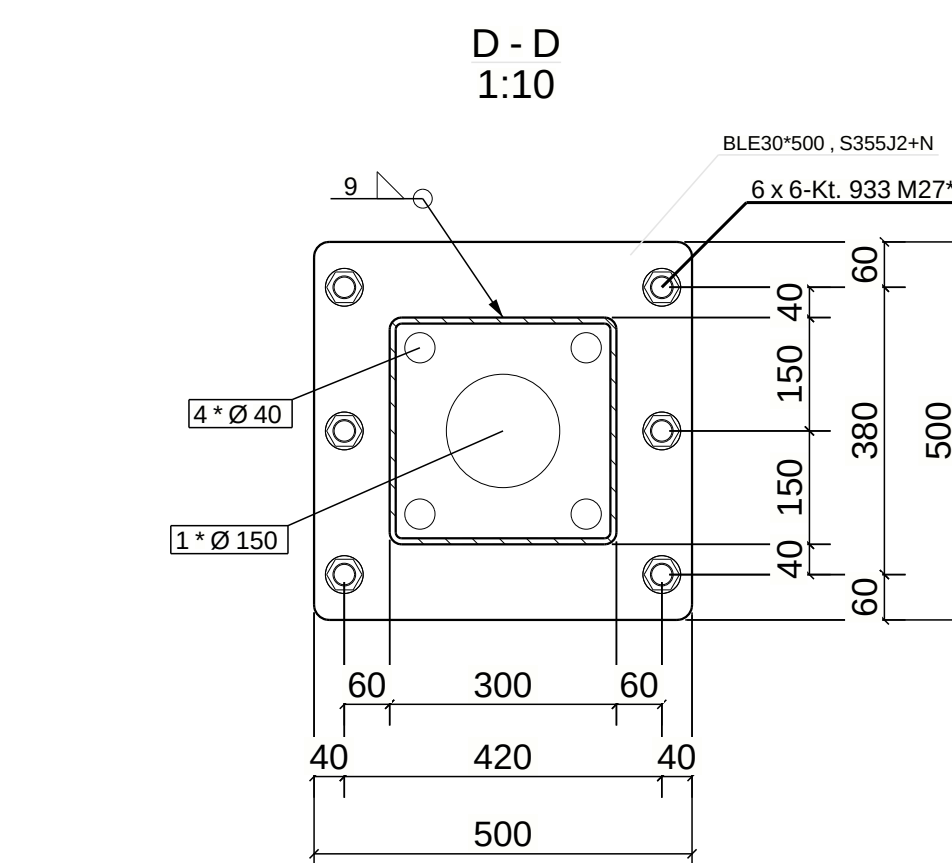
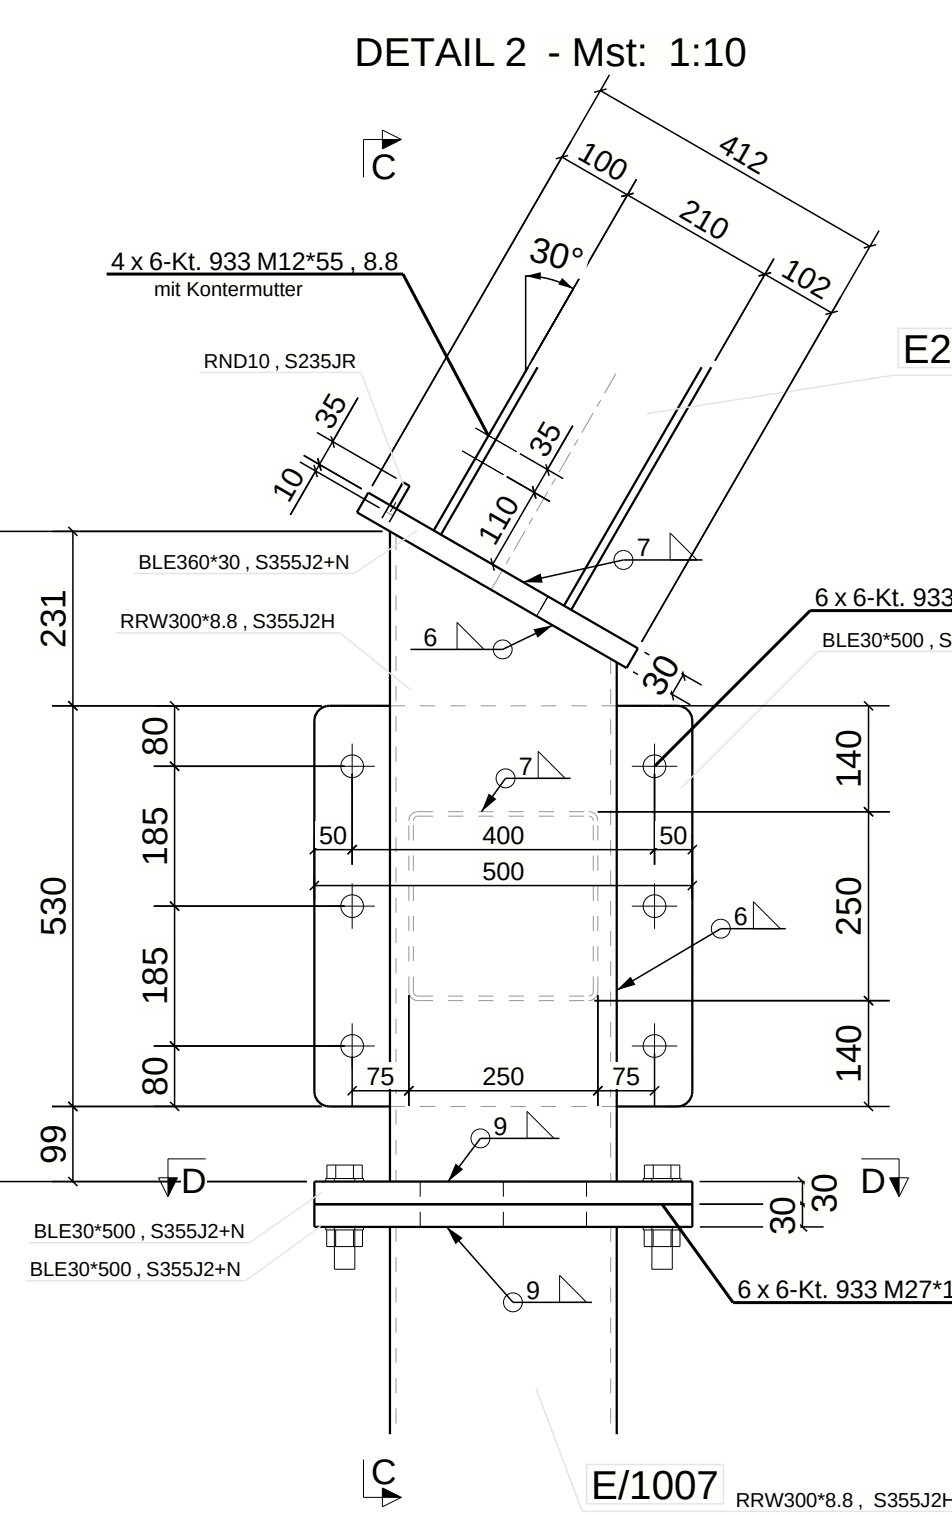
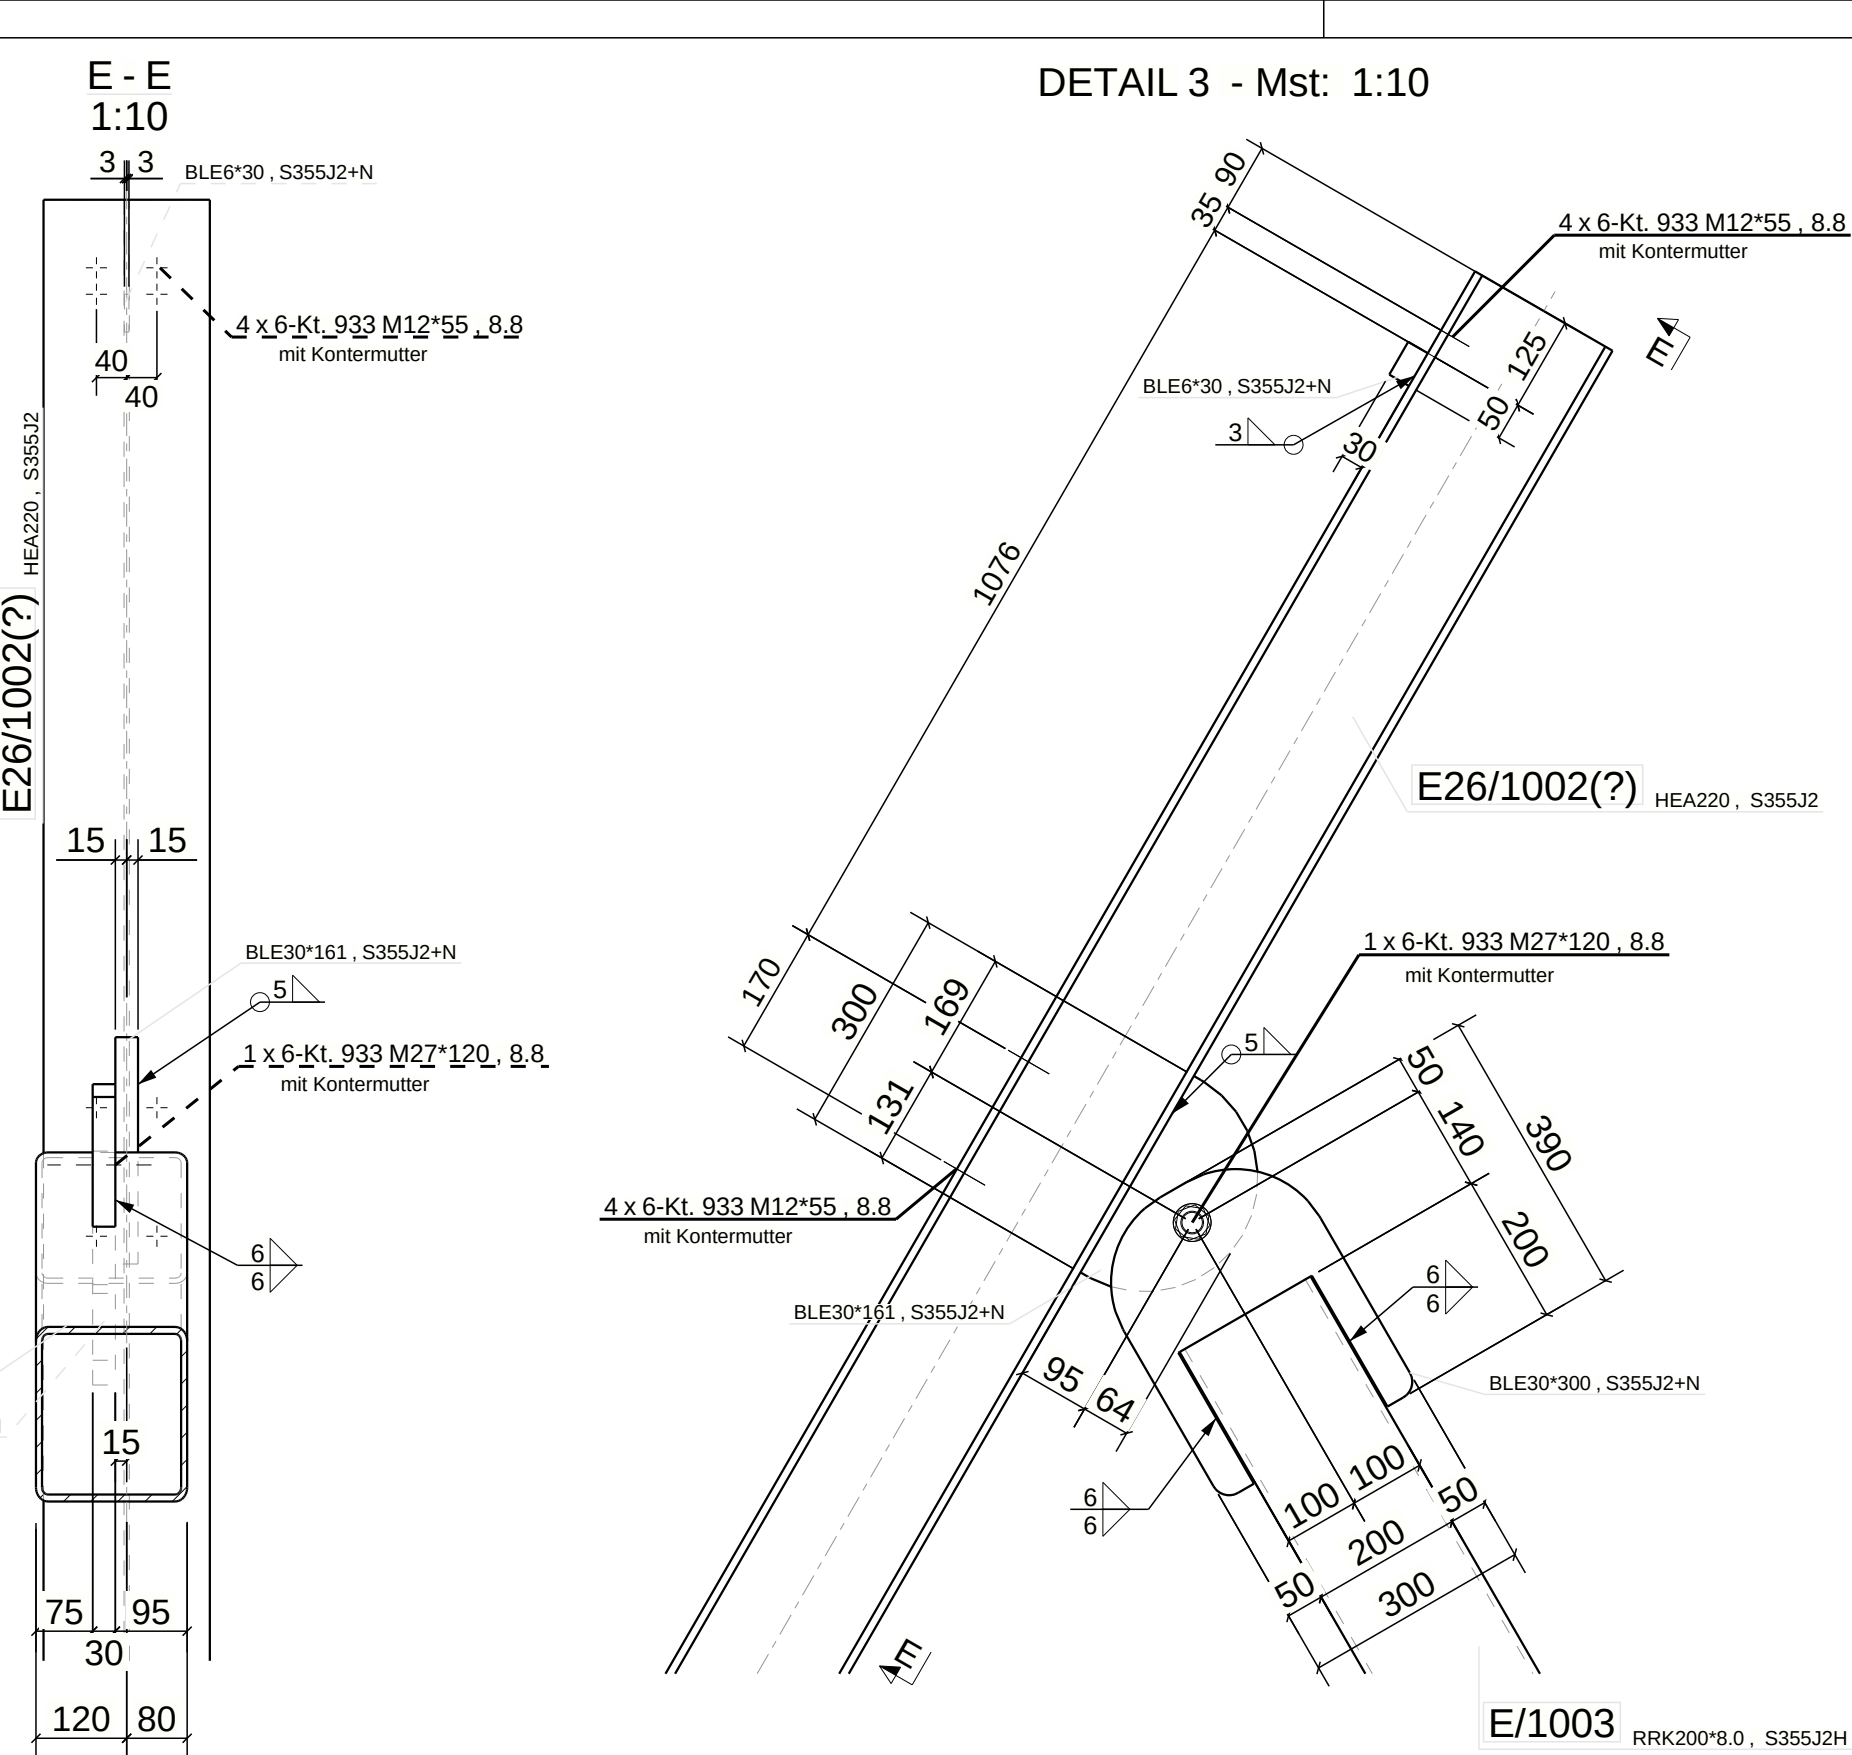


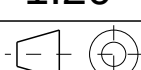

Gesamte Konstruktion ist Roh									
B		11.02.2026		Befestigung Modultisch geändert				P.Koch	
A		09.02.2026		Ergänzungen für Befestigung Modultisch				P.Koch	
INDEX		Seite 1		ANZEICHEN BEZEICHNUNG				NAME	
MAUCHLE Stahlbau									
Industriestrasse 9 - CH-6210 Sursee - T +41 41 925 12 51 - info@mauchle Stahlbau.ch									
Auftragsg.		24027		BAUHEHR					
Zeichner		P.Koch		Xpo Solutions AG					
				BAUSTELLE					
		Interne Kontrolle		NalpSolar					
ABTEILUNG		UNTERSCHRIFT		BEZEICHNUNG					
				Primärkonstruktion Typ E					
				Typ 2026					
PL		J. Mäder		Ansicht, Schnitte & Details					
MASSSTAB		1:10 1:20 1:55		ZEICHNUNGSNUMMER					
ANSICHT				24027 S 0 M 007 B					
				(PROJEKT) (AUTUMN) (LIEF) (ZEICHNUNG) (FERTIGSTELLUNG) (NF) (REVISION)					