DETAIL 3, Schnitt F - F : Auflageträger (A1)
1:10

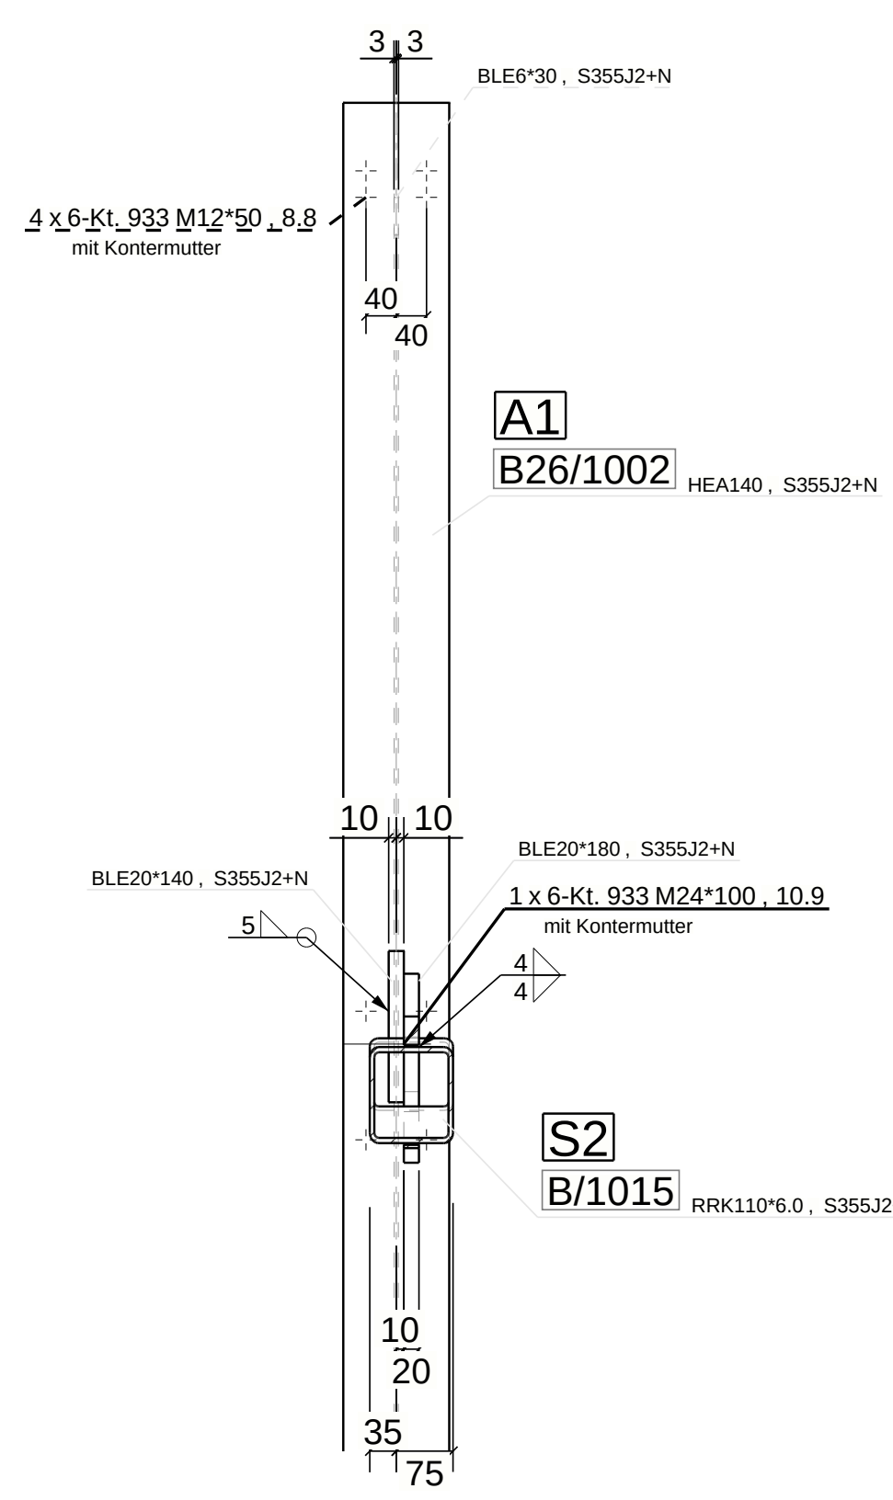

DETAIL 3 : Auflageträger (A1) - Mst: 1:10

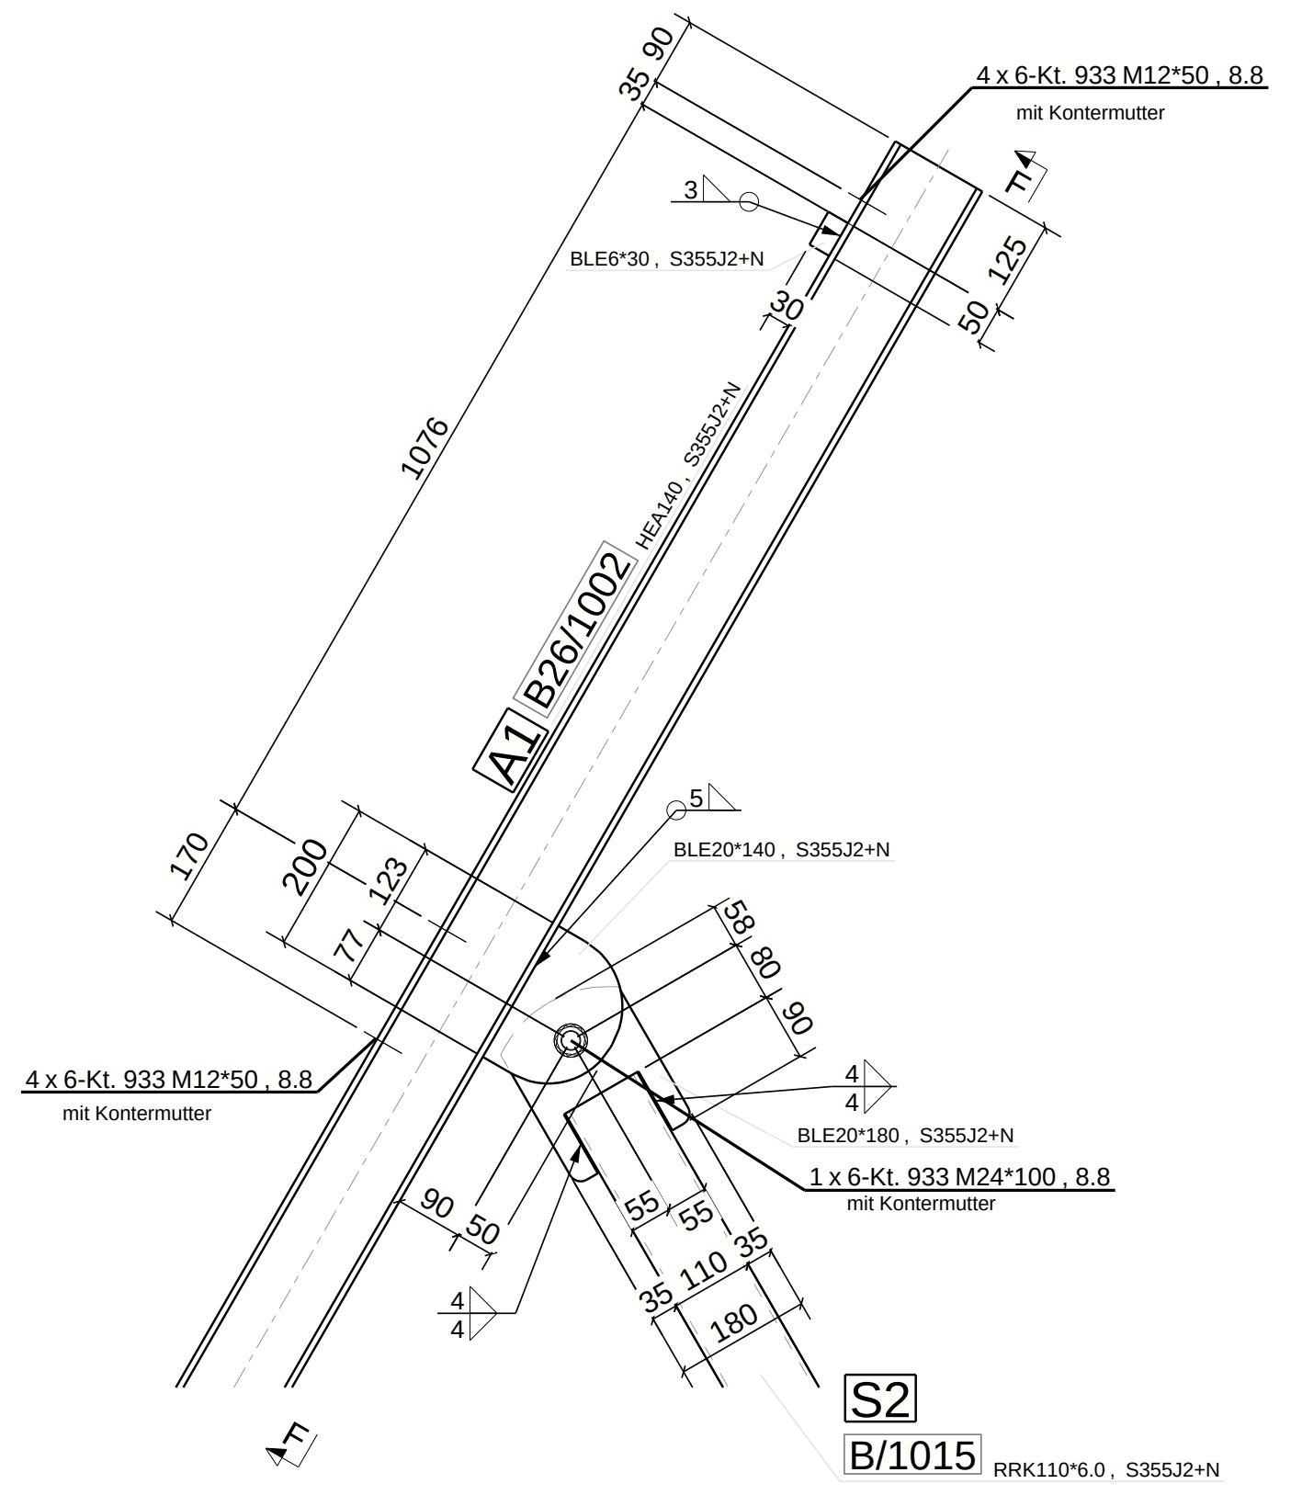

A - A
Schnitt: Primärkonstruktion Typ B - 2026
1:20

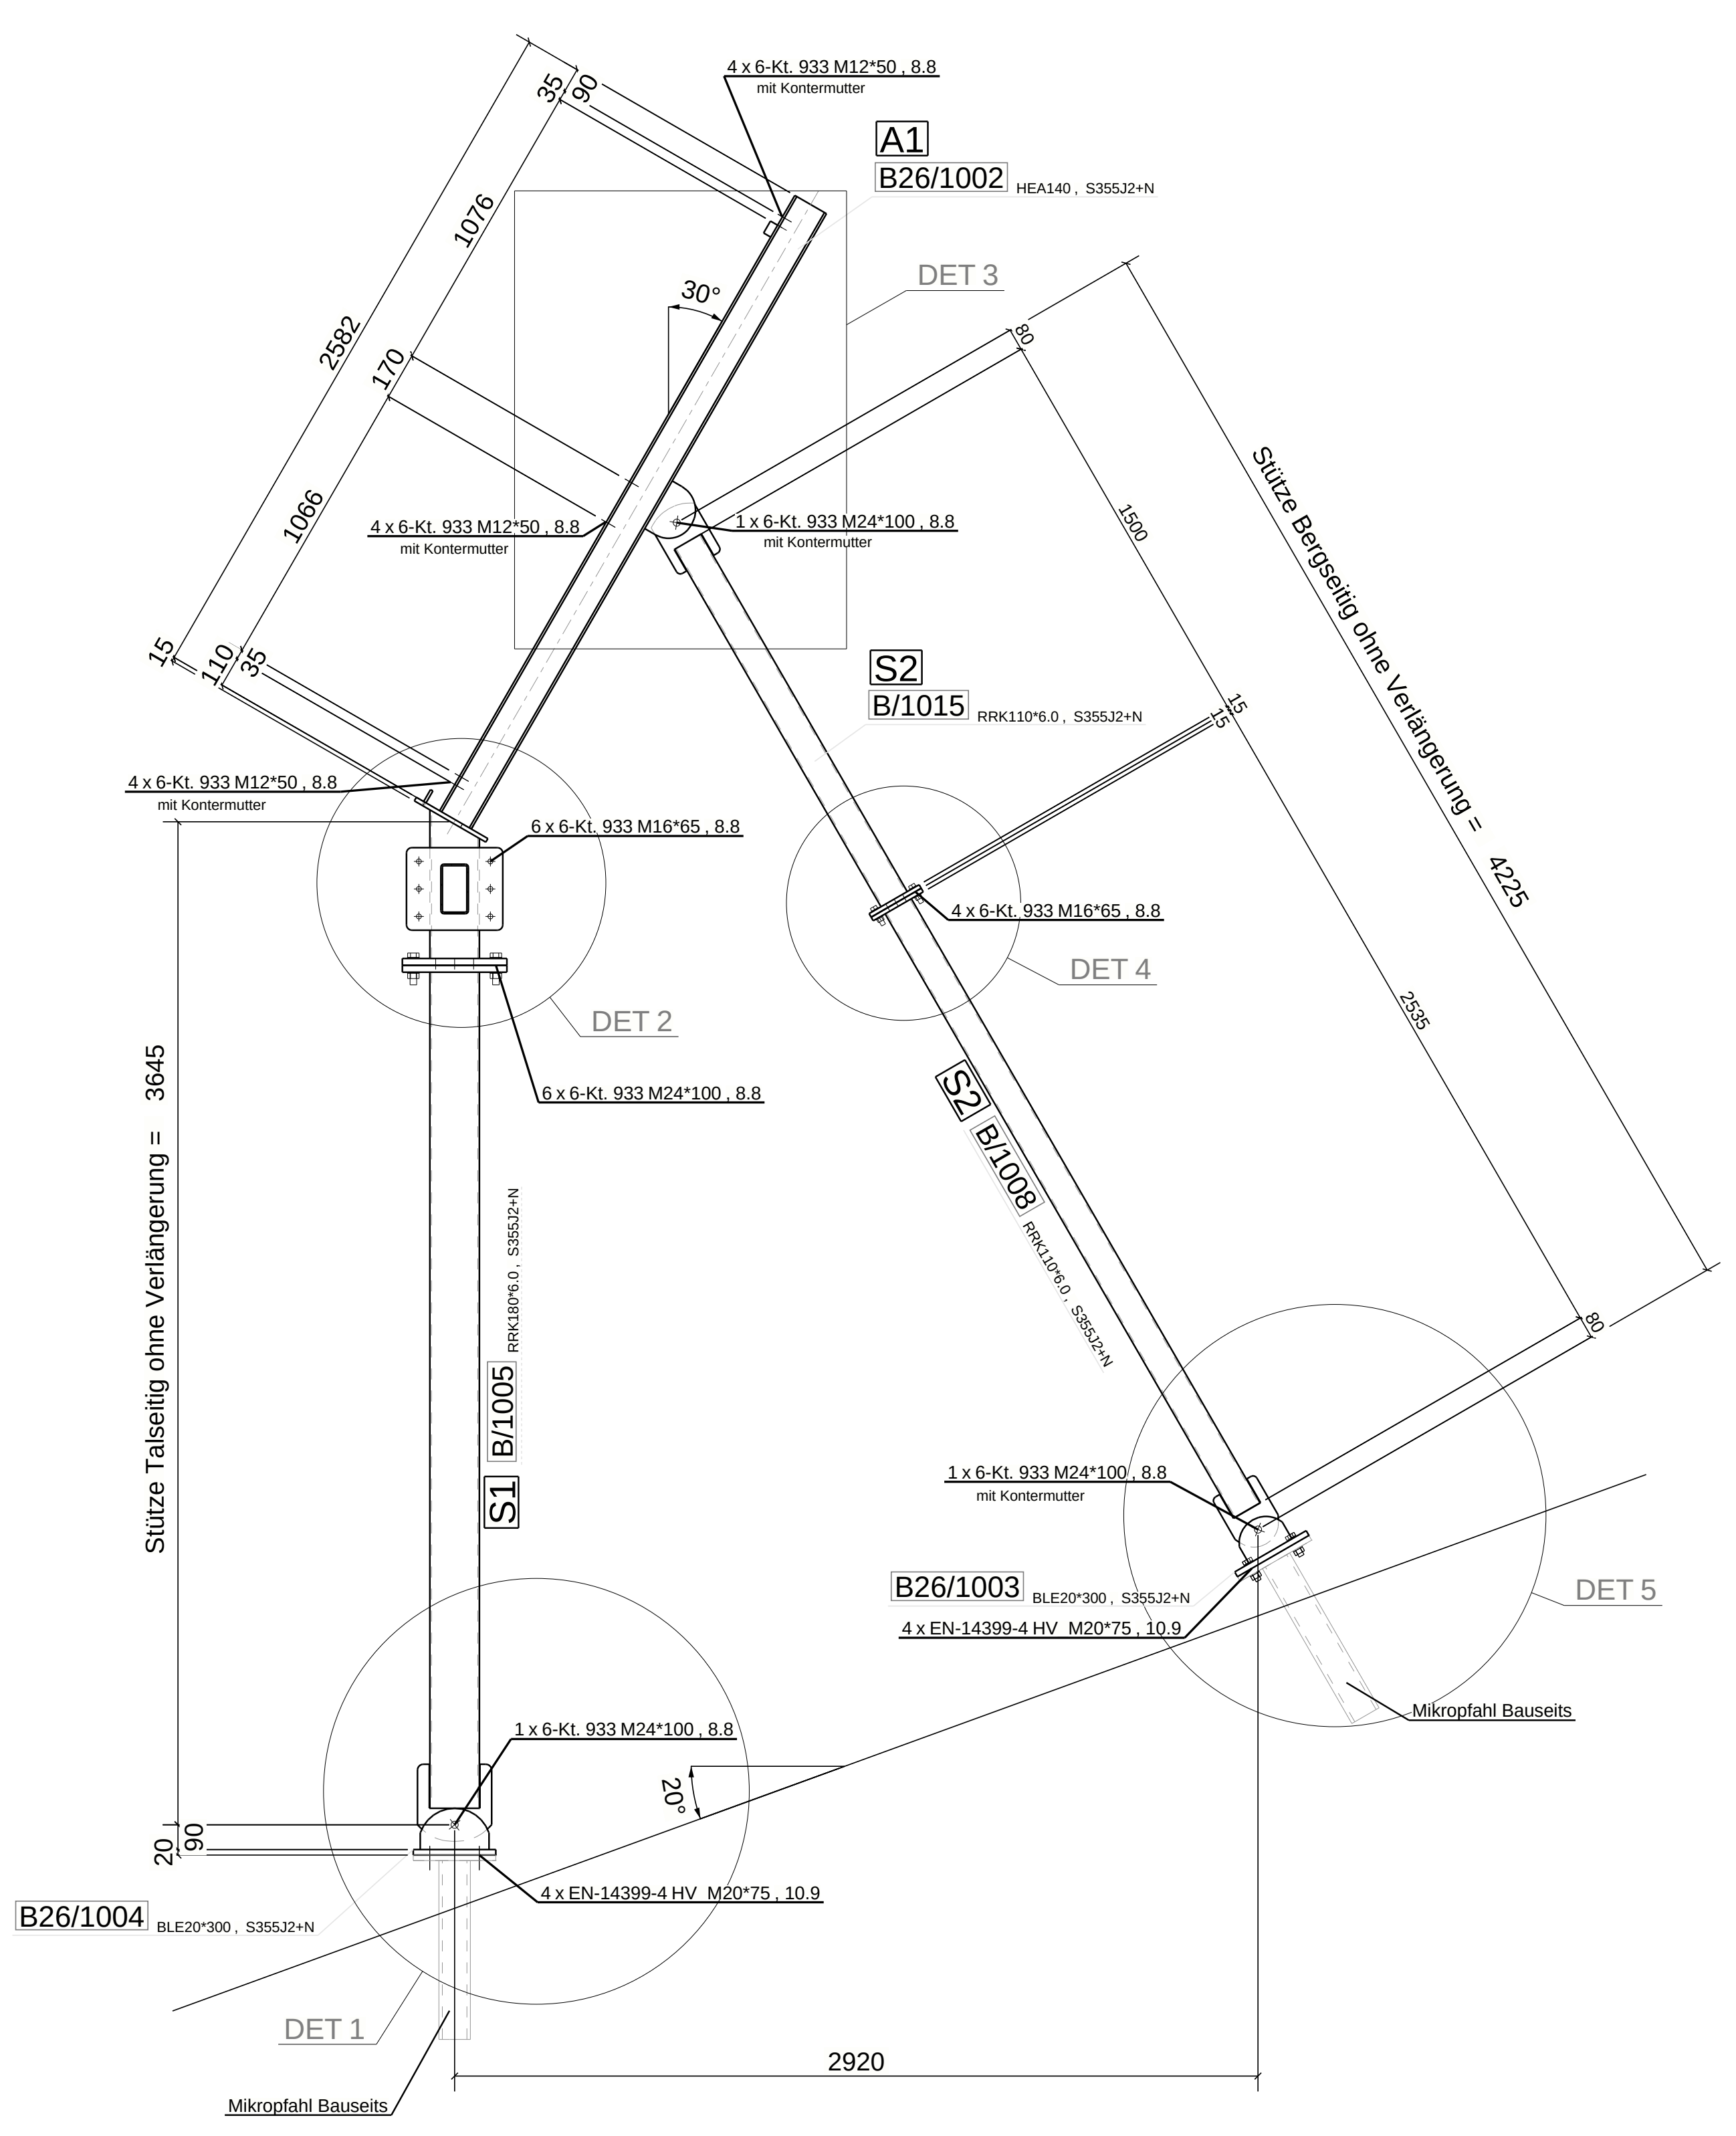
4 x 6-Kt. 933 M12*50 , 8.8
mit Kontermutter
A1
B26/1002
HEA140 , S355J2+N
DET 3
30°
4 x 6-Kt. 933 M12*50 , 8.8
mit Kontermutter
1 x 6-Kt. 933 M24*100 , 8.8
mit Kontermutter
S2
B/1015
RRK110*6.0 , S355J2+N
Stütze Bergseitig ohne Verlängerung = 4225
4 x 6-Kt. 933 M12*50 , 8.8
mit Kontermutter
6 x 6-Kt. 933 M16*65 , 8.8
DET 2
6 x 6-Kt. 933 M16*65 , 8.8
DET 4
6 x 6-Kt. 933 M24*100 , 8.8
S2
B/1008
RRK110*6.0 , S355J2+N
Stütze Talseitig ohne Verlängerung = 3645
S1
B/1005
RRK180*6.0 , S355J2+N
1 x 6-Kt. 933 M24*100 , 8.8
mit Kontermutter
B26/1003
BLE20*300 , S355J2+N
4 x EN-14399-4 HV M20*75 , 10.9
DET 5
Mikropfahl Bauseits
1 x 6-Kt. 933 M24*100 , 8.8
20°
4 x EN-14399-4 HV M20*75 , 10.9
B26/1004
BLE20*300 , S355J2+N
DET 1
2920
Mikropfahl Bauseits

Ansicht: Primärkonstruktion Typ B - 2026
1:20

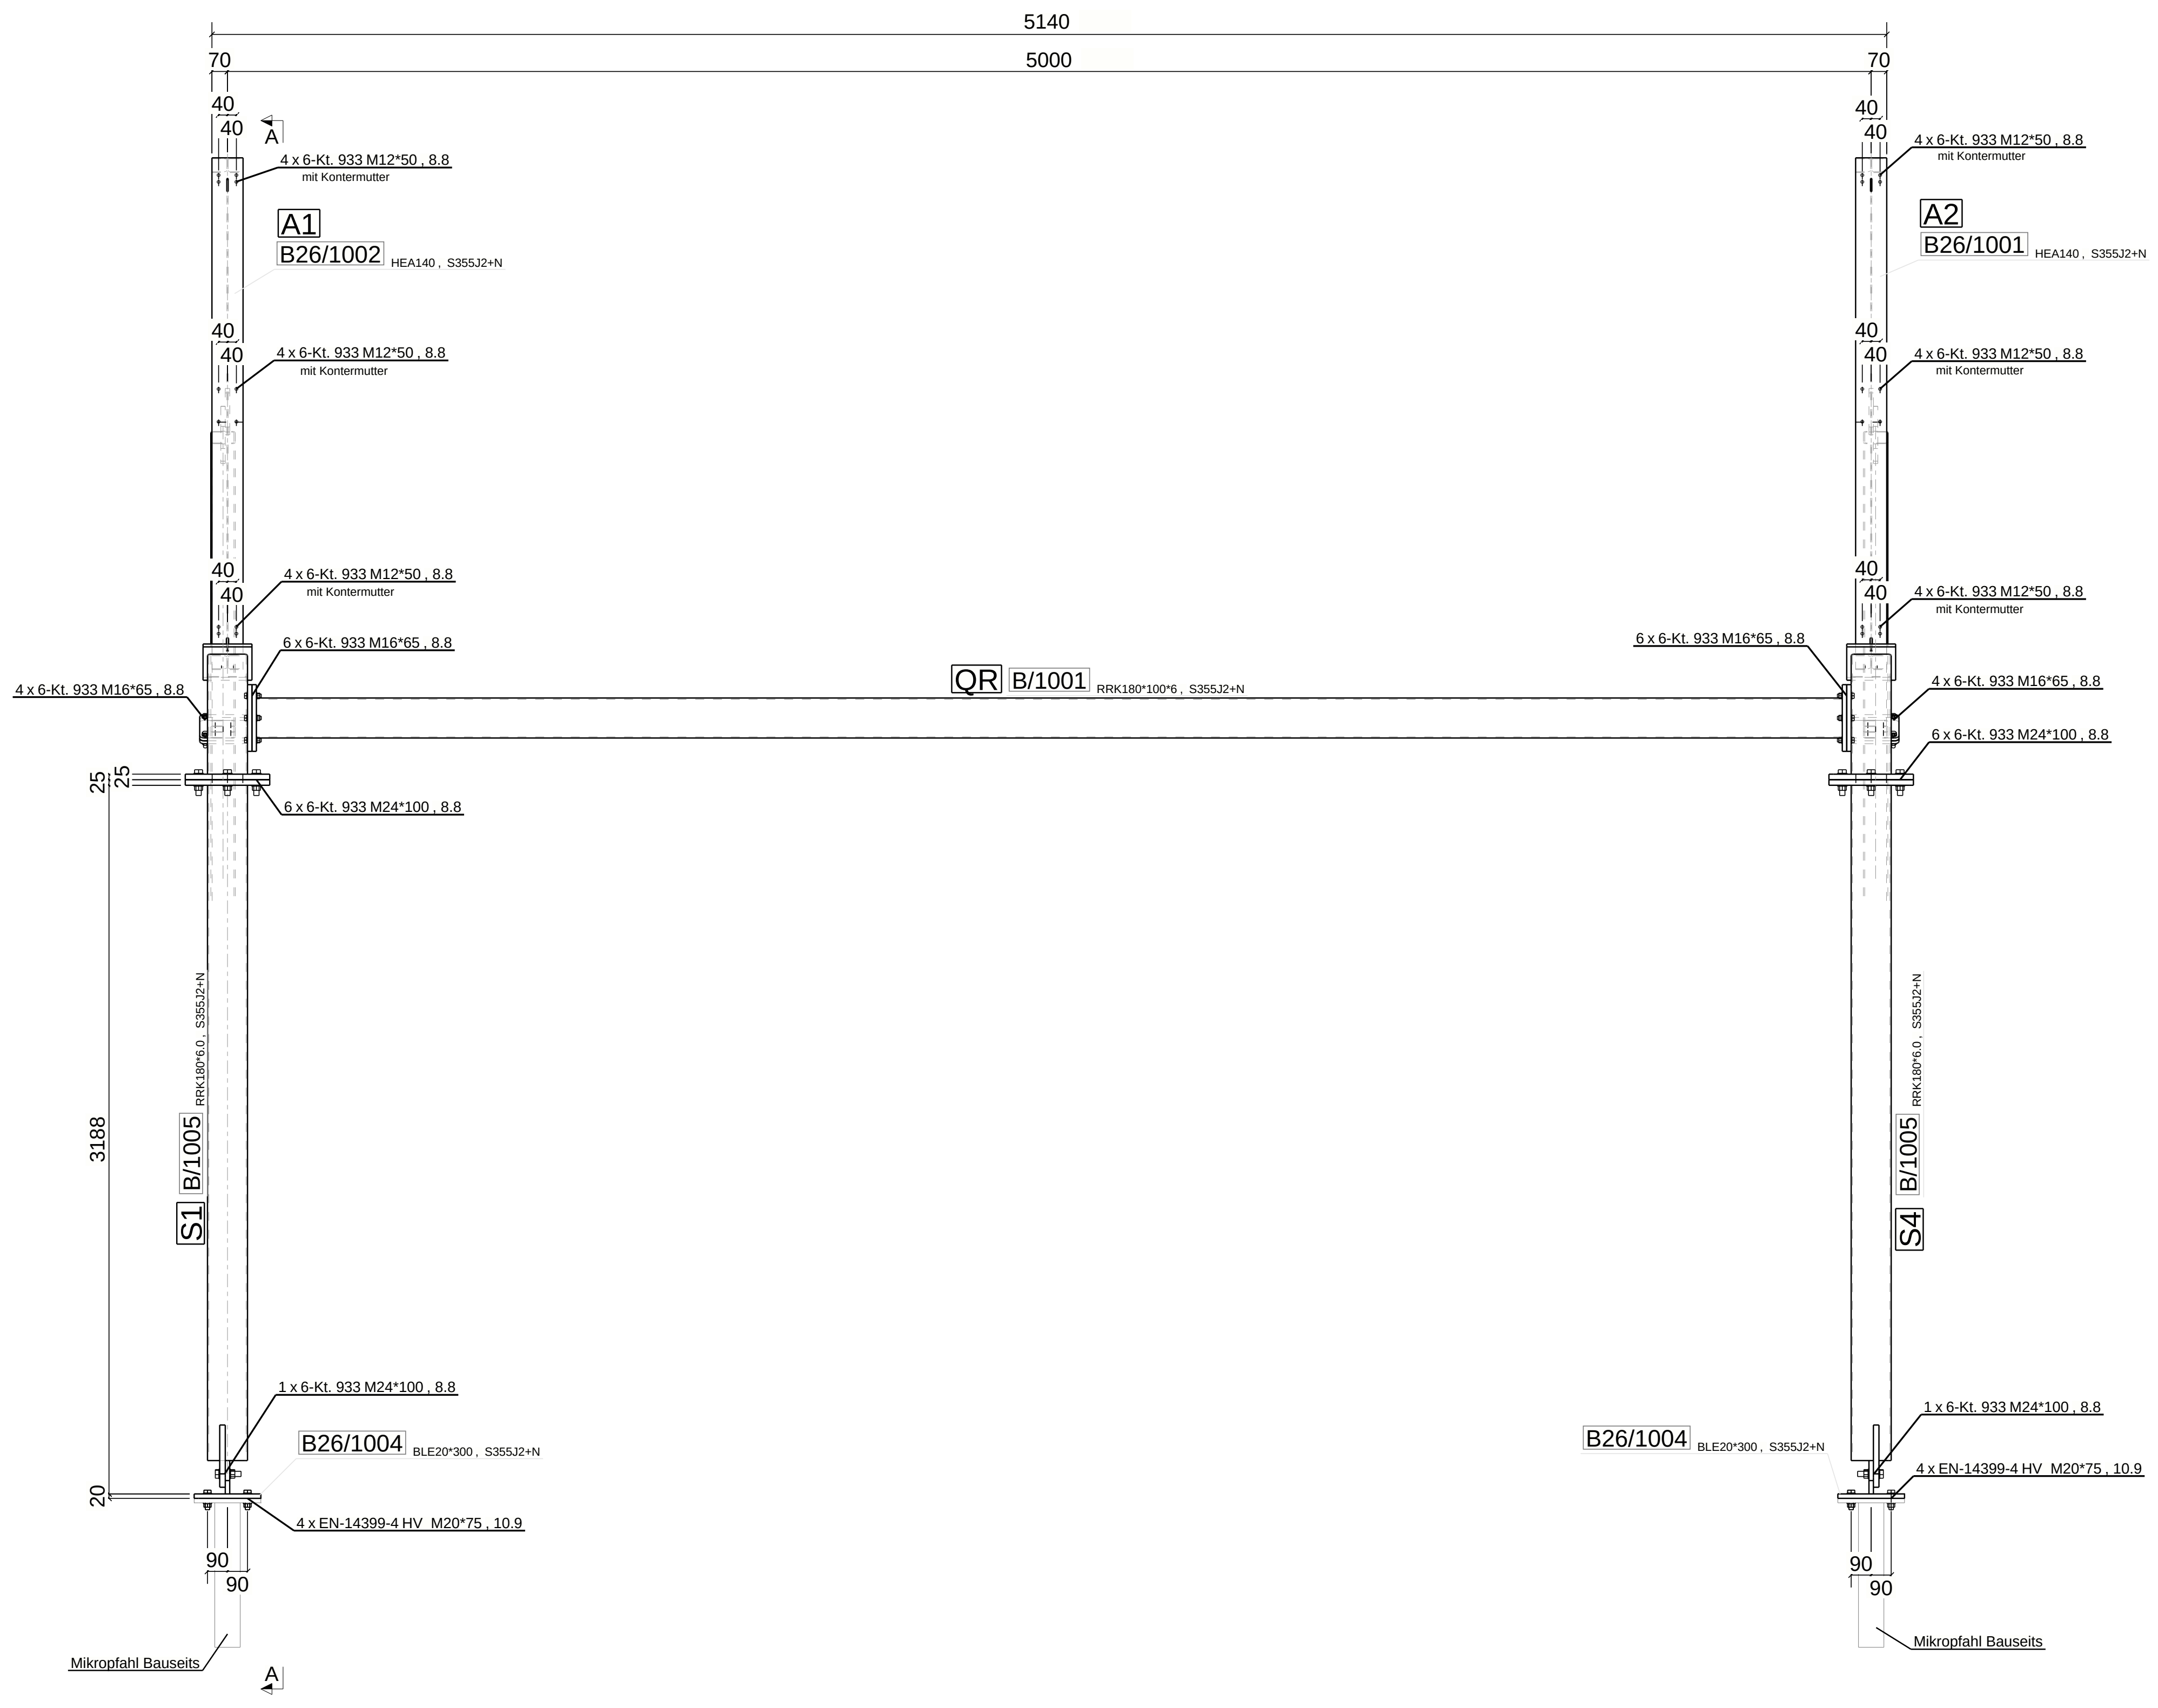
5140
70
5000
70
A
4 x 6-Kt. 933 M12*50 , 8.8
mit Kontermutter
A1
B26/1002
HEA140 , S355J2+N
4 x 6-Kt. 933 M12*50 , 8.8
mit Kontermutter
A2
B26/1001
HEA140 , S355J2+N
4 x 6-Kt. 933 M12*50 , 8.8
mit Kontermutter
6 x 6-Kt. 933 M16*65 , 8.8
4 x 6-Kt. 933 M16*65 , 8.8
QR
B/1001
RRK180*100*6 , S355J2+N
4 x 6-Kt. 933 M16*65 , 8.8
6 x 6-Kt. 933 M24*100 , 8.8
6 x 6-Kt. 933 M24*100 , 8.8
3188
S1
B/1005
RRK180*6.0 , S355J2+N
S4
B/1005
RRK180*6.0 , S355J2+N
1 x 6-Kt. 933 M24*100 , 8.8
B26/1004
BLE20*300 , S355J2+N
4 x EN-14399-4 HV M20*75 , 10.9
B26/1004
BLE20*300 , S355J2+N
1 x 6-Kt. 933 M24*100 , 8.8
4 x EN-14399-4 HV M20*75 , 10.9
Mikropfahl Bauseits
Mikropfahl Bauseits

Isometrie Primärkonstruktion Typ B - 2026

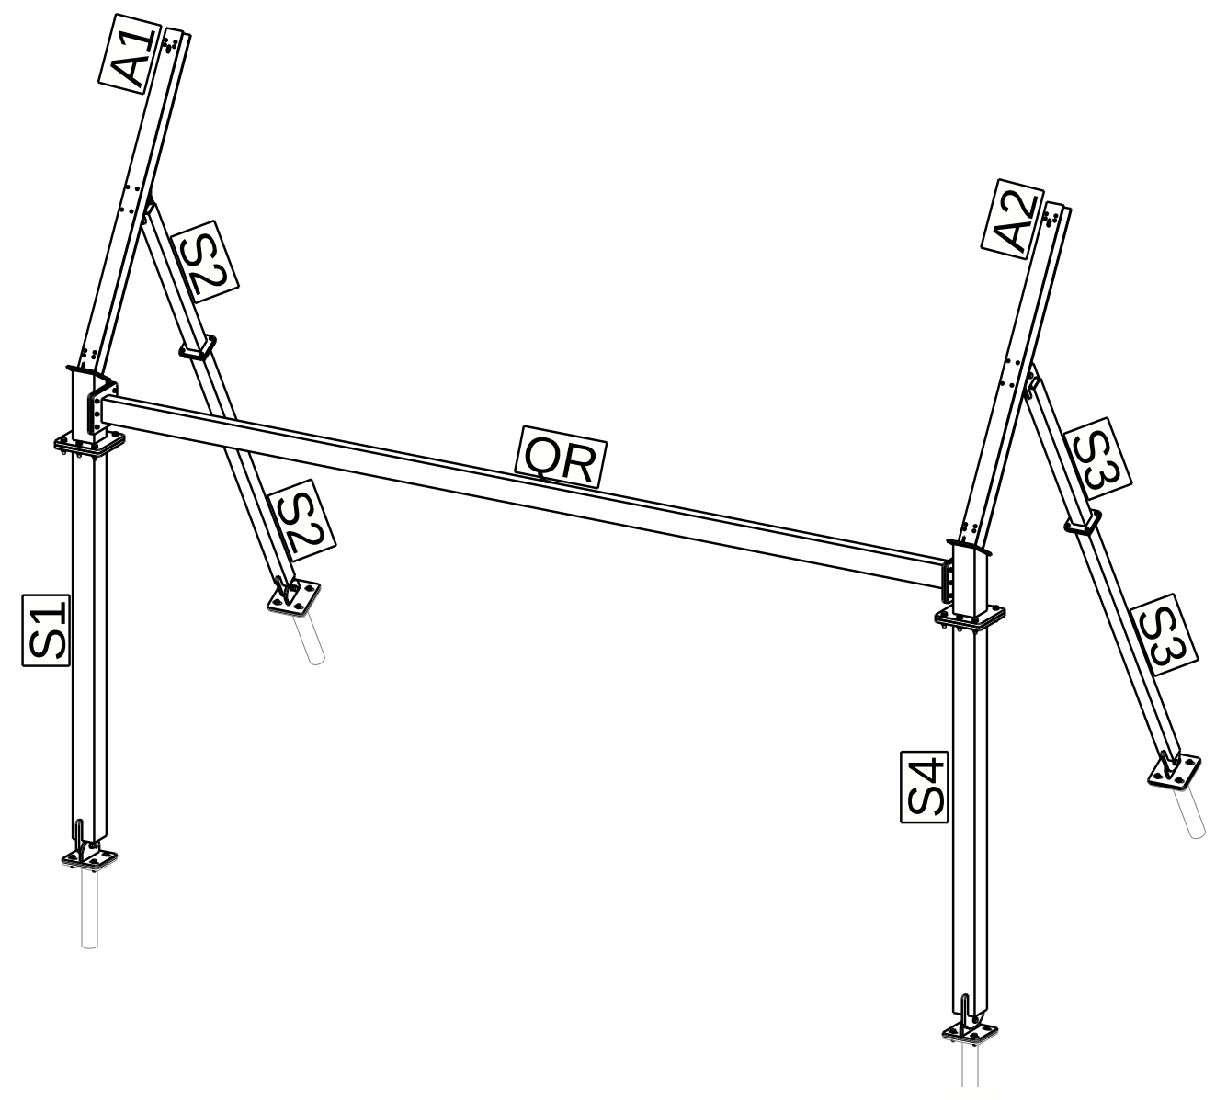

DETAIL 2 : talseitige Stütze (S1/S4) - Mst: 1:10

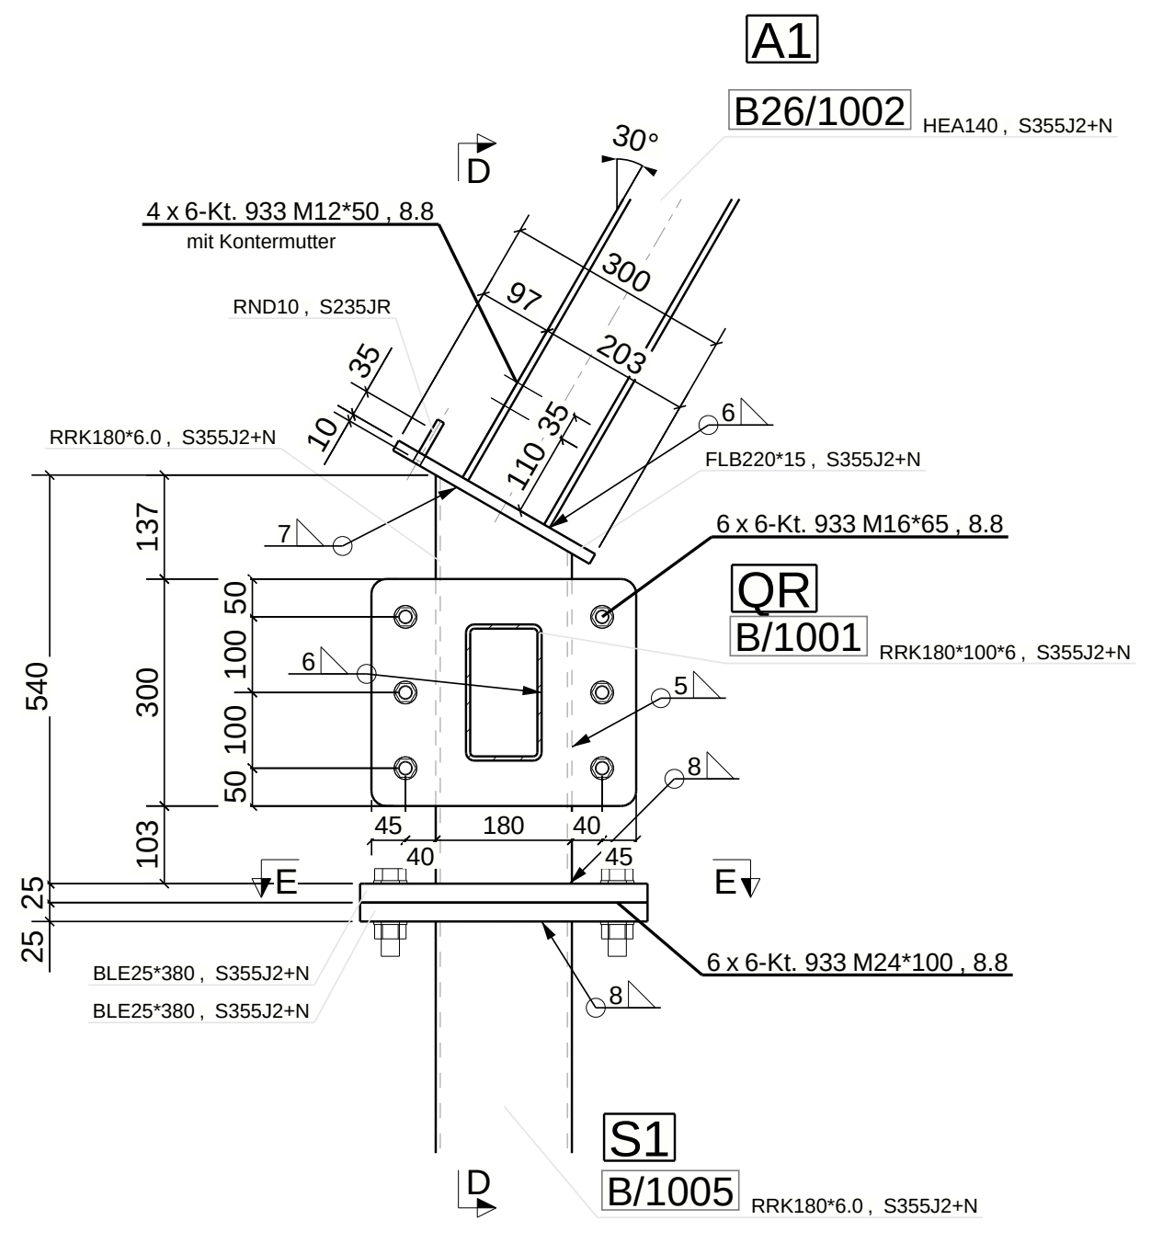

DETAIL 2, Schnitt D - D : talseitige Stütze (S1/S4)
1:10

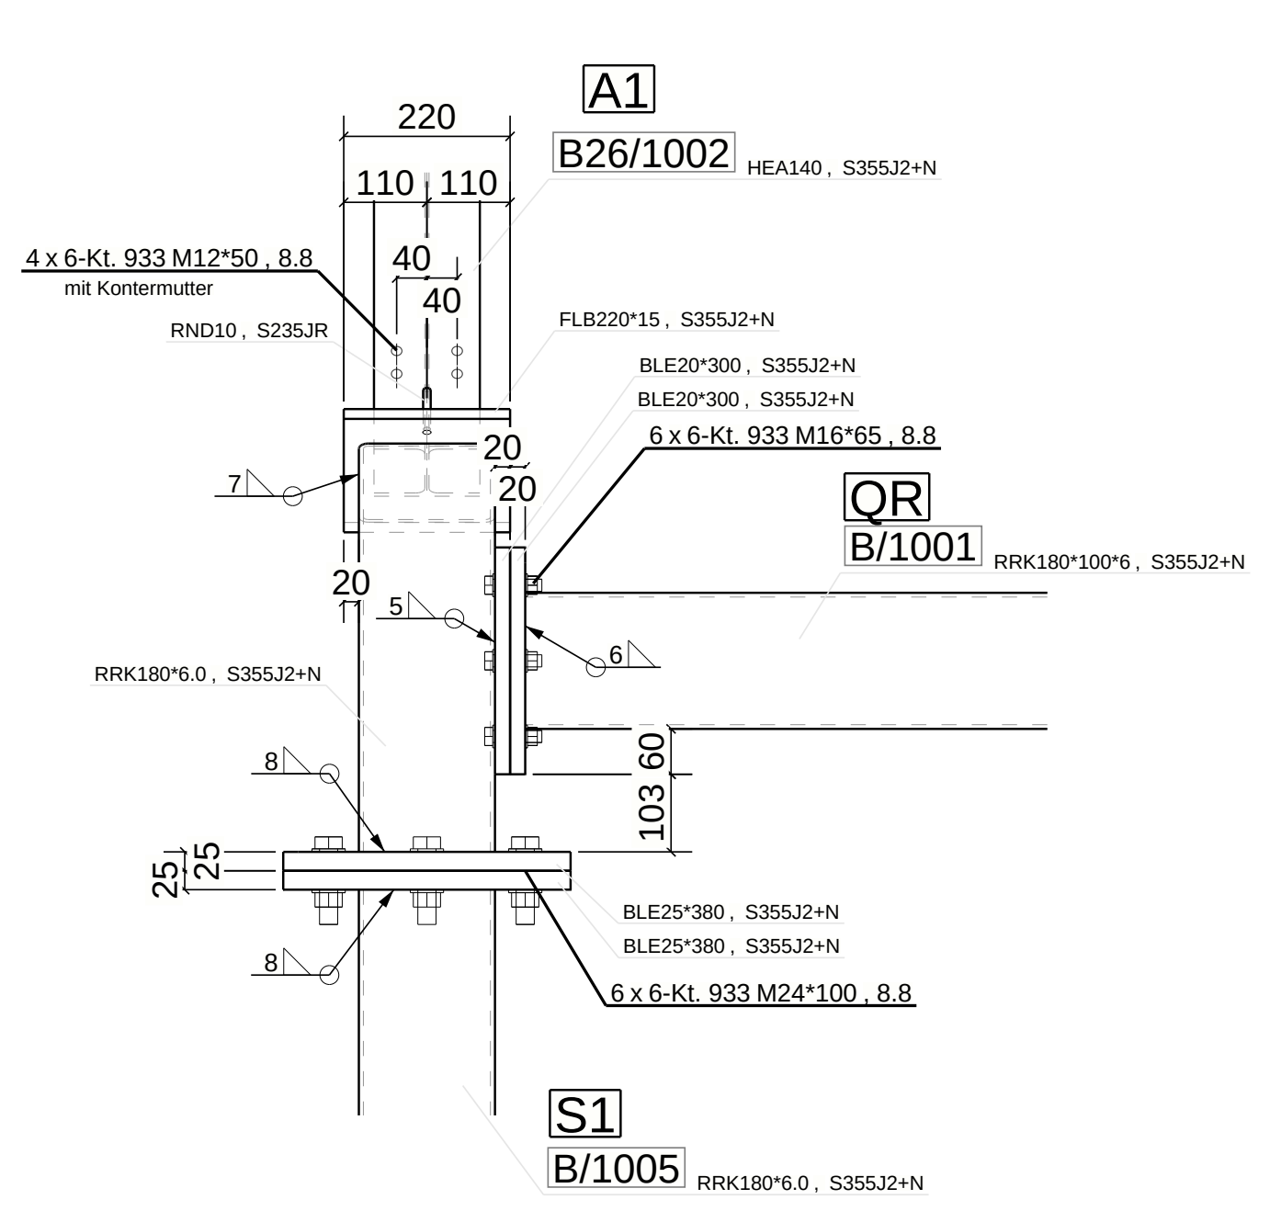

DETAIL 2, Schnitt E - E : talseitige Stütze (S1/S4)
1:10

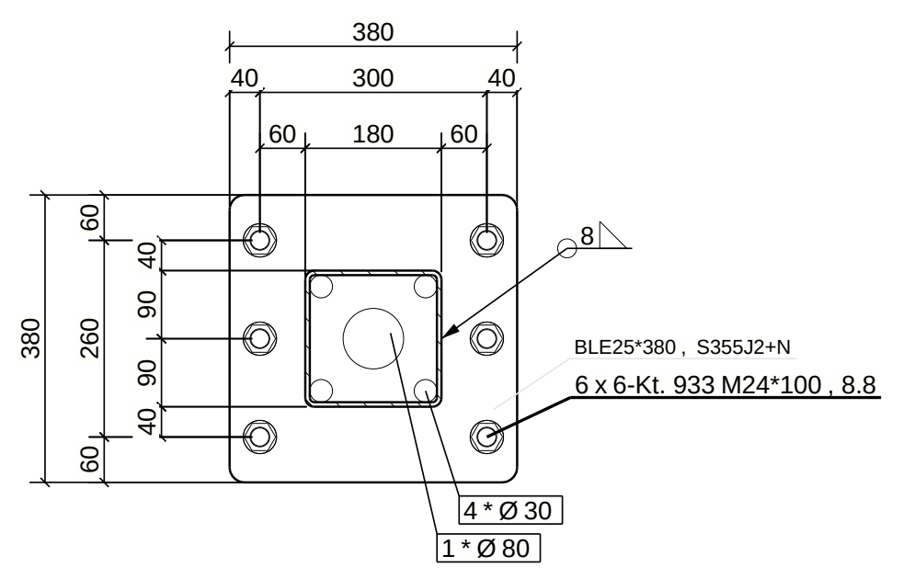

DETAIL 4 : bergseitige Stütze (S2/S3) - Mst: 1:10

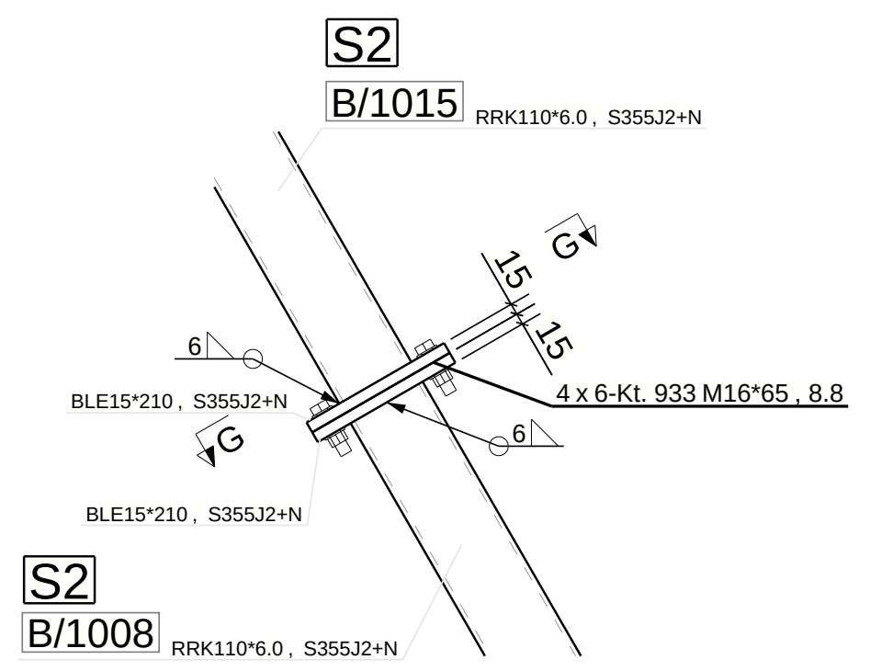

DETAIL 4, Schnitt G - G : bergseitige Stütze (S2/S3)
1:10

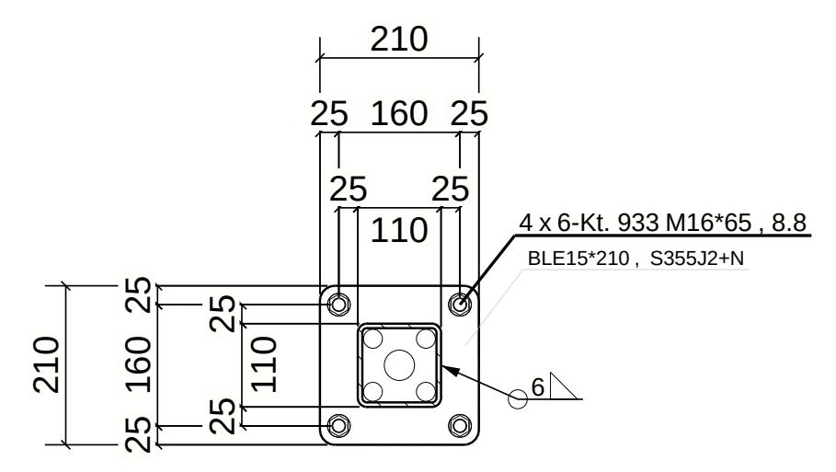

Grundriss: Primärkonstruktion Typ B - 2026
1:20

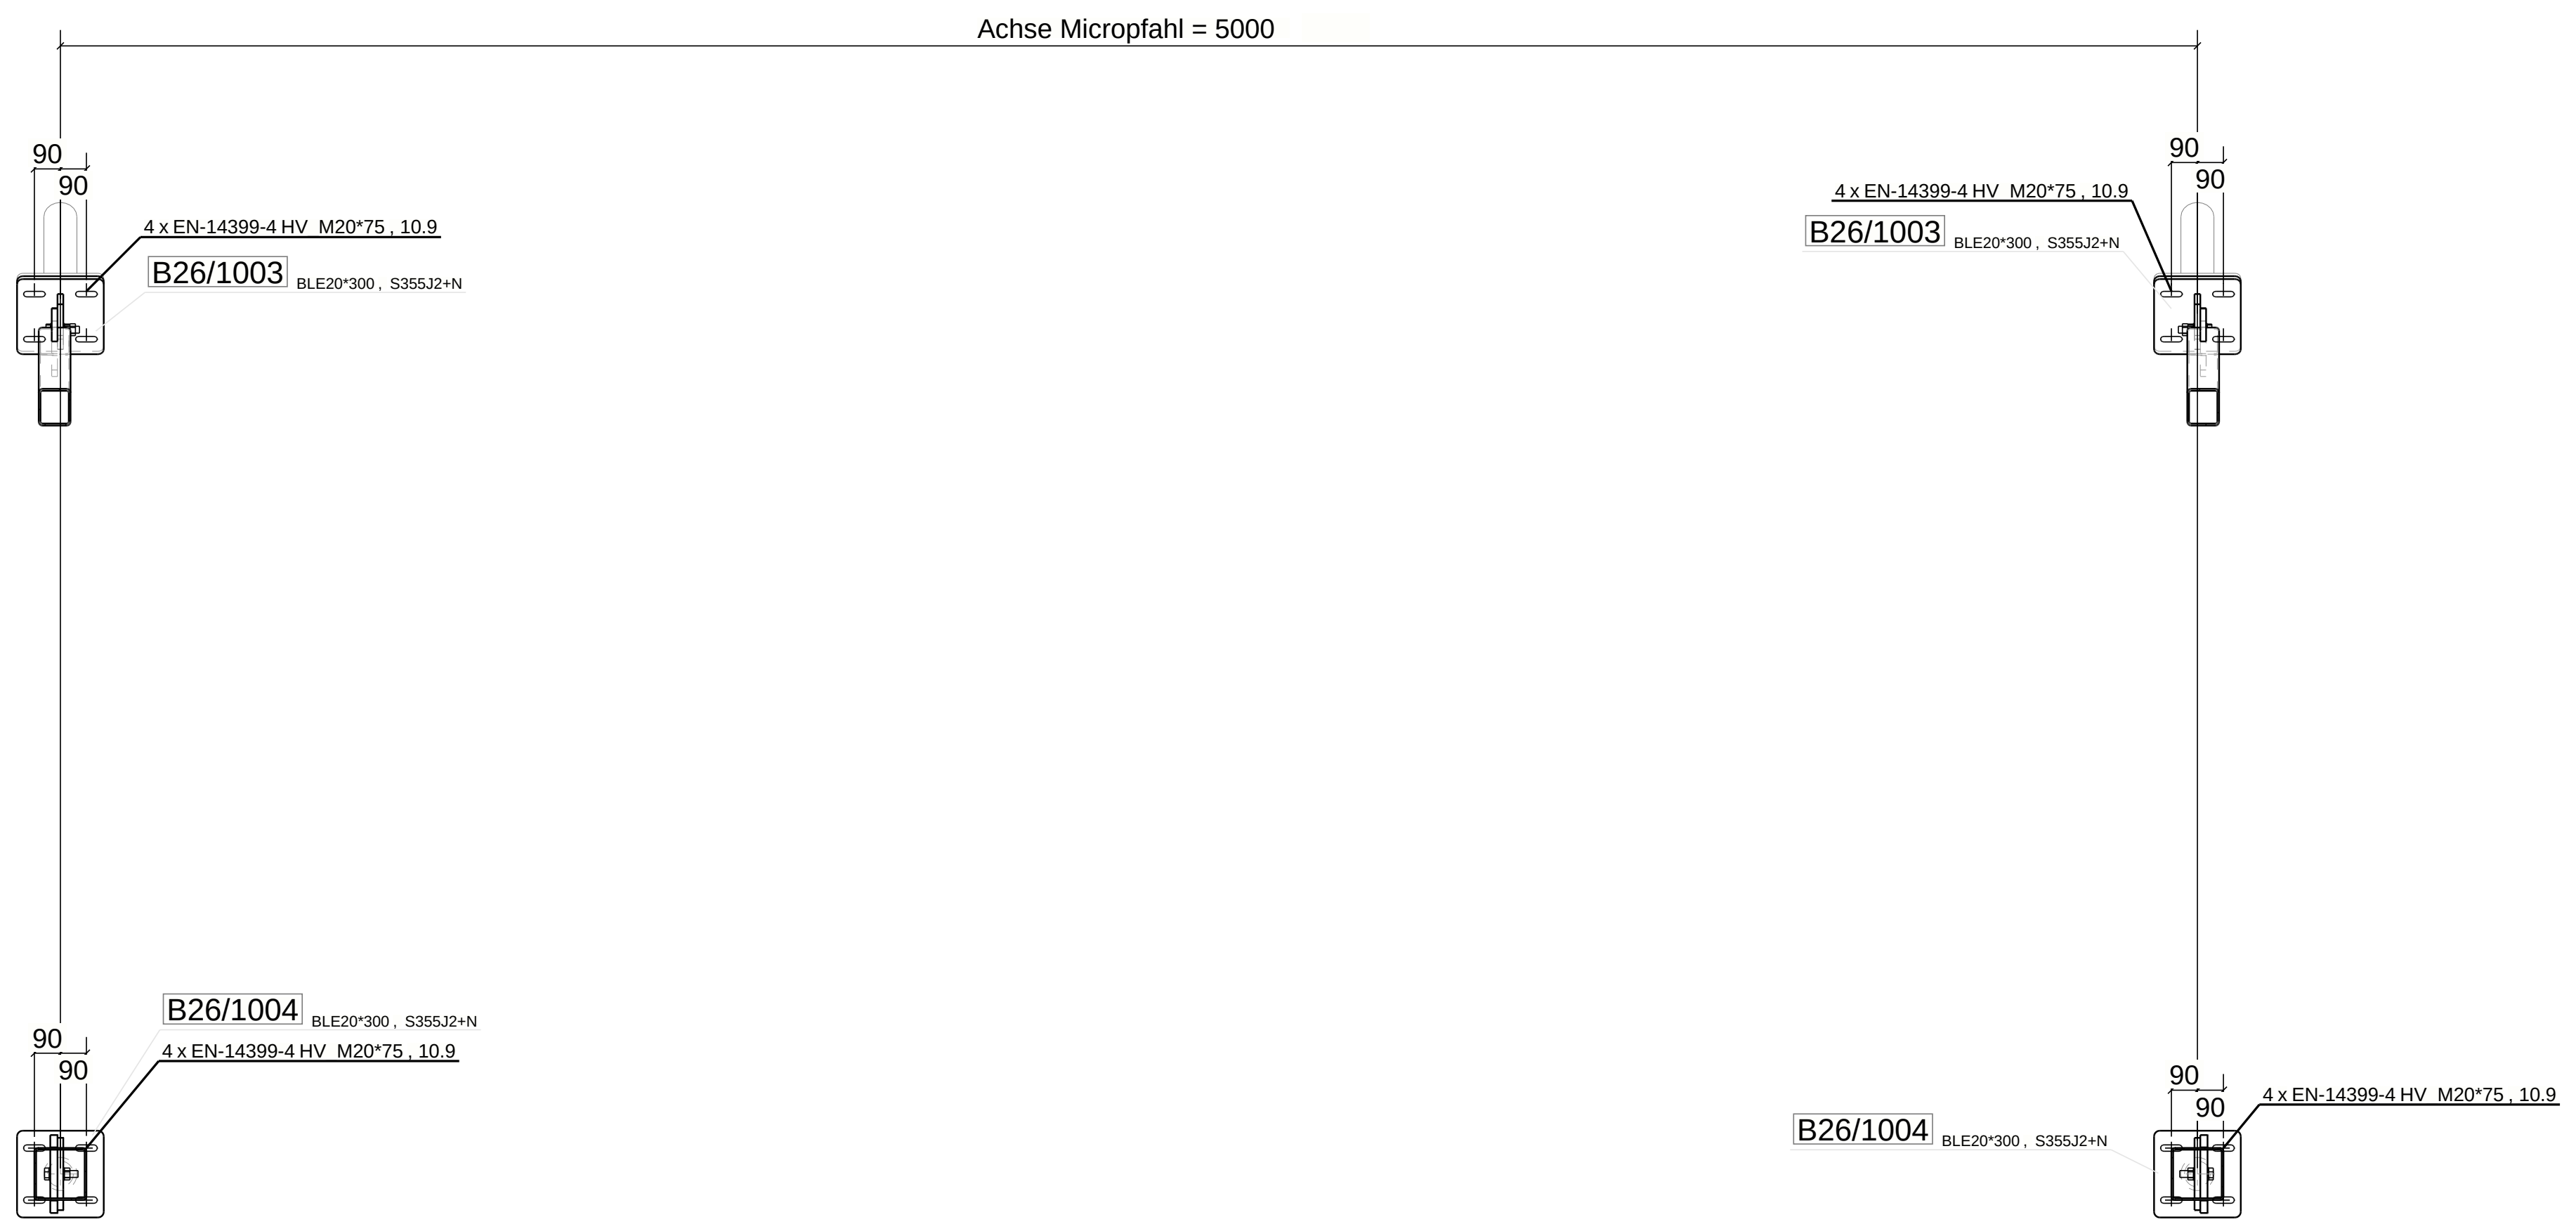

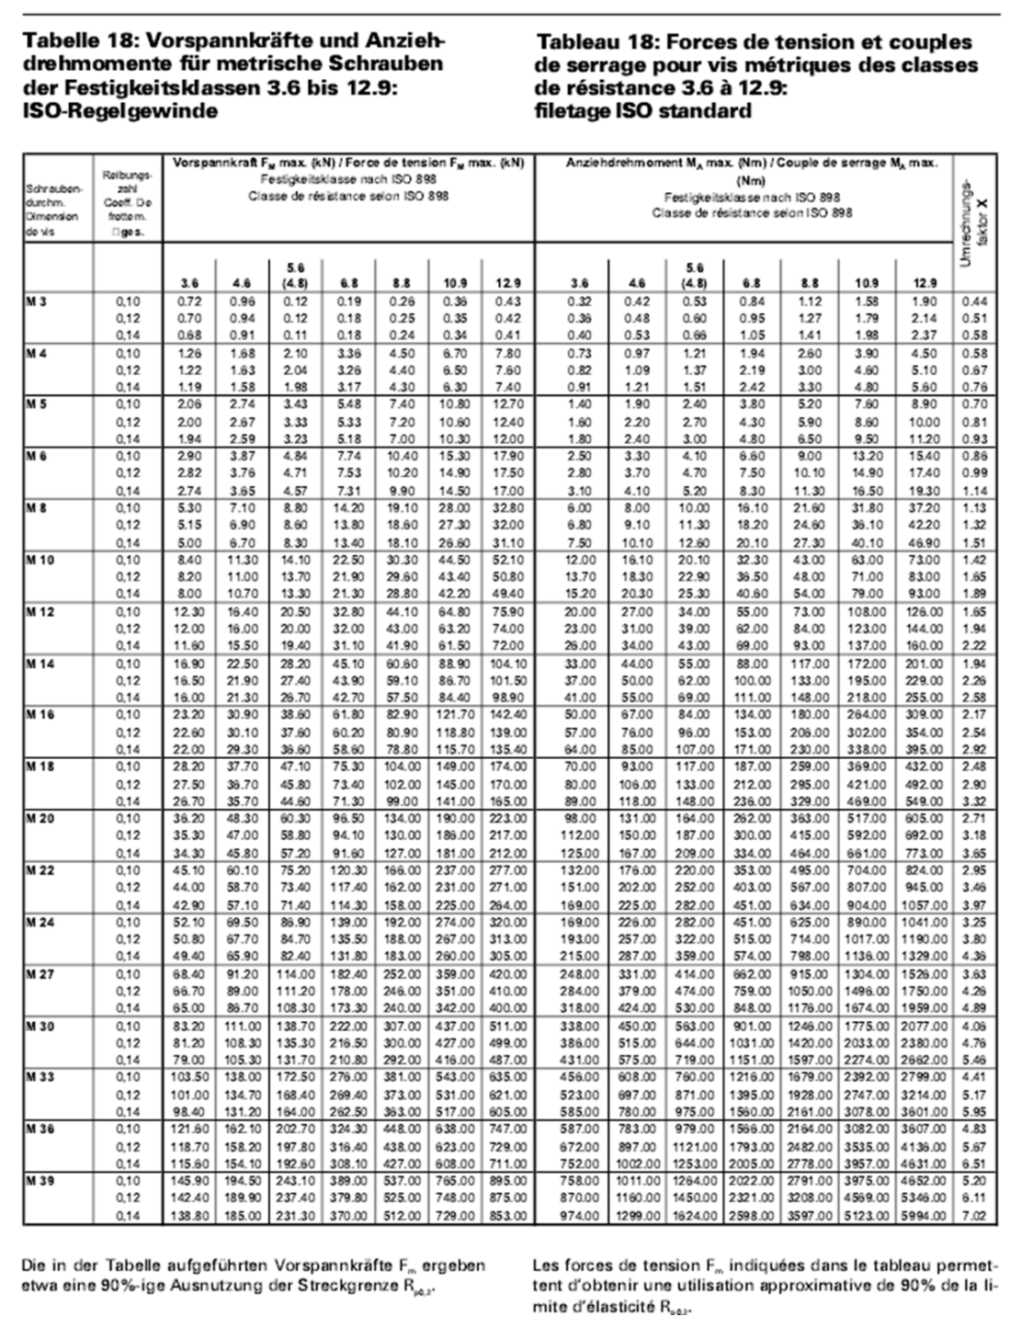

Tabelle 18: Vorspannkräfte und Anziehdrehmomente für metrische Schrauben der Festigkeitsklassen 3.6 bis 12.9: ISO-Regelgewinde

Tableau 18: Forces de tension et couples de serrage pour vis métriques des classes de résistance 3.6 à 12.9: filetage ISO standard

Schrauben-durchm. Dimension de vis	Reibungszahl Coeff. De frottem. µges.	Vorspannkraft F_M max. (kN) / Force de tension F_M max. (kN) Festigkeitsklasse nach ISO 898 Classe de résistance selon ISO 898							Anziehdrehmoment M_A max. (Nm) / Couple de serrage M_A max. (Nm) Festigkeitsklasse nach ISO 898 Classe de résistance selon ISO 898							Umrechnungsfaktor X
		3.6	4.6	5.6 (4.8)	6.8	8.8	10.9	12.9	3.6	4.6	5.6 (4.8)	6.8	8.8	10.9	12.9	
M 3	0,10	0.72	0.96	0.12	0.19	0.26	0.36	0.43	0.32	0.42	0.53	0.84	1.12	1.58	1.90	0.44
	0,12	0.70	0.94	0.12	0.18	0.25	0.35	0.42	0.36	0.48	0.60	0.95	1.27	1.79	2.14	0.51
	0,14	0.68	0.91	0.11	0.18	0.24	0.34	0.41	0.40	0.53	0.66	1.05	1.41	1.98	2.37	0.58
M 4	0,10	1.26	1.68	2.10	3.36	4.50	6.70	7.80	0.73	0.97	1.21	1.94	2.60	3.90	4.50	0.58
	0,12	1.22	1.63	2.04	3.26	4.40	6.50	7.60	0.82	1.09	1.37	2.19	3.00	4.60	5.10	0.67
	0,14	1.19	1.58	1.98	3.17	4.30	6.30	7.40	0.91	1.21	1.51	2.42	3.30	4.80	5.60	0.76
M 5	0,10	2.06	2.74	3.43	5.48	7.40	10.80	12.70	1.40	1.90	2.40	3.80	5.20	7.60	8.90	0.70
	0,12	2.00	2.67	3.33	5.33	7.20	10.60	12.40	1.60	2.20	2.70	4.30	5.90	8.60	10.00	0.81
	0,14	1.94	2.59	3.23	5.18	7.00	10.30	12.00	1.80	2.40	3.00	4.80	6.50	9.50	11.20	0.93
M 6	0,10	2.90	3.87	4.84	7.74	10.40	15.30	17.90	2.50	3.30	4.10	6.60	9.00	13.20	15.40	0.86
	0,12	2.82	3.76	4.71	7.53	10.20	14.90	17.50	2.80	3.70	4.70	7.50	10.10	14.90	17.40	0.99
	0,14	2.74	3.65	4.57	7.31	9.90	14.50	17.00	3.10	4.10	5.20	8.30	11.30	16.50	19.30	1.14
M 8	0,10	5.30	7.10	8.80	14.20	19.10	28.00	32.80	6.00	8.00	10.00	16.10	21.60	31.80	37.20	1.13
	0,12	5.15	6.90	8.60	13.80	18.60	27.30	32.00	6.80	9.10	11.30	18.20	24.60	36.10	42.20	1.32
	0,14	5.00	6.70	8.30	13.40	18.10	26.60	31.10	7.50	10.10	12.60	20.10	27.30	40.10	46.90	1.51
M 10	0,10	8.40	11.30	14.10	22.50	30.30	44.50	52.10	12.00	16.10	20.10	32.30	43.00	63.00	73.00	1.42
	0,12	8.20	11.00	13.70	21.90	29.60	43.40	50.80	13.70	18.30	22.90	36.50	48.00	71.00	83.00	1.65
	0,14	8.00	10.70	13.30	21.30	28.80	42.20	49.40	15.20	20.30	25.30	40.60	54.00	79.00	93.00	1.89
M 12	0,10	12.30	16.40	20.50	32.80	44.10	64.80	75.90	20.00	27.00	34.00	55.00	73.00	108.00	126.00	1.65
	0,12	12.00	16.00	20.00	32.00	43.00	63.20	74.00	23.00	31.00	39.00	62.00	84.00	123.00	144.00	1.94
	0,14	11.60	15.50	19.40	31.10	41.90	61.50	72.00	26.00	34.00	43.00	69.00	93.00	137.00	160.00	2.22
M 14	0,10	16.90	22.50	28.20	45.10	60.60	88.90	104.10	33.00	44.00	55.00	88.00	117.00	172.00	201.00	1.94
	0,12	16.50	21.90	27.40	43.90	59.10	86.70	101.50	37.00	50.00	62.00	100.00	133.00	195.00	229.00	2.26
	0,14	16.00	21.30	26.70	42.70	57.50	84.40	98.90	41.00	55.00	69.00	111.00	148.00	218.00	255.00	2.58
M 16	0,10	23.20	30.90	38.60	61.80	82.90	121.70	142.40	50.00	67.00	84.00	134.00	180.00	264.00	309.00	2.17
	0,12	22.60	30.10	37.60	60.20	80.90	118.80	139.00	57.00	76.00	96.00	153.00	206.00	302.00	354.00	2.54
	0,14	22.00	29.30	36.60	58.60	78.80	115.70	135.40	64.00	85.00	107.00	171.00	230.00	338.00	395.00	2.92
M 18	0,10	28.20	37.70	47.10	75.30	104.00	149.00	174.00	70.00	93.00	117.00	187.00	259.00	369.00	432.00	2.48
	0,12	27.50	36.70	45.80	73.40	102.00	145.00	170.00	80.00	106.00	133.00	212.00	295.00	421.00	492.00	2.90
	0,14	26.70	35.70	44.60	71.30	99.00	141.00	165.00	89.00	118.00	148.00	236.00	329.00	469.00	549.00	3.32
M 20	0,10	36.20	48.30	60.30	96.50	134.00	190.00	223.00	98.00	131.00	164.00	262.00	363.00	517.00	605.00	2.71
	0,12	35.30	47.00	58.80	94.10	130.00	186.00	217.00	112.00	150.00	187.00	300.00	415.00	592.00	692.00	3.18
	0,14	34.30	45.80	57.20	91.60	127.00	181.00	212.00	125.00	167.00	209.00	334.00	464.00	661.00	773.00	3.65
M 22	0,10	45.10	60.10	75.20	120.30	166.00	237.00	277.00	132.00	176.00	220.00	353.00	495.00	704.00	824.00	2.95
	0,12	44.00	58.70	73.40	117.40	162.00	231.00	271.00	151.00	202.00	252.00	403.00	567.00	807.00	945.00	3.46
	0,14	42.90	57.10	71.40	114.30	158.00	225.00	264.00	169.00	225.00	282.00	451.00	634.00	904.00	1057.00	3.97
M 24	0,10	52.10	69.50	86.90	139.00	192.00	274.00	320.00	169.00	226.00	282.00	451.00	625.00	890.00	1041.00	3.25
	0,12	50.80	67.70	84.70	135.50	188.00	267.00	313.00	193.00	257.00	322.00	515.00	714.00	1017.00	1190.00	3.80
	0,14	49.40	65.90	82.40	131.80	183.00	260.00	305.00	215.00	287.00	359.00	574.00	798.00	1136.00	1329.00	4.36
M 27	0,10	68.40	91.20	114.00	182.40	252.00	359.00	420.00	248.00	331.00	414.00	662.00	915.00	1304.00	1526.00	3.63
	0,12	66.70	89.00	111.20	178.00	246.00	351.00	410.00	284.00	379.00	474.00	759.00	1050.00	1496.00	1750.00	4.26
	0,14	65.00	86.70	108.30	173.30	240.00	342.00	400.00	318.00	424.00	530.00	848.00	1176.00	1674.00	1959.00	4.89
M 30	0,10	83.20	111.00	138.70	222.00	307.00	437.00	511.00	338.00	450.00	563.00	901.00	1246.00	1775.00	2077.00	4.06
	0,12	81.20	108.30	135.30	216.50	300.00	427.00	499.00	386.00	515.00	644.00	1031.00	1420.00	2033.00	2380.00	4.76
	0,14	79.00	105.30	131.70	210.80	292.00	416.00	487.00	431.00	575.00	719.00	1151.00	1597.00	2274.00	2662.00	5.46
M 33	0,10	103.50	138.00	172.50	276.00	381.00	543.00	635.00	456.00	608.00	760.00	1216.00	1679.00	2392.00	2799.00	4.41
	0,12	101.00	134.70	168.40	269.40	373.00	531.00	621.00	523.00	697.00	871.00	1395.00	1928.00	2747.00	3214.00	5.17
	0,14	98.40	131.20	164.00	262.50	363.00	517.00	605.00	585.00	780.00	975.00	1560.00	2161.00	3078.00	3601.00	5.95
M 36	0,10	121.60	162.10	202.70	324.30	448.00	638.00	747.00	587.00	783.00	979.00	1566.00	2164.00	3082.00	3607.00	4.83
	0,12	118.70	158.20	197.80	316.40	438.00	623.00	729.00	672.00	897.00	1121.00	1793.00	2482.00	3535.00	4136.00	5.67
	0,14	115.60	154.10	192.60	308.10	427.00	608.00	711.00	752.00	1002.00	1253.00	2005.00	2778.00	3957.00	4631.00	6.51
M 39	0,10	145.90	194.50	243.10	389.00	537.00	765.00	895.00	758.00	1011.00	1264.00	2022.00	2791.00	3975.00	4652.00	5.20
	0,12	142.40	189.90	237.40	379.80	525.00	748.00	875.00	870.00	1160.00	1450.00	2321.00	3208.00	4569.00	5346.00	6.11
	0,14	138.80	185.00	231.30	370.00	512.00	729.00	853.00	974.00	1299.00	1624.00	2598.00	3597.00	5123.00	5994.00	7.02

Die in der Tabelle aufgeführten Vorspannkräfte F_m ergeben etwa eine 90%-ige Ausnutzung der Streckgrenze $R_{p0.2}$.

Les forces de tension F_m indiquées dans le tableau permettent d'obtenir une utilisation approximative de 90% de la limite d'élasticité $R_{p0.2}$.

DETAIL 1: talseitiger Stützenfuss (S1/S4) - Mst: 1:10

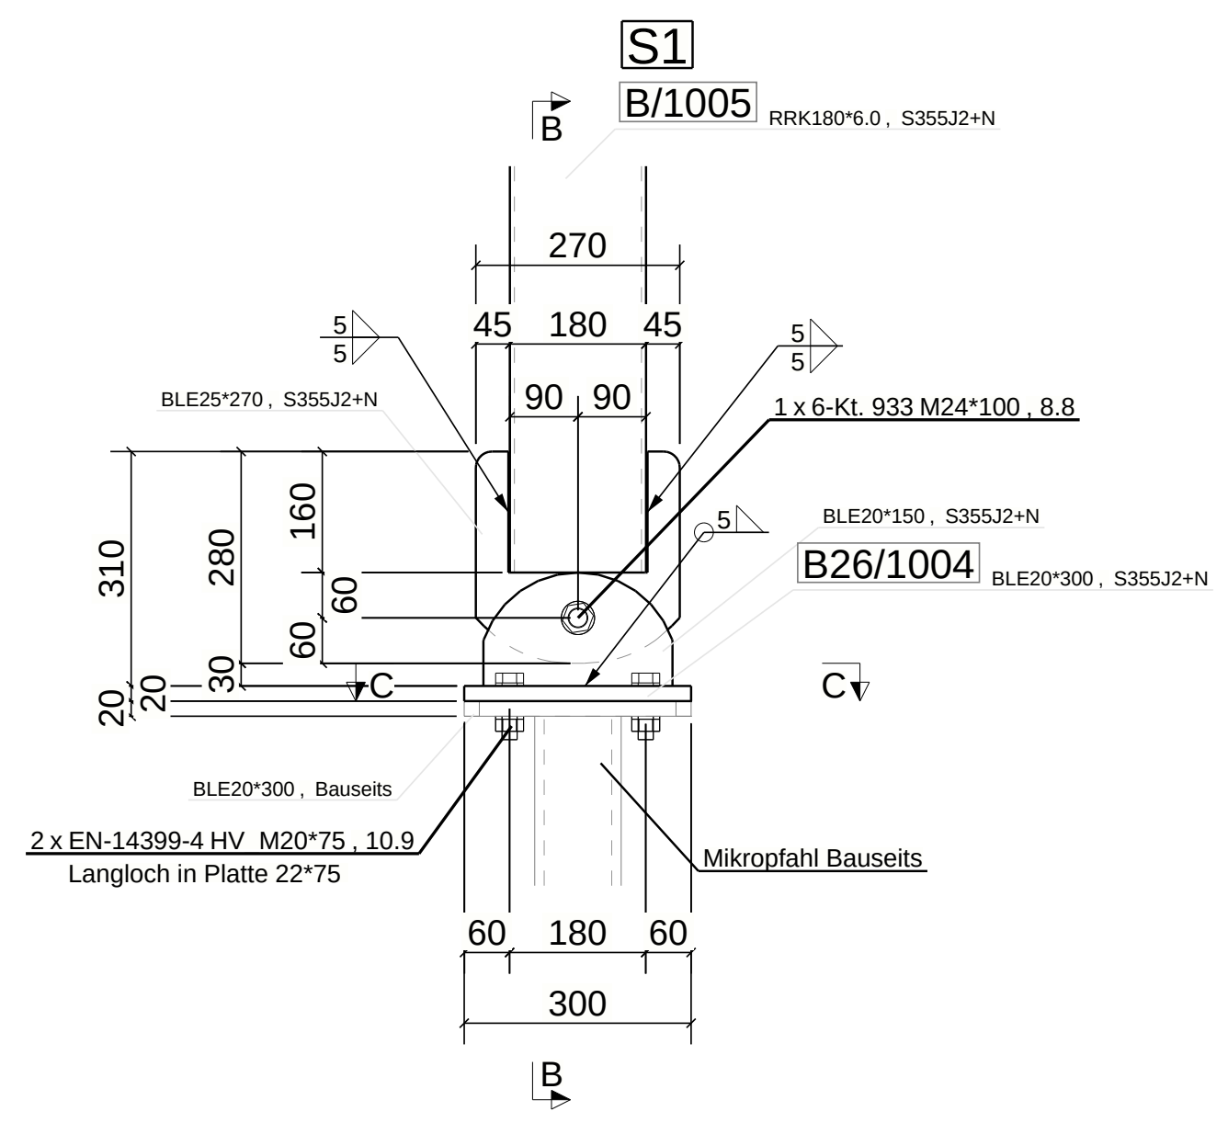

DETAIL 1, Schnitt B - B : talseitiger Stützenfuss (S1/S4)
1:10

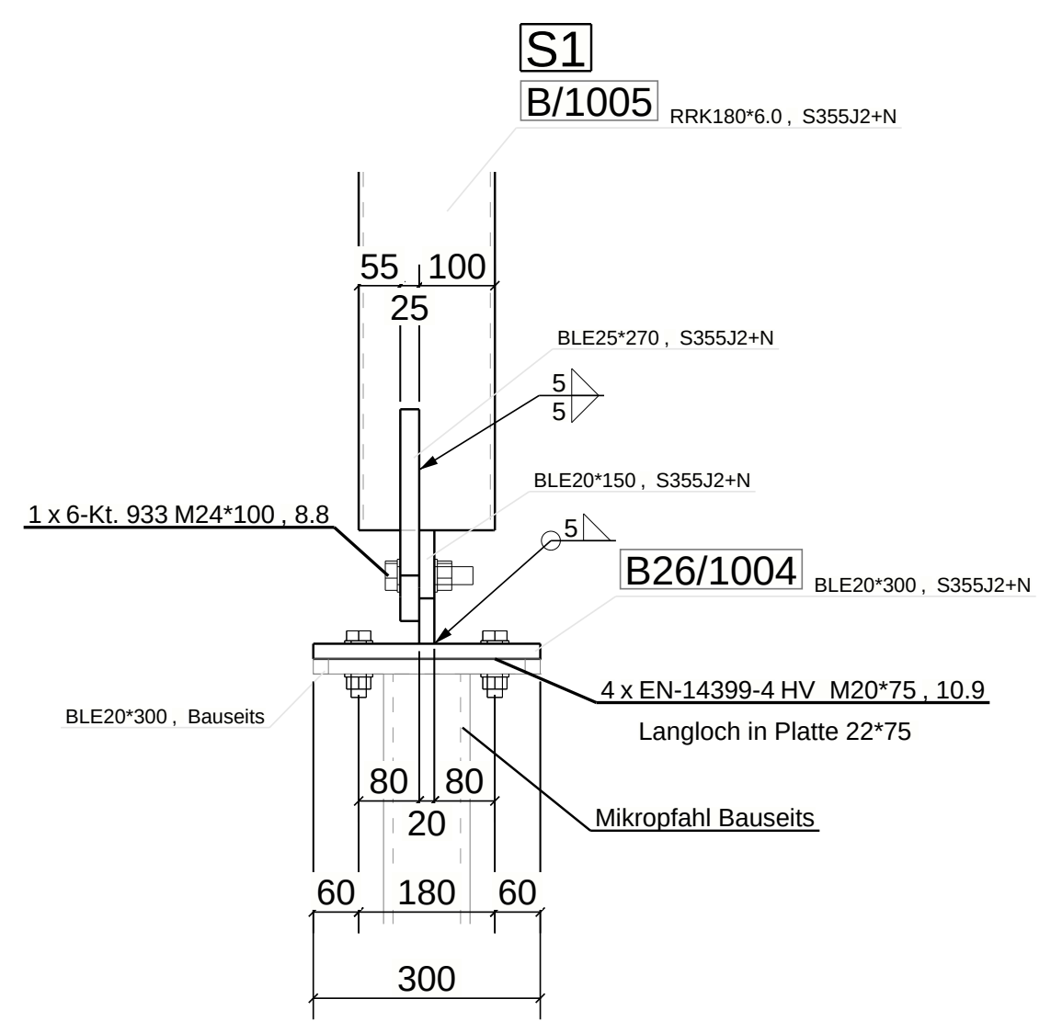

DETAIL 5 : bergseitiger Stützenfuss (S2/S3) - Mst: 1:10

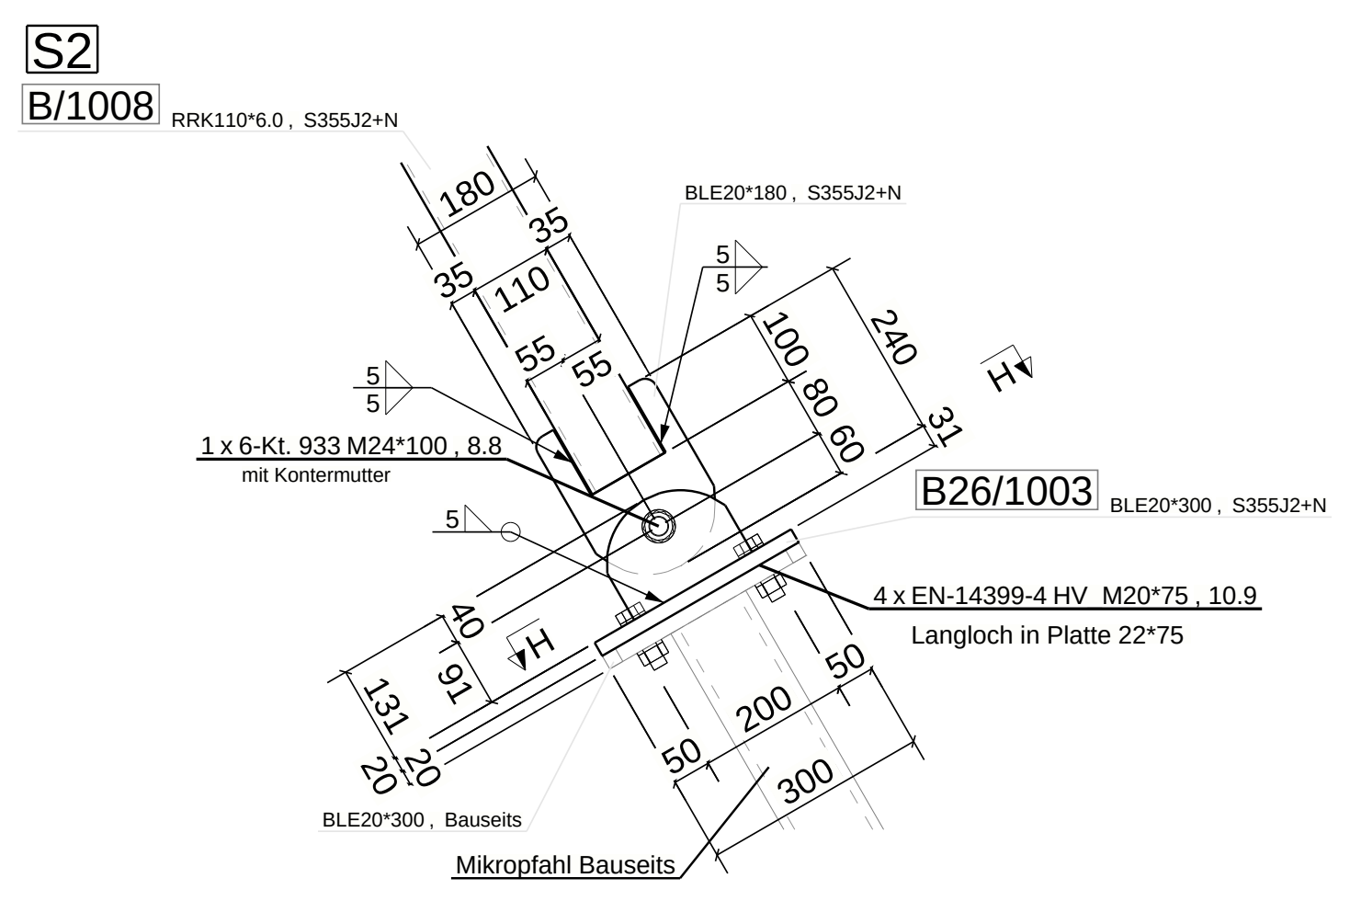

DETAIL 1, Schnitt C - C : talseitiger Stützenfuss (S1/S4)
1:10

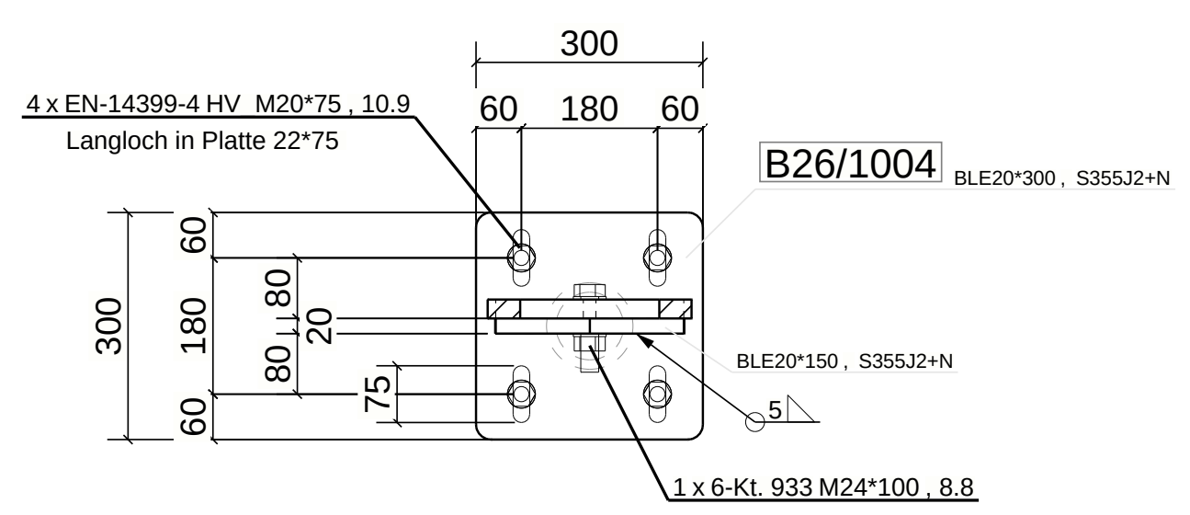

DETAIL 5, Schnitt H - H 3: bergseitiger Stützenfuss (S2/S3)
1:10

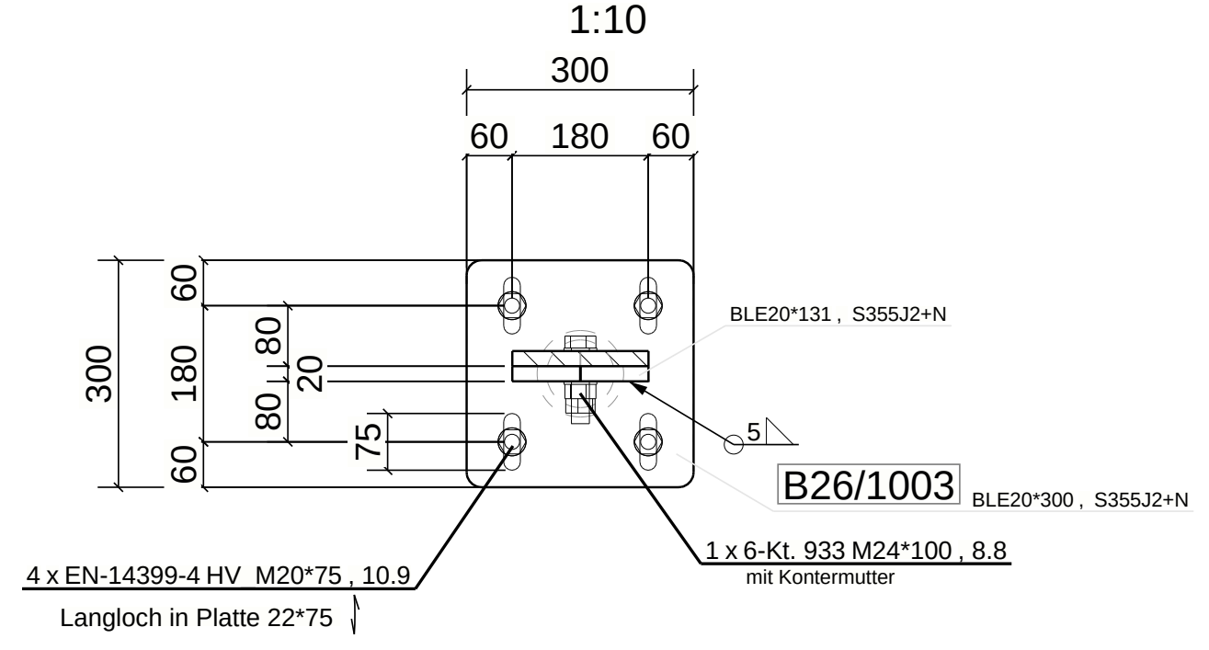

Gesamte Konstruktion ist Roh

INDEX	DATUM	ÄNDERUNG BENENNUNG	NAME

MAUCHLE
Stahlbau

Industriestrasse 9 - CH-6210 Sursee - T +41 41 925 12 51 - info@mauchlestahlbau.ch

Auftragsnr.	24027
Zeichner	P.Koch
Interne Kontrolle	
ABTEILUNG	UNTERSCHRIFT
PL	J. Mäder
MAßSTAB	1:10 1:20 1:55
ANSICHT	

BAUHERR
Axpo Solutions AG

BAUSTELLE
NalpSolar

BENENNUNG
Primärkonstruktion Typ B
Typ 2026 - für 8er Modultisch
Ansicht, Schnitte & Details

ZEICHNUNGSNUMMER

PROJEKT	ABTEILUNG	LOS	TIPOLOGIE	FORTLAUFENDE NR°	REVISION
24027	S	0	M	014	

DER INHALT DIESER ZEICHNUNG IST UNSER GEISTIGES EIGENTUM UND DARF NICHT OHNE UNSERE GENEHMIGUNG VERVIELFÄLTIGT ODER AN DRITTE PERSONEN WEITERGEGEBEN WERDEN.