## DETAIL 3, Schnitt F - F : Auflageträger (A1)
1:10

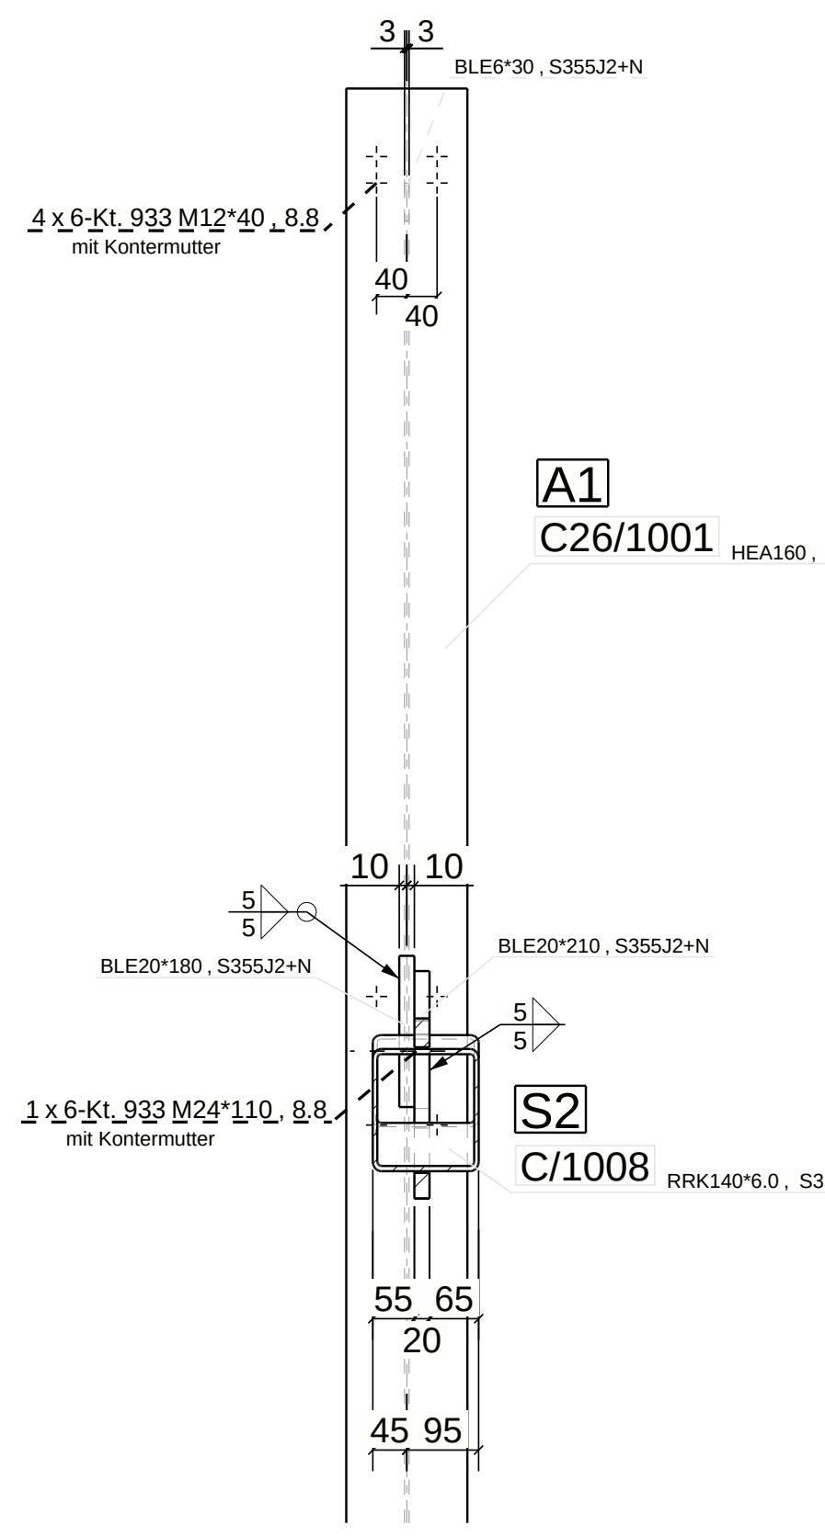

## DETAIL 3 : Auflageträger (A1) - Mst: 1:10

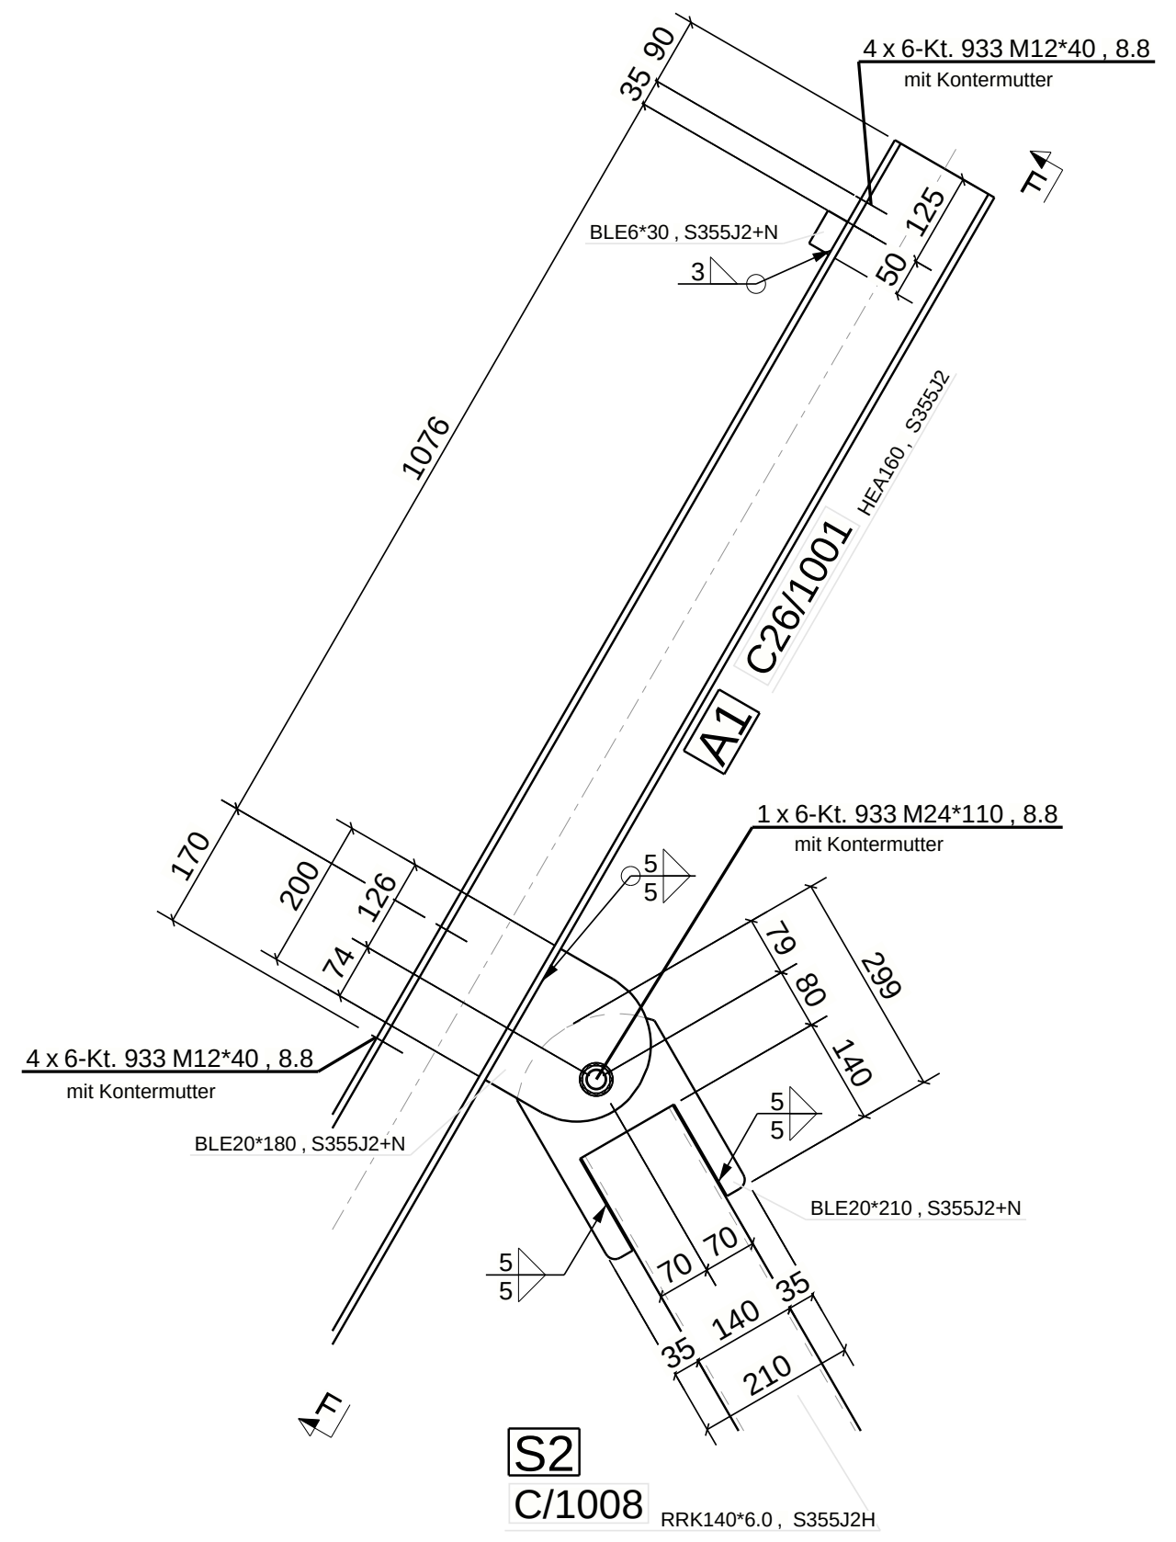

## A - A
## Schnitt: Primärkonstruktion Typ C - 2026
1:20

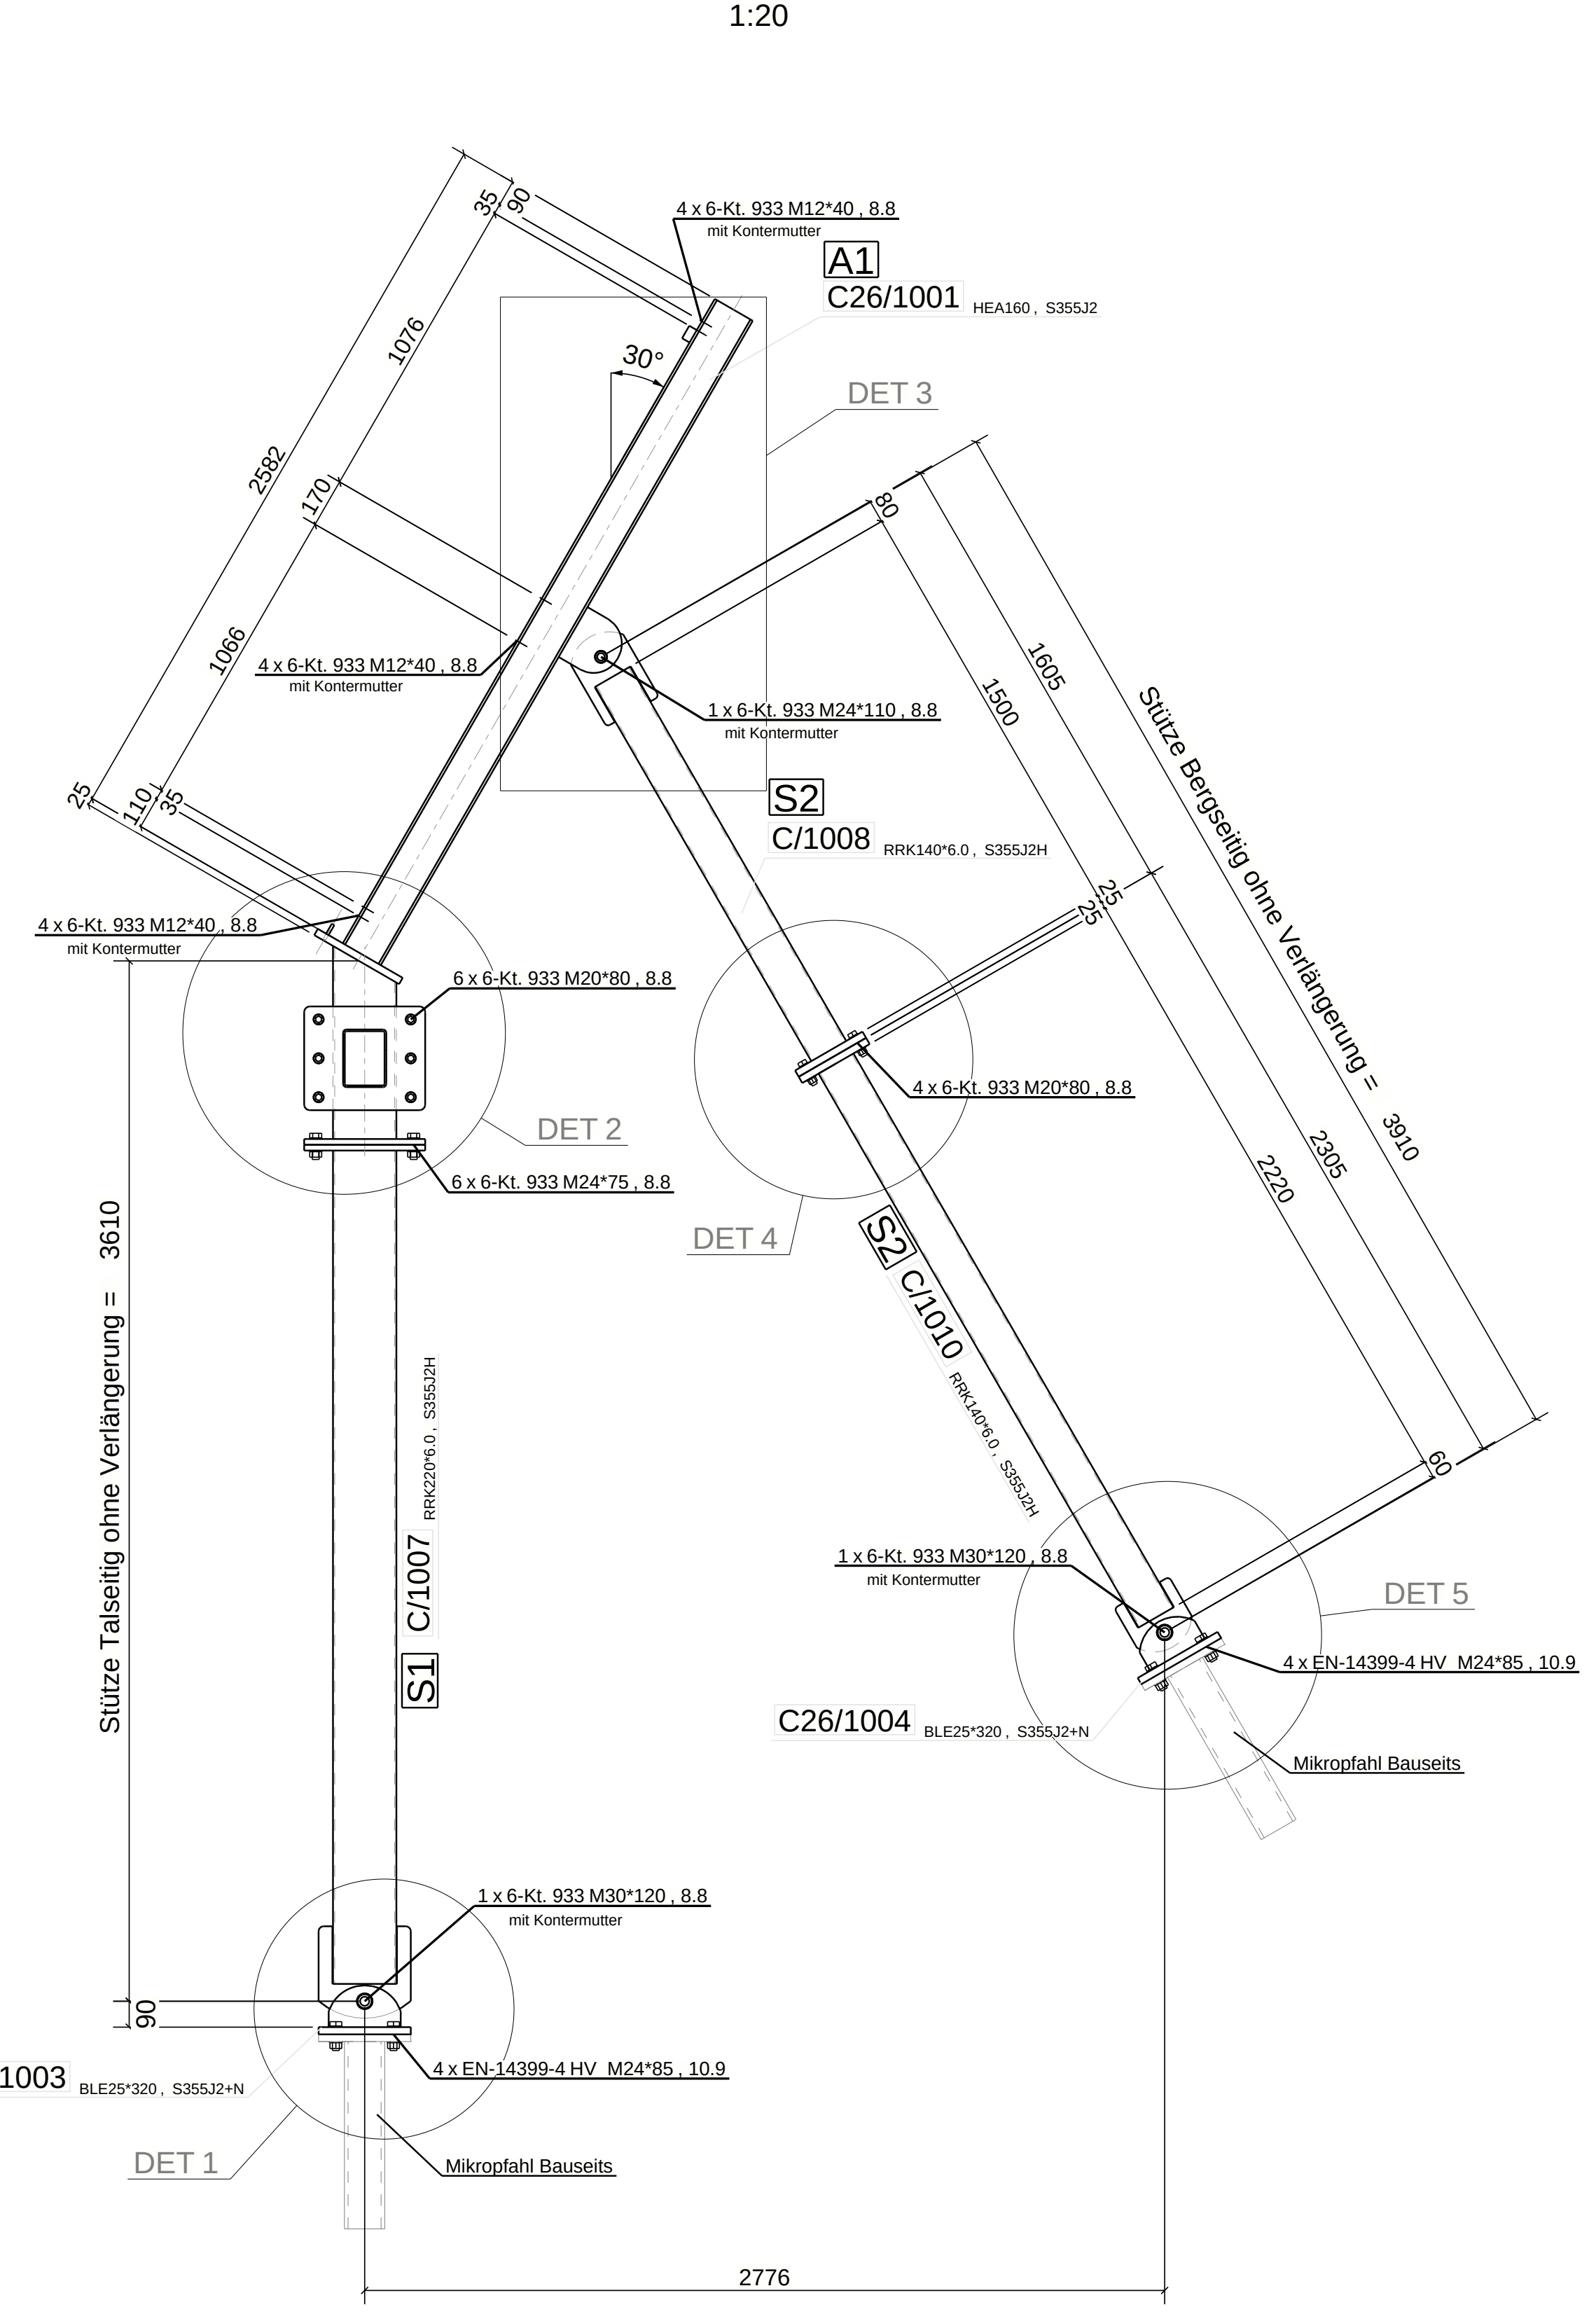
4 x 6-Kt. 933 M12*40 , 8.8
mit Kontermutter
A1
C26/1001 HEA160 , S355J2
30°
DET 3
2582
1076
1 x 6-Kt. 933 M24*110 , 8.8
mit Kontermutter
S2
C/1008 RRK140*6.0 , S355J2H
4 x 6-Kt. 933 M12*40 , 8.8
mit Kontermutter
6 x 6-Kt. 933 M20*80 , 8.8
6 x 6-Kt. 933 M24*75 , 8.8
DET 2
DET 4
4 x 6-Kt. 933 M20*80 , 8.8
Stütze Bergseitig ohne Verlängerung = 3910
1605
1500
2305
2220
S2 C/1010 RRK140*6.0 , S355J2H
Stütze Talseitig ohne Verlängerung = 3610
S1 C/1007 RRK220*6.0 , S355J2H
1 x 6-Kt. 933 M30*120 , 8.8
mit Kontermutter
C26/1004 BLE25*320 , S355J2+N
4 x EN-14399-4 HV M24*85 , 10.9
Mikropfahl Bauseits
DET 5
1 x 6-Kt. 933 M30*120 , 8.8
mit Kontermutter
C26/1003 BLE25*320 , S355J2+N
4 x EN-14399-4 HV M24*85 , 10.9
DET 1
Mikropfahl Bauseits
2776

## Ansicht: Primärkonstruktion Typ C - 2026
1:20

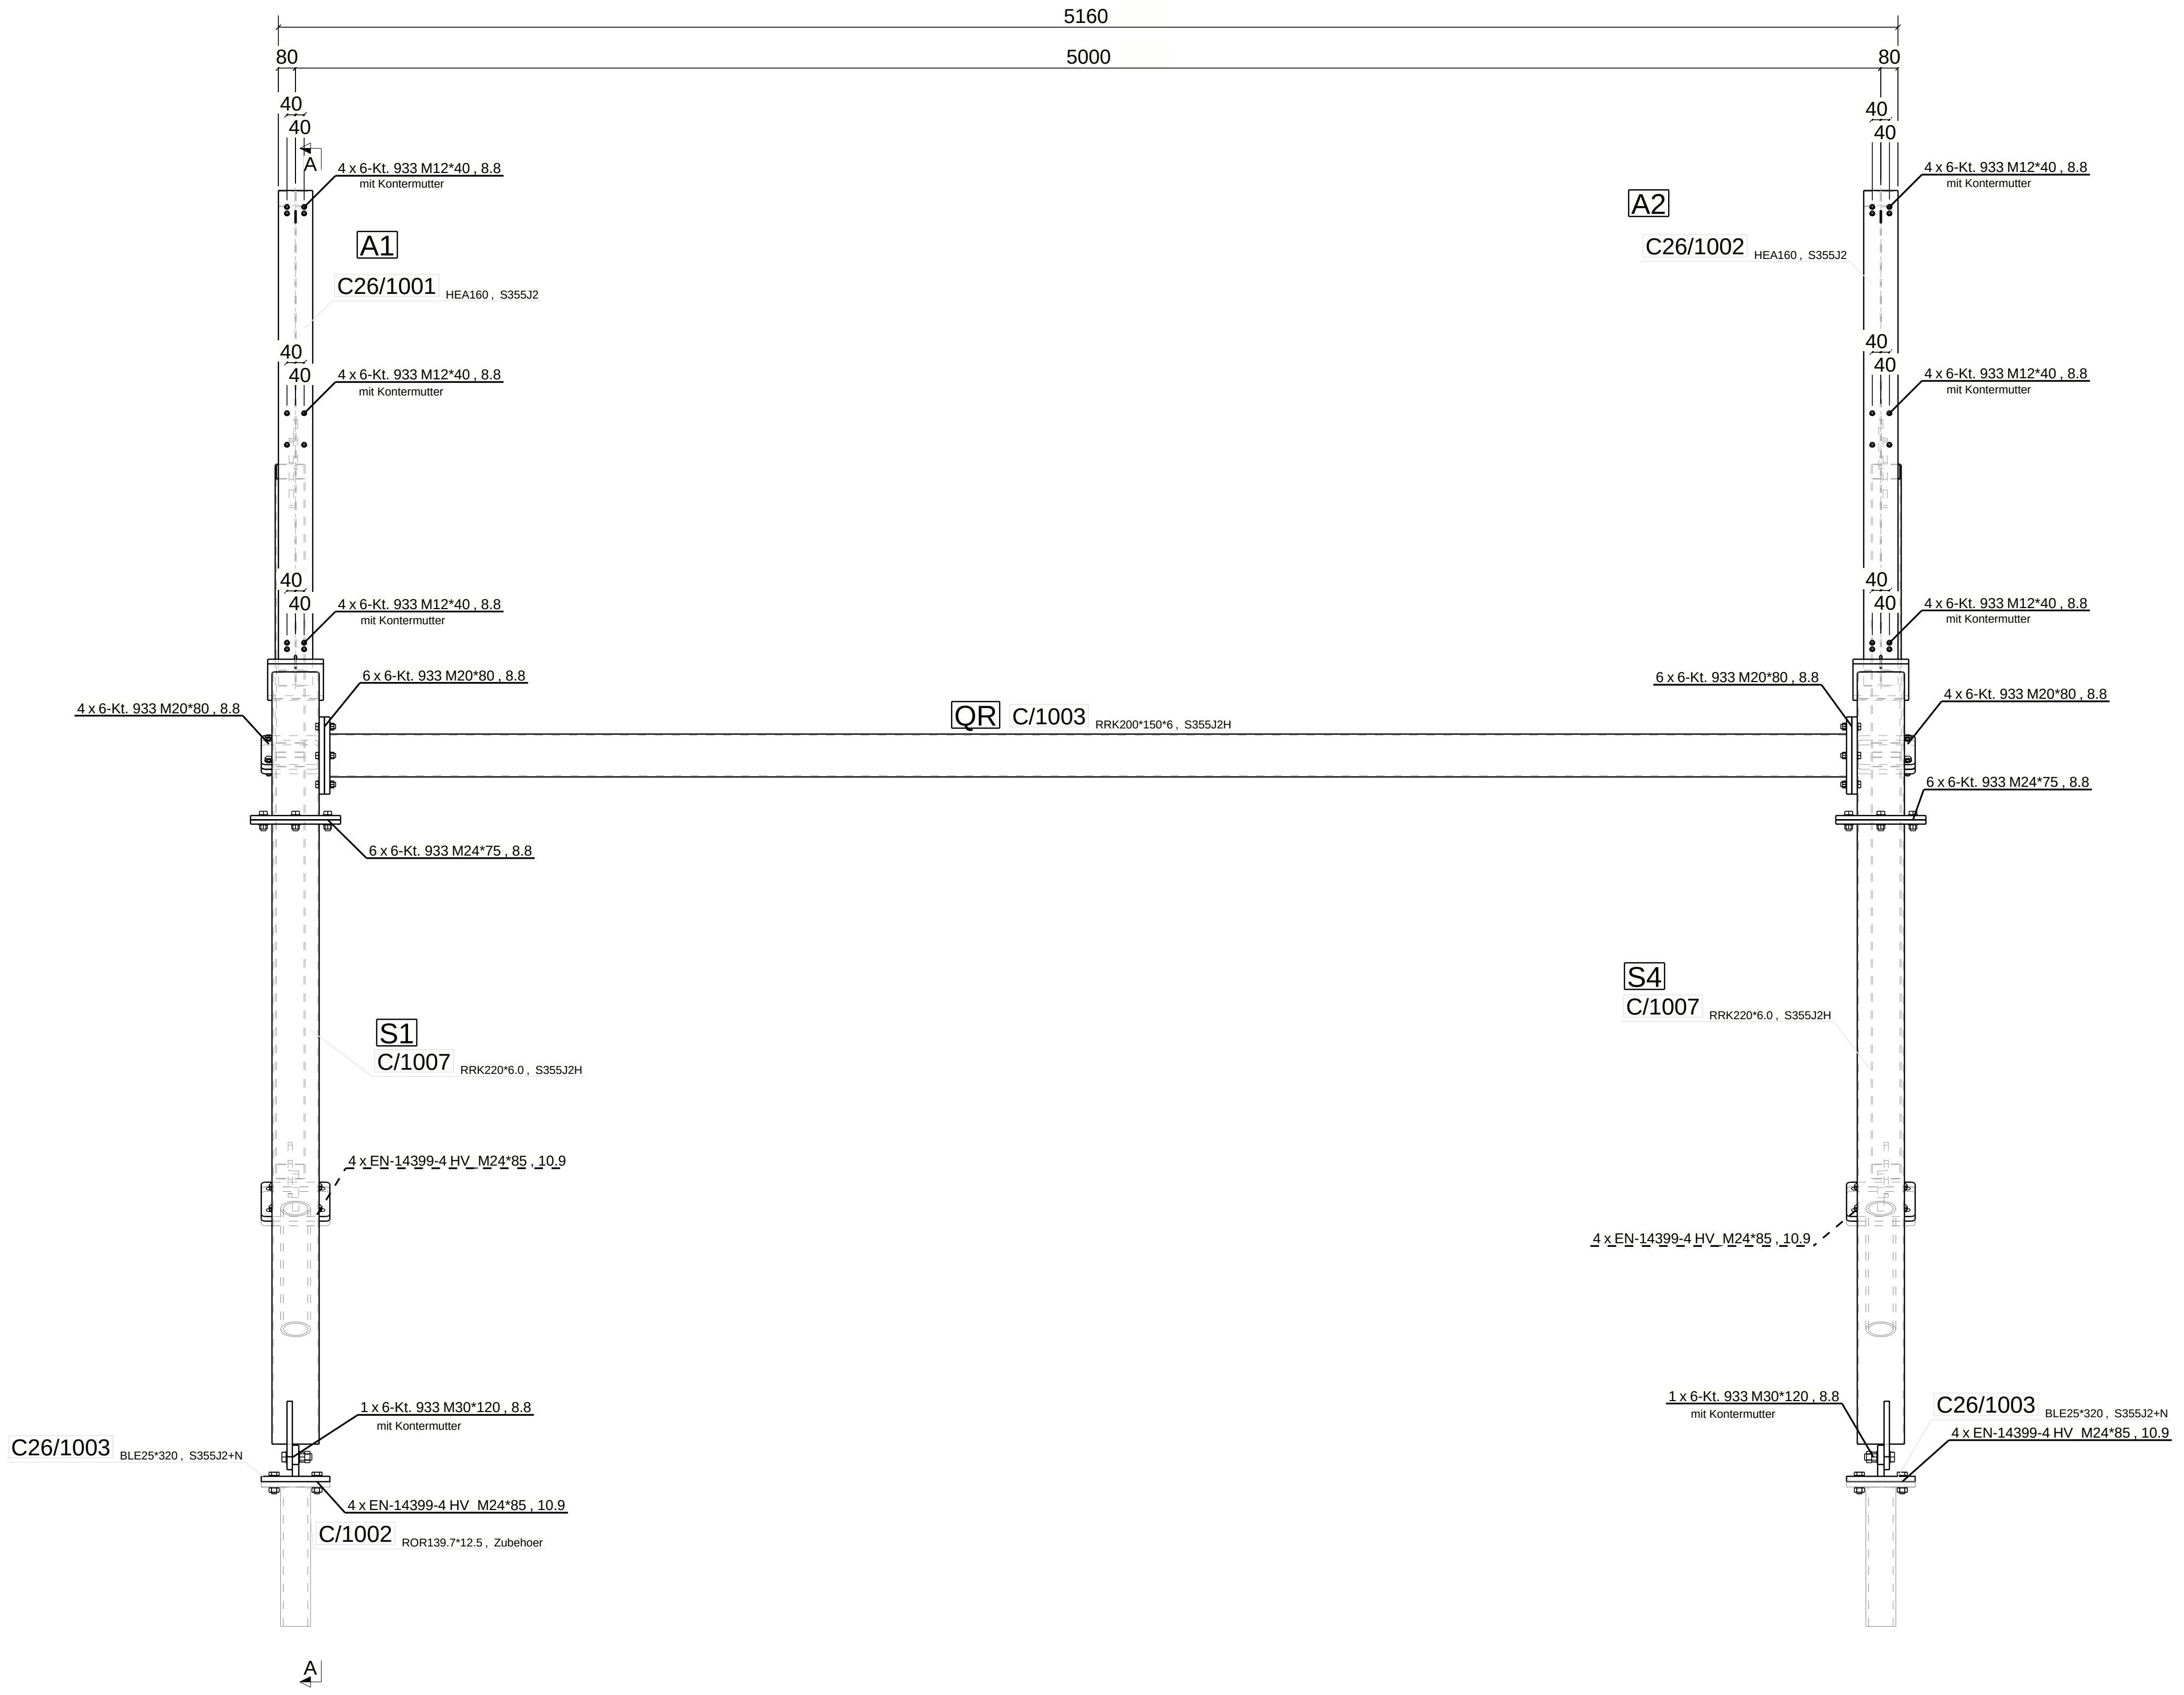
5160
80
5000
80
4 x 6-Kt. 933 M12*40 , 8.8
mit Kontermutter
A1
C26/1001 HEA160 , S355J2
A2
C26/1002 HEA160 , S355J2
4 x 6-Kt. 933 M20*80 , 8.8
6 x 6-Kt. 933 M20*80 , 8.8
QR C/1003 RRK200*150*6 , S355J2H
6 x 6-Kt. 933 M24*75 , 8.8
S1
C/1007 RRK220*6.0 , S355J2H
S4
C/1007 RRK220*6.0 , S355J2H
4 x EN-14399-4 HV M24*85 , 10.9
1 x 6-Kt. 933 M30*120 , 8.8
mit Kontermutter
C26/1003 BLE25*320 , S355J2+N
4 x EN-14399-4 HV M24*85 , 10.9
C/1002 ROR139.7*12.5 , Zubehoer
A

## Isometrie Primärkonstruktion Typ C - 2026

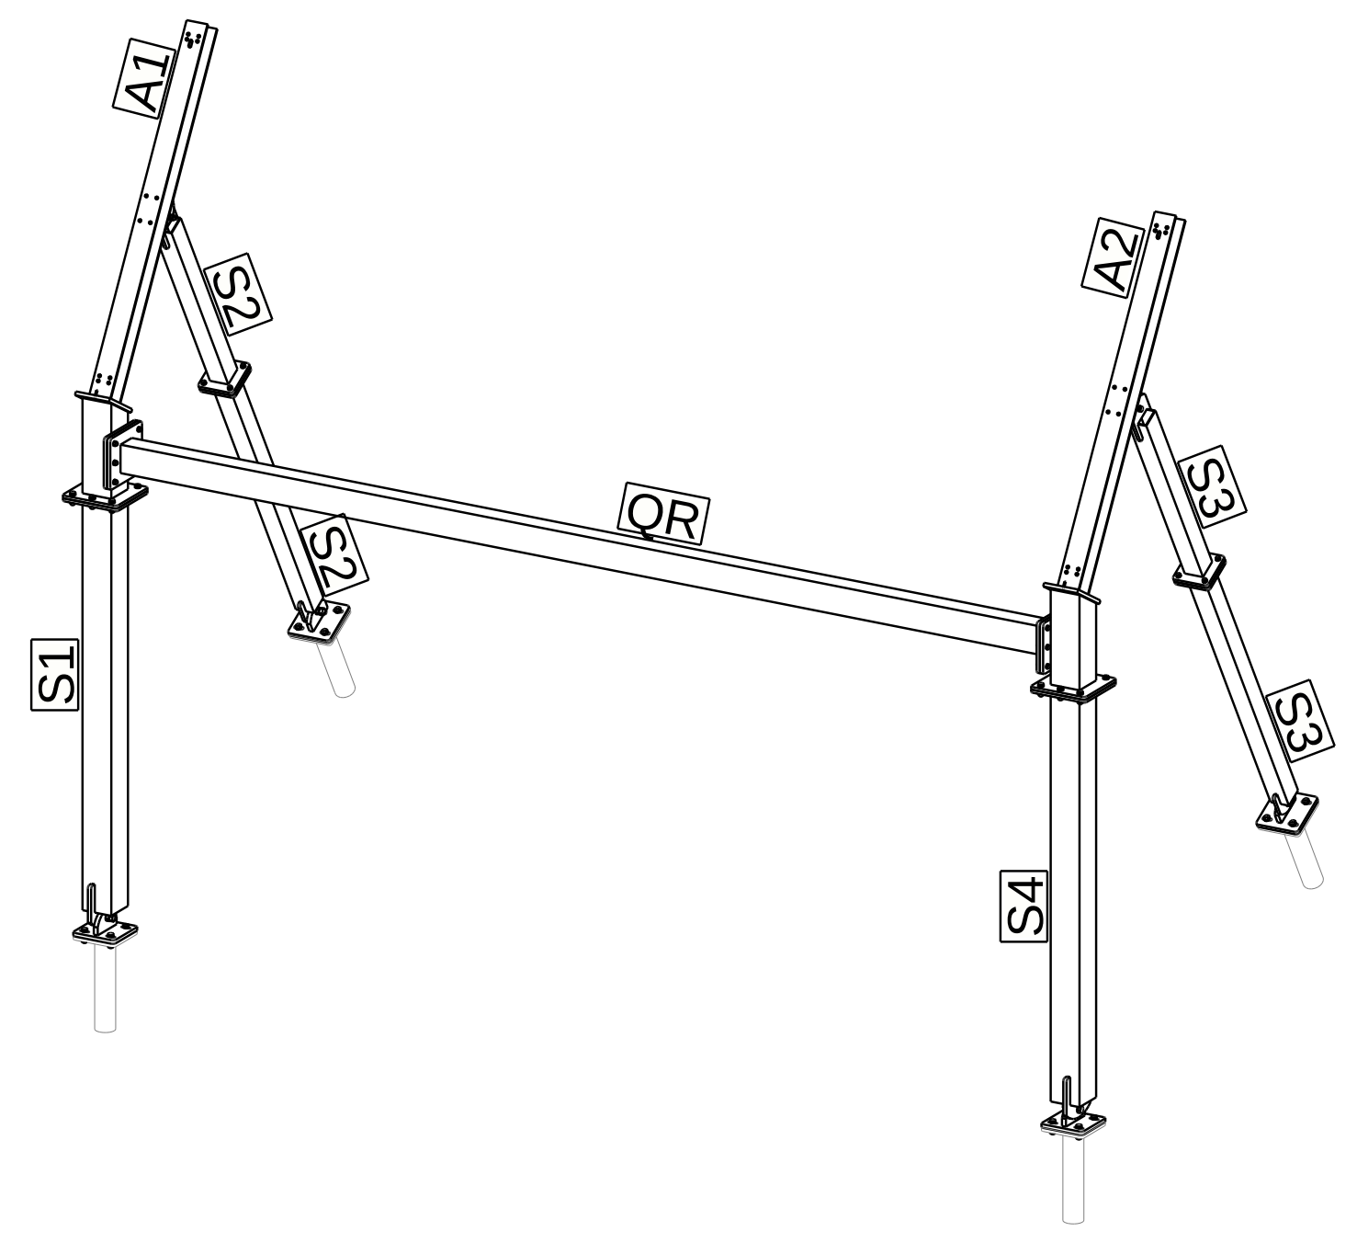

## DETAIL 2 : talseitige Stütze (S1/S4) - Mst: 1:10

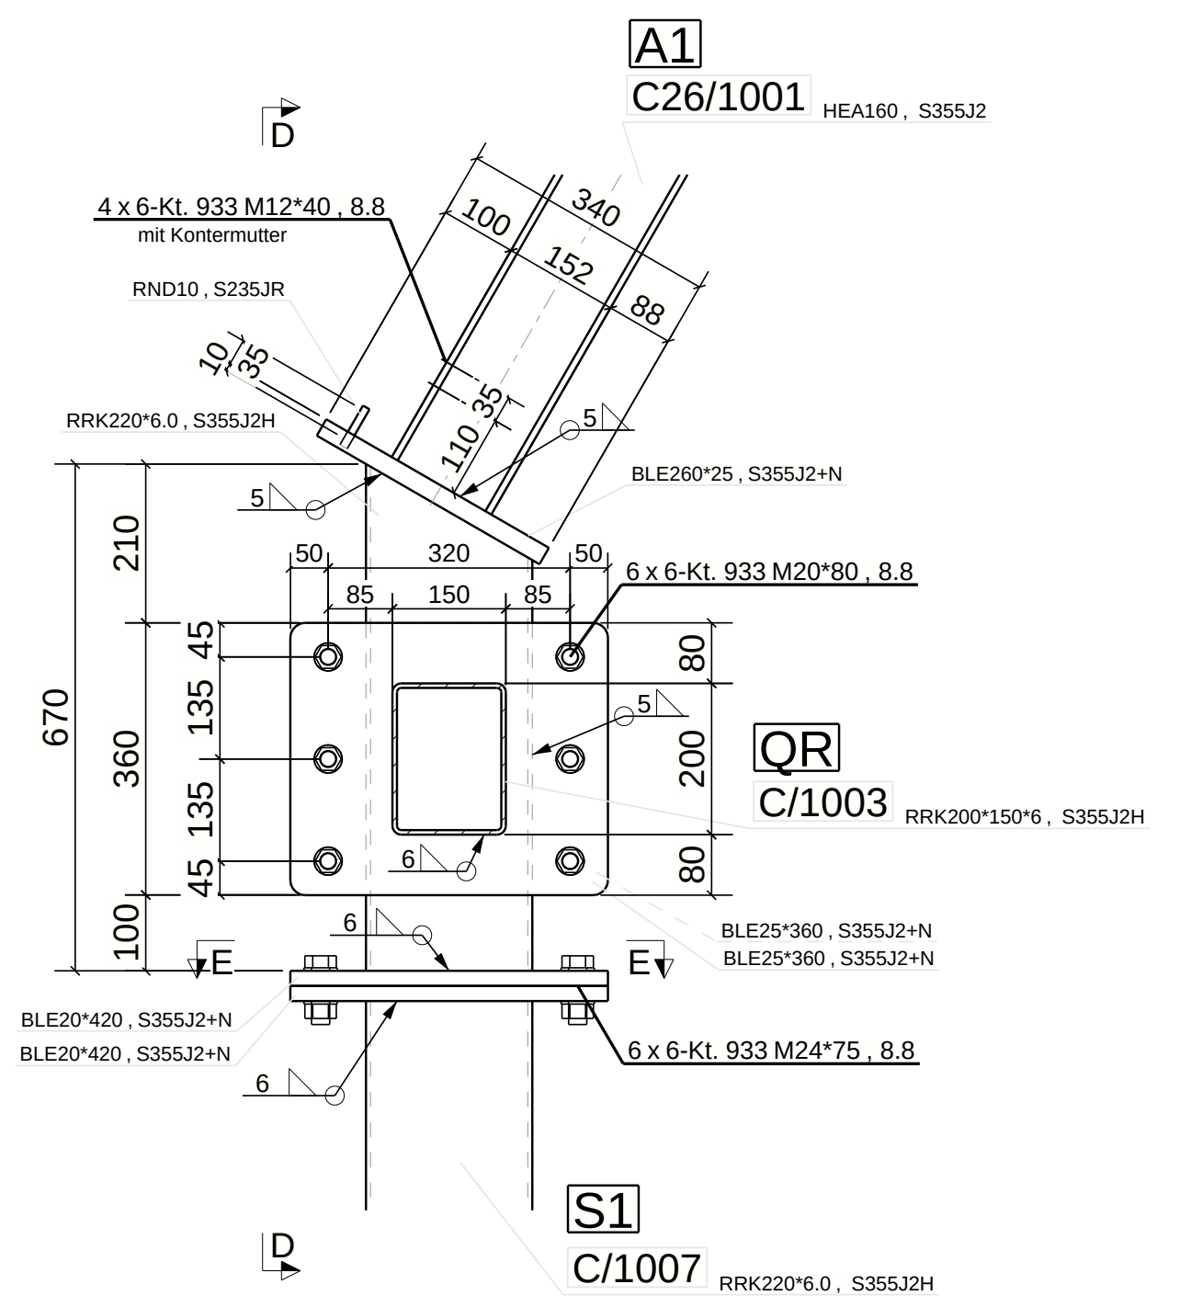

## DETAIL 2, Schnitt D - D : talseitige Stütze (S1/S4)
1:10

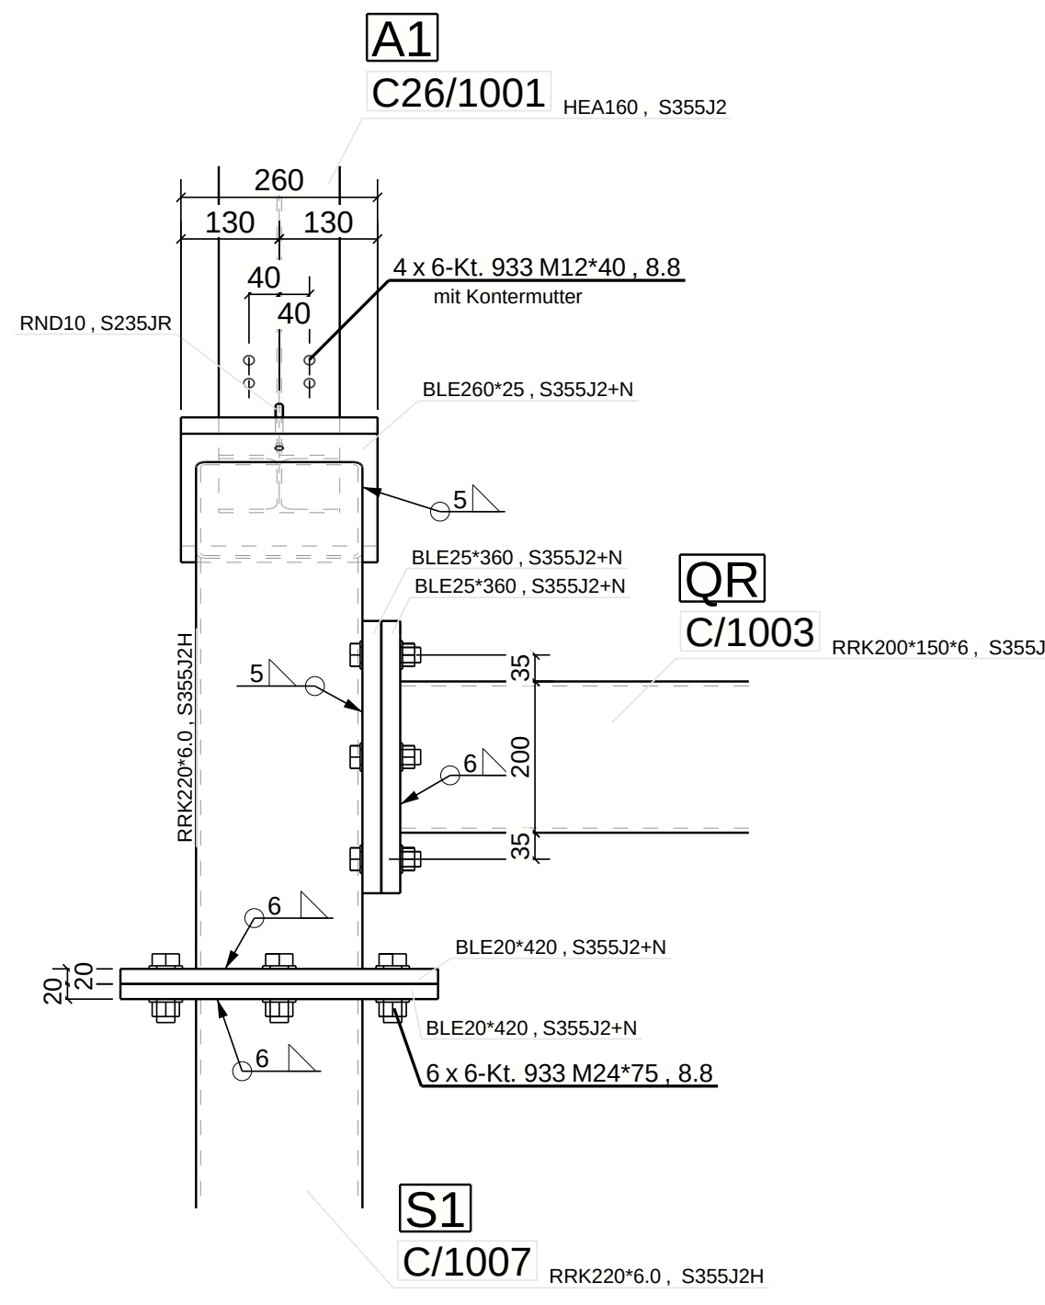

## DETAIL 2, Schnitt E - E : talseitige Stütze (S1/S4)
1:10

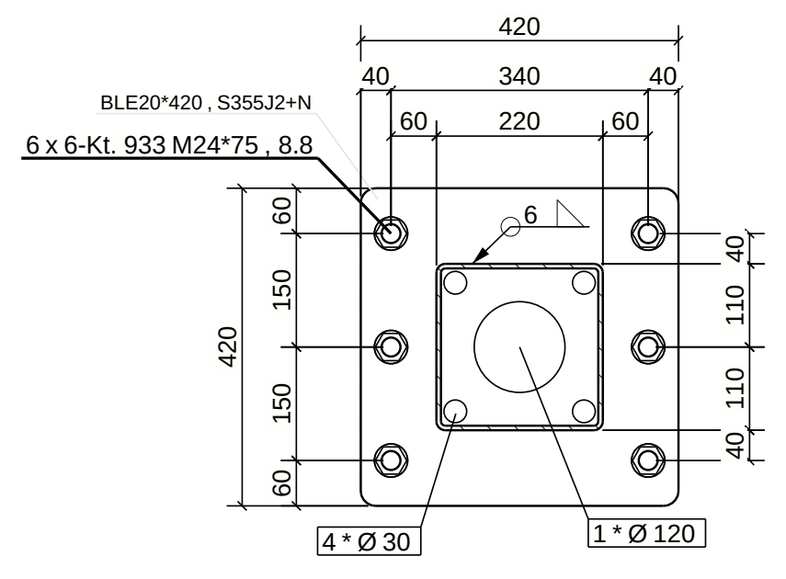

## DETAIL 4 : bergseitige Stütze (S2/S3) - Mst: 1:10

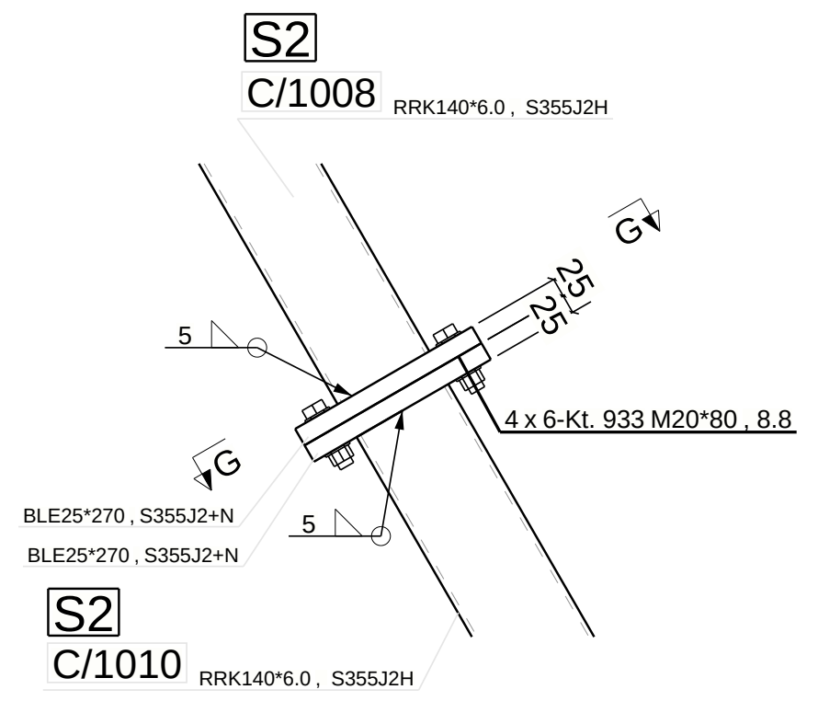
S2
C/1008 RRK140*6.0 , S355J2H
G
6 x 6-Kt. 933 M20*80 , 8.8
BLE25*270 , S355J2+N
BLE25*270 , S355J2+N
S2
C/1010 RRK140*6.0 , S355J2H

## DETAIL 4, Schnitt G - G : bergseitige Stütze (S2/S3)
1:10

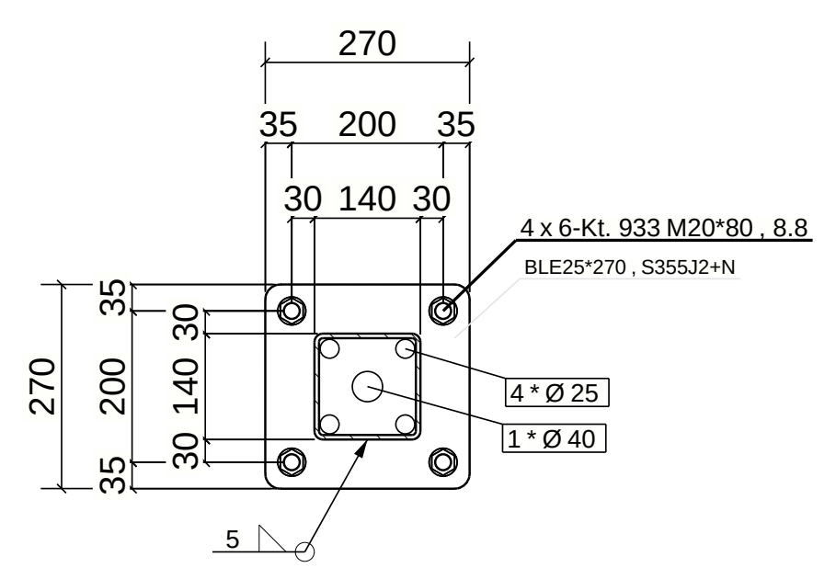

## Grundriss: Primärkonstruktion Typ C- 2026
1:20

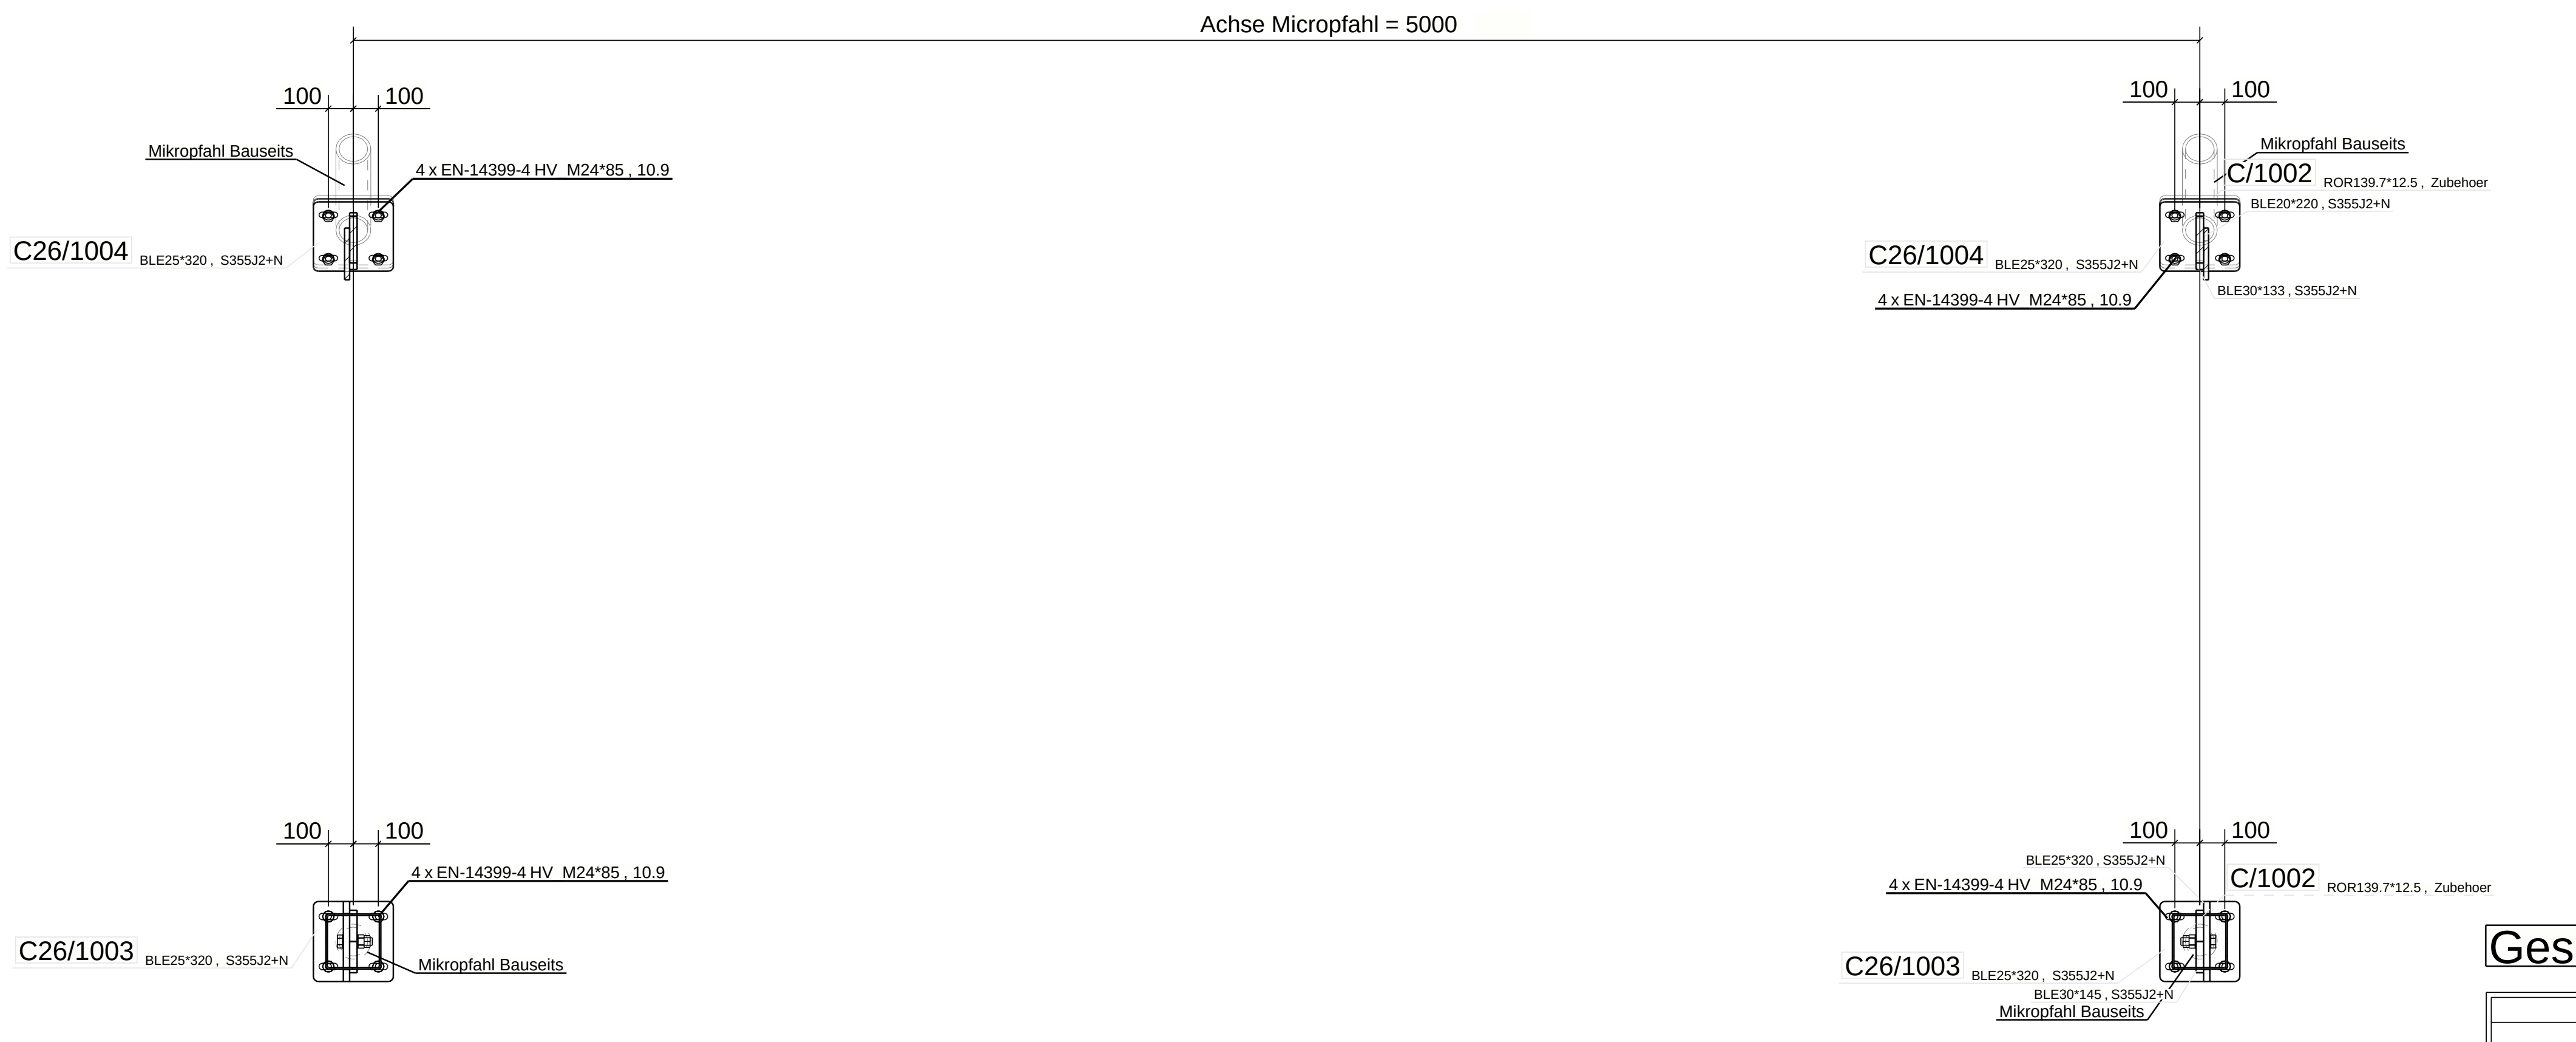

**Tabelle 18: Vorspannkräfte und Anziehdrehmomente für metrische Schrauben der Festigkeitsklassen 3.6 bis 12.9: ISO-Regelgewinde**

**Tableau 18: Forces de tension et couples de serrage pour vis métriques des classes de résistance 3.6 à 12.9: filetage ISO standard**

| Schrauben-durchm. Dimension de vis | Reibungs-zahl Coeff. De frottem. µges. | Vorspannkraft $F_M$ max. (kN) / Force de tension $F_M$ max. (kN) Festigkeitsklasse nach ISO 898 Classe de résistance selon ISO 898 | | | | | | | Anziehdrehmoment $M_A$ max. (Nm) / Couple de serrage $M_A$ max. (Nm) Festigkeitsklasse nach ISO 898 Classe de résistance selon ISO 898 | | | | | | | Umrechnungs-faktor X |
|---|---|---|---|---|---|---|---|---|---|---|---|---|---|---|---|---|
| | | 3.6 | 4.6 | 5.6 (4.8) | 6.8 | 8.8 | 10.9 | 12.9 | 3.6 | 4.6 | 5.6 (4.8) | 6.8 | 8.8 | 10.9 | 12.9 | |
| M 3 | 0,10 | 0.72 | 0.96 | 0.12 | 0.19 | 0.26 | 0.36 | 0.43 | 0.32 | 0.42 | 0.53 | 0.84 | 1.12 | 1.58 | 1.90 | 0.44 |
| | 0,12 | 0.70 | 0.94 | 0.12 | 0.18 | 0.25 | 0.35 | 0.42 | 0.36 | 0.48 | 0.60 | 0.95 | 1.27 | 1.79 | 2.14 | 0.51 |
| | 0,14 | 0.68 | 0.91 | 0.11 | 0.18 | 0.24 | 0.34 | 0.41 | 0.40 | 0.53 | 0.66 | 1.05 | 1.41 | 1.98 | 2.37 | 0.58 |
| M 4 | 0,10 | 1.26 | 1.68 | 2.10 | 3.36 | 4.50 | 6.70 | 7.80 | 0.73 | 0.97 | 1.21 | 1.94 | 2.60 | 3.90 | 4.50 | 0.58 |
| | 0,12 | 1.22 | 1.63 | 2.04 | 3.26 | 4.40 | 6.50 | 7.60 | 0.82 | 1.09 | 1.37 | 2.19 | 3.00 | 4.60 | 5.10 | 0.67 |
| | 0,14 | 1.19 | 1.58 | 1.98 | 3.17 | 4.30 | 6.30 | 7.40 | 0.91 | 1.21 | 1.51 | 2.42 | 3.30 | 4.80 | 5.60 | 0.76 |
| M 5 | 0,10 | 2.06 | 2.74 | 3.43 | 5.48 | 7.40 | 10.80 | 12.70 | 1.40 | 1.90 | 2.40 | 3.80 | 5.20 | 7.60 | 8.90 | 0.70 |
| | 0,12 | 2.00 | 2.67 | 3.33 | 5.33 | 7.20 | 10.60 | 12.40 | 1.60 | 2.20 | 2.70 | 4.30 | 5.90 | 8.60 | 10.00 | 0.81 |
| | 0,14 | 1.94 | 2.59 | 3.23 | 5.18 | 7.00 | 10.30 | 12.00 | 1.80 | 2.40 | 3.00 | 4.80 | 6.50 | 9.50 | 11.20 | 0.93 |
| M 6 | 0,10 | 2.90 | 3.87 | 4.84 | 7.74 | 10.40 | 15.30 | 17.90 | 2.50 | 3.30 | 4.10 | 6.60 | 9.00 | 13.20 | 15.40 | 0.86 |
| | 0,12 | 2.82 | 3.76 | 4.71 | 7.53 | 10.20 | 14.90 | 17.50 | 2.80 | 3.70 | 4.70 | 7.50 | 10.10 | 14.90 | 17.40 | 0.99 |
| | 0,14 | 2.74 | 3.65 | 4.57 | 7.31 | 9.90 | 14.50 | 17.00 | 3.10 | 4.10 | 5.20 | 8.30 | 11.30 | 16.50 | 19.30 | 1.14 |
| M 8 | 0,10 | 5.30 | 7.10 | 8.80 | 14.20 | 19.10 | 28.00 | 32.80 | 6.00 | 8.00 | 10.00 | 16.10 | 21.60 | 31.80 | 37.20 | 1.13 |
| | 0,12 | 5.15 | 6.90 | 8.60 | 13.80 | 18.60 | 27.30 | 32.00 | 6.80 | 9.10 | 11.30 | 18.20 | 24.60 | 36.10 | 42.20 | 1.32 |
| | 0,14 | 5.00 | 6.70 | 8.30 | 13.40 | 18.10 | 26.60 | 31.10 | 7.50 | 10.10 | 12.60 | 20.10 | 27.30 | 40.10 | 46.90 | 1.51 |
| M 10 | 0,10 | 8.40 | 11.30 | 14.10 | 22.50 | 30.30 | 44.50 | 52.10 | 12.00 | 16.10 | 20.10 | 32.30 | 43.00 | 63.00 | 73.00 | 1.42 |
| | 0,12 | 8.20 | 11.00 | 13.70 | 21.90 | 29.60 | 43.40 | 50.80 | 13.70 | 18.30 | 22.90 | 36.50 | 48.00 | 71.00 | 83.00 | 1.65 |
| | 0,14 | 8.00 | 10.70 | 13.30 | 21.30 | 28.80 | 42.20 | 49.40 | 15.20 | 20.30 | 25.30 | 40.60 | 54.00 | 79.00 | 93.00 | 1.89 |
| M 12 | 0,10 | 12.30 | 16.40 | 20.50 | 32.80 | 44.10 | 64.80 | 75.90 | 20.00 | 27.00 | 34.00 | 55.00 | 73.00 | 108.00 | 126.00 | 1.65 |
| | 0,12 | 12.00 | 16.00 | 20.00 | 32.00 | 43.00 | 63.20 | 74.00 | 23.00 | 31.00 | 39.00 | 62.00 | 84.00 | 123.00 | 144.00 | 1.94 |
| | 0,14 | 11.60 | 15.50 | 19.40 | 31.10 | 41.90 | 61.50 | 72.00 | 26.00 | 34.00 | 43.00 | 69.00 | 93.00 | 137.00 | 160.00 | 2.22 |
| M 14 | 0,10 | 16.90 | 22.50 | 28.20 | 45.10 | 60.60 | 88.90 | 104.10 | 33.00 | 44.00 | 55.00 | 88.00 | 117.00 | 172.00 | 201.00 | 1.94 |
| | 0,12 | 16.50 | 21.90 | 27.40 | 43.90 | 59.10 | 86.70 | 101.50 | 37.00 | 50.00 | 62.00 | 100.00 | 133.00 | 195.00 | 229.00 | 2.26 |
| | 0,14 | 16.00 | 21.30 | 26.70 | 42.70 | 57.50 | 84.40 | 98.90 | 41.00 | 55.00 | 69.00 | 111.00 | 148.00 | 218.00 | 255.00 | 2.58 |
| M 16 | 0,10 | 23.20 | 30.90 | 38.60 | 61.80 | 82.90 | 121.70 | 142.40 | 50.00 | 67.00 | 84.00 | 134.00 | 180.00 | 264.00 | 309.00 | 2.17 |
| | 0,12 | 22.60 | 30.10 | 37.60 | 60.20 | 80.90 | 118.80 | 139.00 | 57.00 | 76.00 | 96.00 | 153.00 | 206.00 | 302.00 | 354.00 | 2.54 |
| | 0,14 | 22.00 | 29.30 | 36.60 | 58.60 | 78.80 | 115.70 | 135.40 | 64.00 | 85.00 | 107.00 | 171.00 | 230.00 | 338.00 | 395.00 | 2.92 |
| M 18 | 0,10 | 28.20 | 37.70 | 47.10 | 75.30 | 104.00 | 149.00 | 174.00 | 70.00 | 93.00 | 117.00 | 187.00 | 259.00 | 369.00 | 432.00 | 2.48 |
| | 0,12 | 27.50 | 36.70 | 45.80 | 73.40 | 102.00 | 145.00 | 170.00 | 80.00 | 106.00 | 133.00 | 212.00 | 295.00 | 421.00 | 492.00 | 2.90 |
| | 0,14 | 26.70 | 35.70 | 44.60 | 71.30 | 99.00 | 141.00 | 165.00 | 89.00 | 118.00 | 148.00 | 236.00 | 329.00 | 469.00 | 549.00 | 3.32 |
| M 20 | 0,10 | 36.20 | 48.30 | 60.30 | 96.50 | 134.00 | 190.00 | 223.00 | 98.00 | 131.00 | 164.00 | 262.00 | 363.00 | 517.00 | 605.00 | 2.71 |
| | 0,12 | 35.30 | 47.00 | 58.80 | 94.10 | 130.00 | 186.00 | 217.00 | 112.00 | 150.00 | 187.00 | 300.00 | 415.00 | 592.00 | 692.00 | 3.18 |
| | 0,14 | 34.30 | 45.80 | 57.20 | 91.60 | 127.00 | 181.00 | 212.00 | 125.00 | 167.00 | 209.00 | 334.00 | 464.00 | 661.00 | 773.00 | 3.65 |
| M 22 | 0,10 | 45.10 | 60.10 | 75.20 | 120.30 | 166.00 | 237.00 | 277.00 | 132.00 | 176.00 | 220.00 | 353.00 | 495.00 | 704.00 | 824.00 | 2.95 |
| | 0,12 | 44.00 | 58.70 | 73.40 | 117.40 | 162.00 | 231.00 | 271.00 | 151.00 | 202.00 | 252.00 | 403.00 | 567.00 | 807.00 | 945.00 | 3.46 |
| | 0,14 | 42.90 | 57.10 | 71.40 | 114.30 | 158.00 | 225.00 | 264.00 | 169.00 | 225.00 | 282.00 | 451.00 | 634.00 | 904.00 | 1057.00 | 3.97 |
| M 24 | 0,10 | 52.10 | 69.50 | 86.90 | 139.00 | 192.00 | 274.00 | 320.00 | 169.00 | 226.00 | 282.00 | 451.00 | 625.00 | 890.00 | 1041.00 | 3.25 |
| | 0,12 | 50.80 | 67.70 | 84.70 | 135.50 | 188.00 | 267.00 | 313.00 | 193.00 | 257.00 | 322.00 | 515.00 | 714.00 | 1017.00 | 1190.00 | 3.80 |
| | 0,14 | 49.40 | 65.90 | 82.40 | 131.80 | 183.00 | 260.00 | 305.00 | 215.00 | 287.00 | 359.00 | 574.00 | 798.00 | 1136.00 | 1329.00 | 4.36 |
| M 27 | 0,10 | 68.40 | 91.20 | 114.00 | 182.40 | 252.00 | 359.00 | 420.00 | 248.00 | 331.00 | 414.00 | 662.00 | 915.00 | 1304.00 | 1526.00 | 3.63 |
| | 0,12 | 66.70 | 89.00 | 111.20 | 178.00 | 246.00 | 351.00 | 410.00 | 284.00 | 379.00 | 474.00 | 759.00 | 1050.00 | 1496.00 | 1750.00 | 4.26 |
| | 0,14 | 65.00 | 86.70 | 108.30 | 173.30 | 240.00 | 342.00 | 400.00 | 318.00 | 424.00 | 530.00 | 848.00 | 1176.00 | 1674.00 | 1959.00 | 4.89 |
| M 30 | 0,10 | 83.20 | 111.00 | 138.70 | 222.00 | 307.00 | 437.00 | 511.00 | 338.00 | 450.00 | 563.00 | 901.00 | 1246.00 | 1775.00 | 2077.00 | 4.06 |
| | 0,12 | 81.20 | 108.30 | 135.30 | 216.50 | 300.00 | 427.00 | 499.00 | 386.00 | 515.00 | 644.00 | 1031.00 | 1420.00 | 2033.00 | 2380.00 | 4.76 |
| | 0,14 | 79.00 | 105.30 | 131.70 | 210.80 | 292.00 | 416.00 | 487.00 | 431.00 | 575.00 | 719.00 | 1151.00 | 1597.00 | 2274.00 | 2662.00 | 5.46 |
| M 33 | 0,10 | 103.50 | 138.00 | 172.50 | 276.00 | 381.00 | 543.00 | 635.00 | 456.00 | 608.00 | 760.00 | 1216.00 | 1679.00 | 2392.00 | 2799.00 | 4.41 |
| | 0,12 | 101.00 | 134.70 | 168.40 | 269.40 | 373.00 | 531.00 | 621.00 | 523.00 | 697.00 | 871.00 | 1395.00 | 1928.00 | 2747.00 | 3214.00 | 5.17 |
| | 0,14 | 98.40 | 131.20 | 164.00 | 262.50 | 363.00 | 517.00 | 605.00 | 585.00 | 780.00 | 975.00 | 1560.00 | 2161.00 | 3078.00 | 3601.00 | 5.95 |
| M 36 | 0,10 | 121.60 | 162.10 | 202.70 | 324.30 | 448.00 | 638.00 | 747.00 | 587.00 | 783.00 | 979.00 | 1566.00 | 2164.00 | 3082.00 | 3607.00 | 4.83 |
| | 0,12 | 118.70 | 158.20 | 197.80 | 316.40 | 438.00 | 623.00 | 729.00 | 672.00 | 897.00 | 1121.00 | 1793.00 | 2482.00 | 3535.00 | 4136.00 | 5.67 |
| | 0,14 | 115.60 | 154.10 | 192.60 | 308.10 | 427.00 | 608.00 | 711.00 | 752.00 | 1002.00 | 1253.00 | 2005.00 | 2778.00 | 3957.00 | 4631.00 | 6.51 |
| M 39 | 0,10 | 145.90 | 194.50 | 243.10 | 389.00 | 537.00 | 765.00 | 895.00 | 758.00 | 1011.00 | 1264.00 | 2022.00 | 2791.00 | 3975.00 | 4652.00 | 5.20 |
| | 0,12 | 142.40 | 189.90 | 237.40 | 379.80 | 525.00 | 748.00 | 875.00 | 870.00 | 1160.00 | 1450.00 | 2321.00 | 3208.00 | 4569.00 | 5346.00 | 6.11 |
| | 0,14 | 138.80 | 185.00 | 231.30 | 370.00 | 512.00 | 729.00 | 853.00 | 974.00 | 1299.00 | 1624.00 | 2598.00 | 3597.00 | 5123.00 | 5994.00 | 7.02 |

Die in der Tabelle aufgeführten Vorspannkräfte $F_m$ ergeben etwa eine 90%-ige Ausnutzung der Streckgrenze $R_{p0,2}$.

Les forces de tension $F_m$ indiquées dans le tableau permettent d'obtenir une utilisation approximative de 90% de la limite d'élasticité $R_{p0,2}$.

## DETAIL 1: talseitiger Stützenfuss (S1/S4) - Mst: 1:10

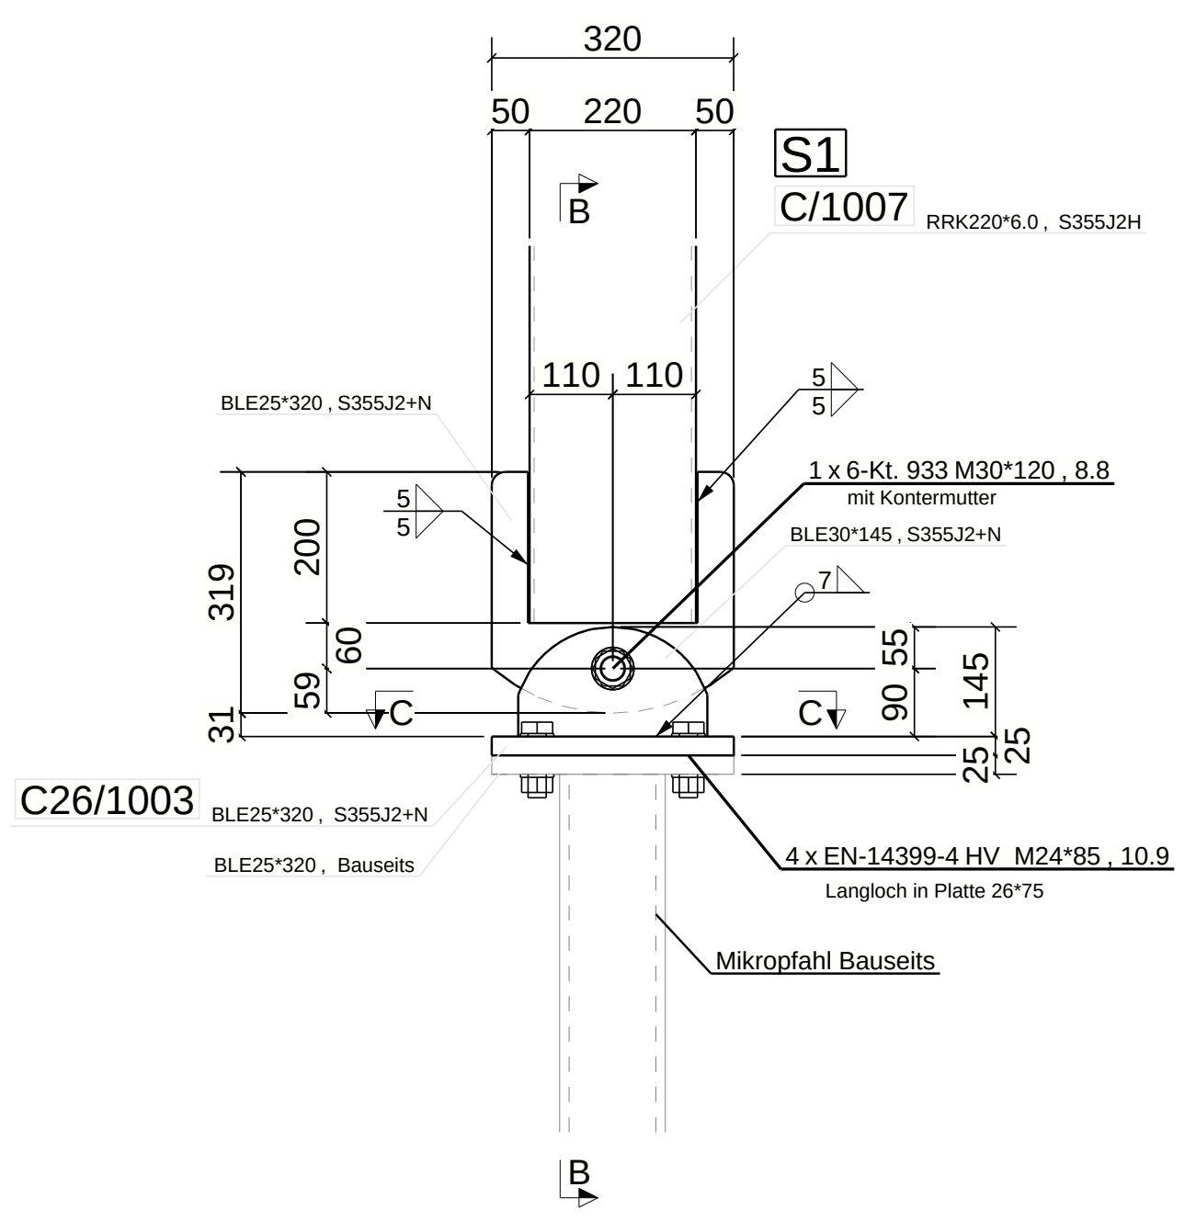

## DETAIL 1, Schnitt B - B : talseitiger Stützenfuss (S1/S4)
1:10

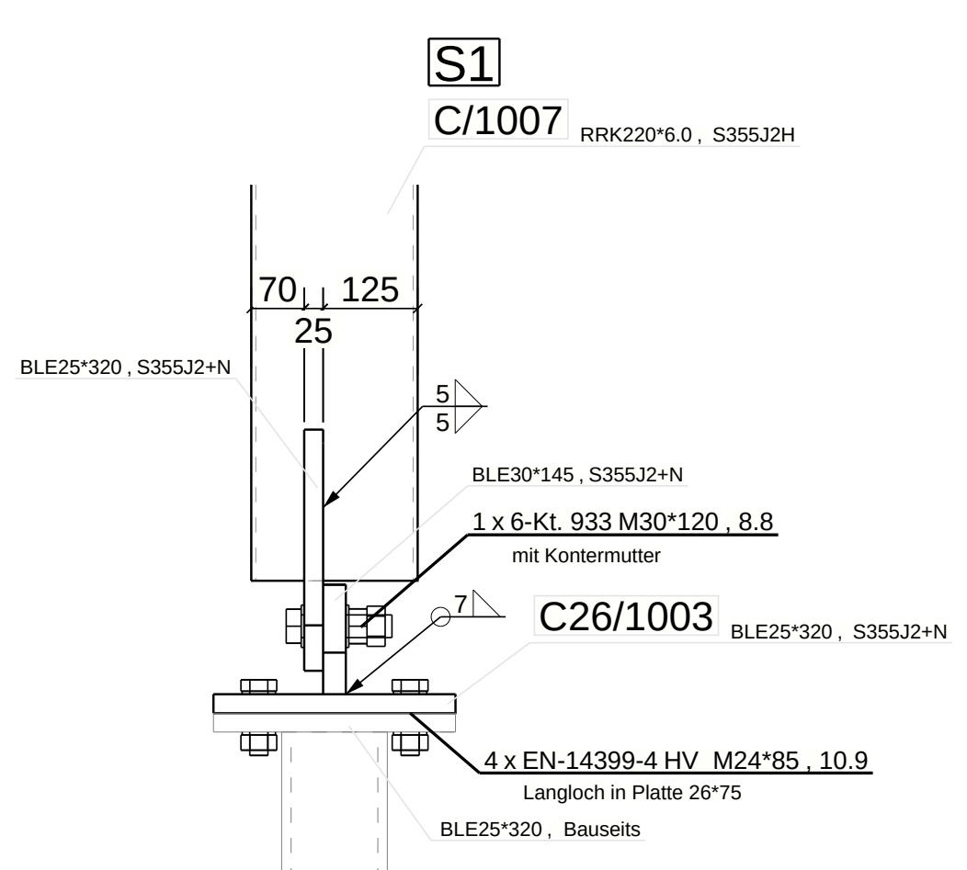
S1
C/1007 RRK220*6.0 , S355J2H
70 125
BLE25*320 , S355J2+N
BLE30*145 , S355J2+N
1 x 6-Kt. 933 M30*120 , 8.8
mit Kontermutter
C26/1003 BLE25*320 , S355J2+N
4 x EN-14399-4 HV M24*85 , 10.9
Langloch in Platte 26*75
BLE25*320 , Bauseits

## DETAIL 5 : bergseitiger Stützenfuss (S2/S3) - Mst: 1:10

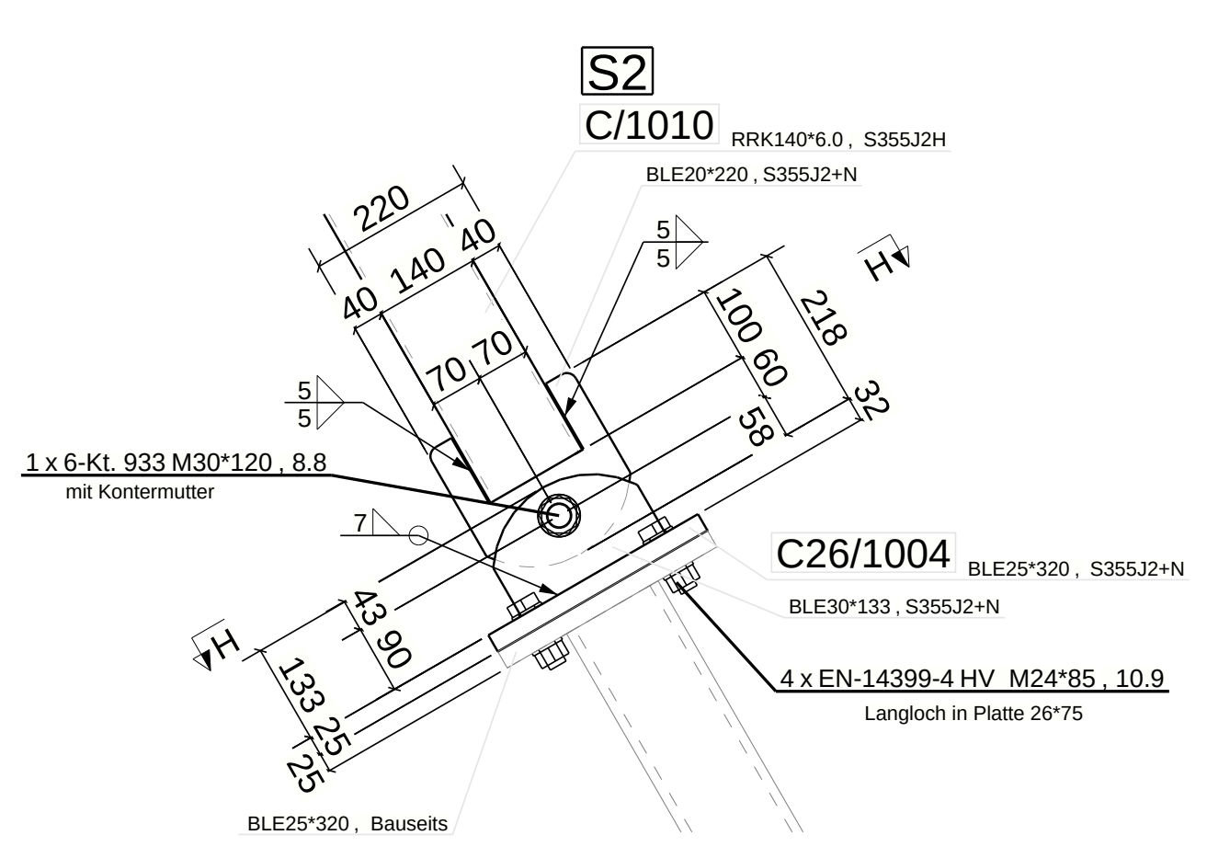
S2
C/1010 RRK140*6.0 , S355J2H
BLE20*220 , S355J2+N
H
1 x 6-Kt. 933 M30*120 , 8.8
mit Kontermutter
C26/1004 BLE25*320 , S355J2+N
BLE30*133 , S355J2+N
4 x EN-14399-4 HV M24*85 , 10.9
Langloch in Platte 26*75
BLE25*320 , Bauseits
H

## DETAIL 1, Schnitt C - C : talseitiger Stützenfuss (S1/S4)
1:10

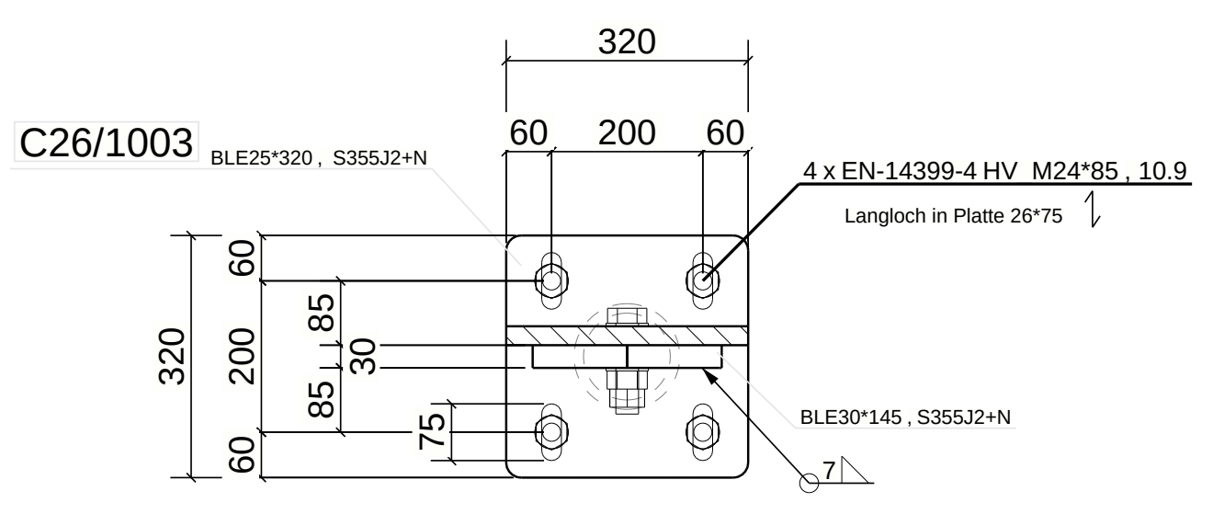
320
60 200 60
C26/1003 BLE25*320 , S355J2+N
4 x EN-14399-4 HV M24*85 , 10.9
Langloch in Platte 26*75
BLE30*145 , S355J2+N

## DETAIL 5, Schnitt H - H 3: bergseitiger Stützenfuss (S2/S3)
1:10

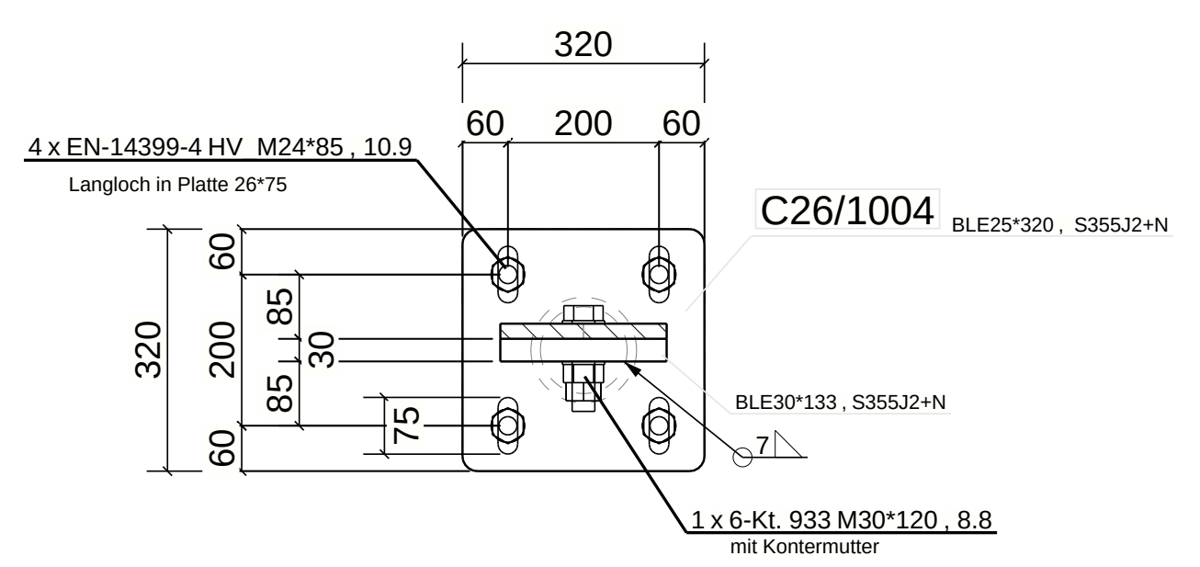
320
60 200 60
4 x EN-14399-4 HV M24*85 , 10.9
Langloch in Platte 26*75
C26/1004 BLE25*320 , S355J2+N
BLE30*133 , S355J2+N
1 x 6-Kt. 933 M30*120 , 8.8
mit Kontermutter

Gesamte Konstruktion ist Roh

| INDEX | DATUM | ÄNDERUNG BENENNUNG | NAME |
|---|---|---|---|
| | | | |

MAUCHLE
Stahlbau

Industriestrasse 9 - CH-6210 Sursee - T +41 41 925 12 51 - info@mauchlestahlbau.ch

| | |
|---|---|
| Auftragsnr. | 24027 |
| Zeichner | P.Koch |
| Interne Kontrolle | |
| ABTEILUNG | UNTERSCHRIFT |
| PL | J. Mäder |
| MAßSTAB | 1:10 1:20 1:50 |
| ANSICHT | |

BAUHERR
Axpo Solutions AG

BAUSTELLE
NalpSolar

BENENNUNG
Primärkonstruktion Typ C
Typ 2026 - für 8er Modultisch
Ansicht, Schnitte & Details

ZEICHNUNGSNUMMER

| PROJEKT | ABTEILUNG | LOS | TIPOLOGIE | FORTLAUFENDE NR° | REVISION |
|---|---|---|---|---|---|
| 24027 | S | 0 | M | 015 | |

DER INHALT DIESER ZEICHNUNG IST UNSER GEISTIGES EIGENTUM UND DARF NICHT OHNE UNSERE GENEHMIGUNG VERVIELFÄLTIGT ODER AN DRITTE PERSONEN WEITERGEGEBEN WERDEN.