




DETAIL 3 : Auflageträger (A1) - Mst: 1:10

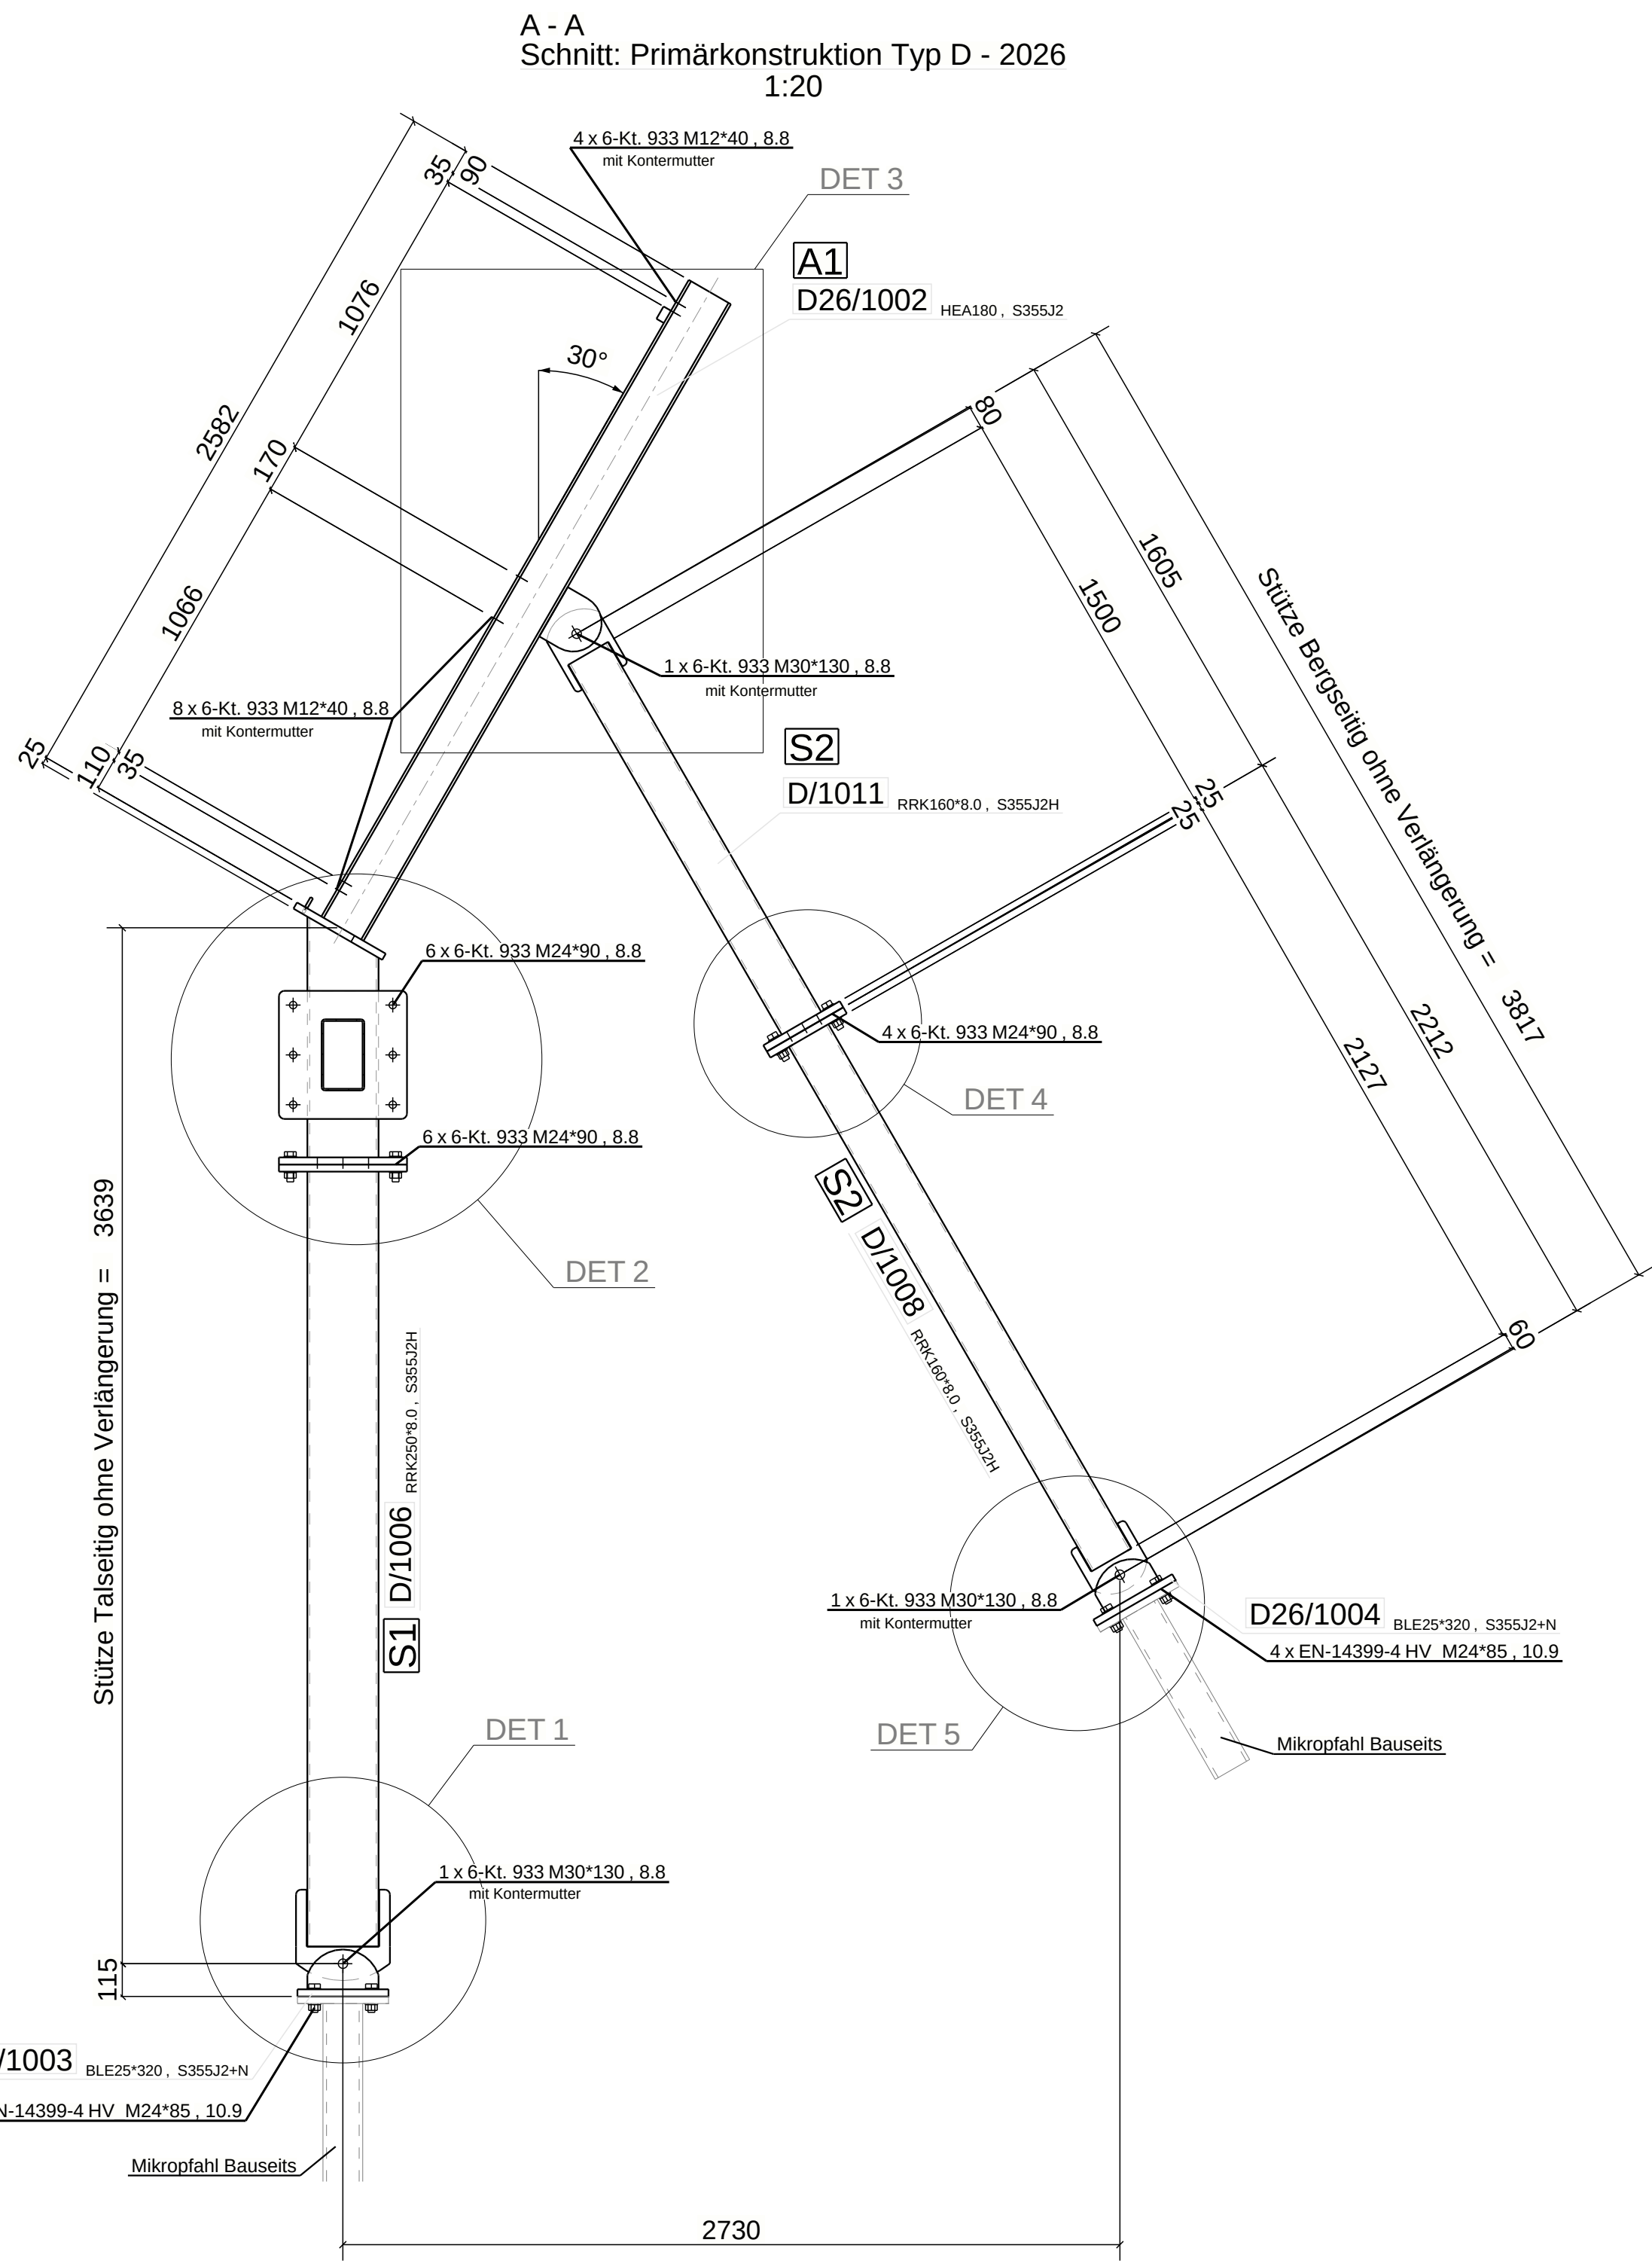


DETAIL 2, Schnitt D - D : talseitige Stütze (S1/S4)

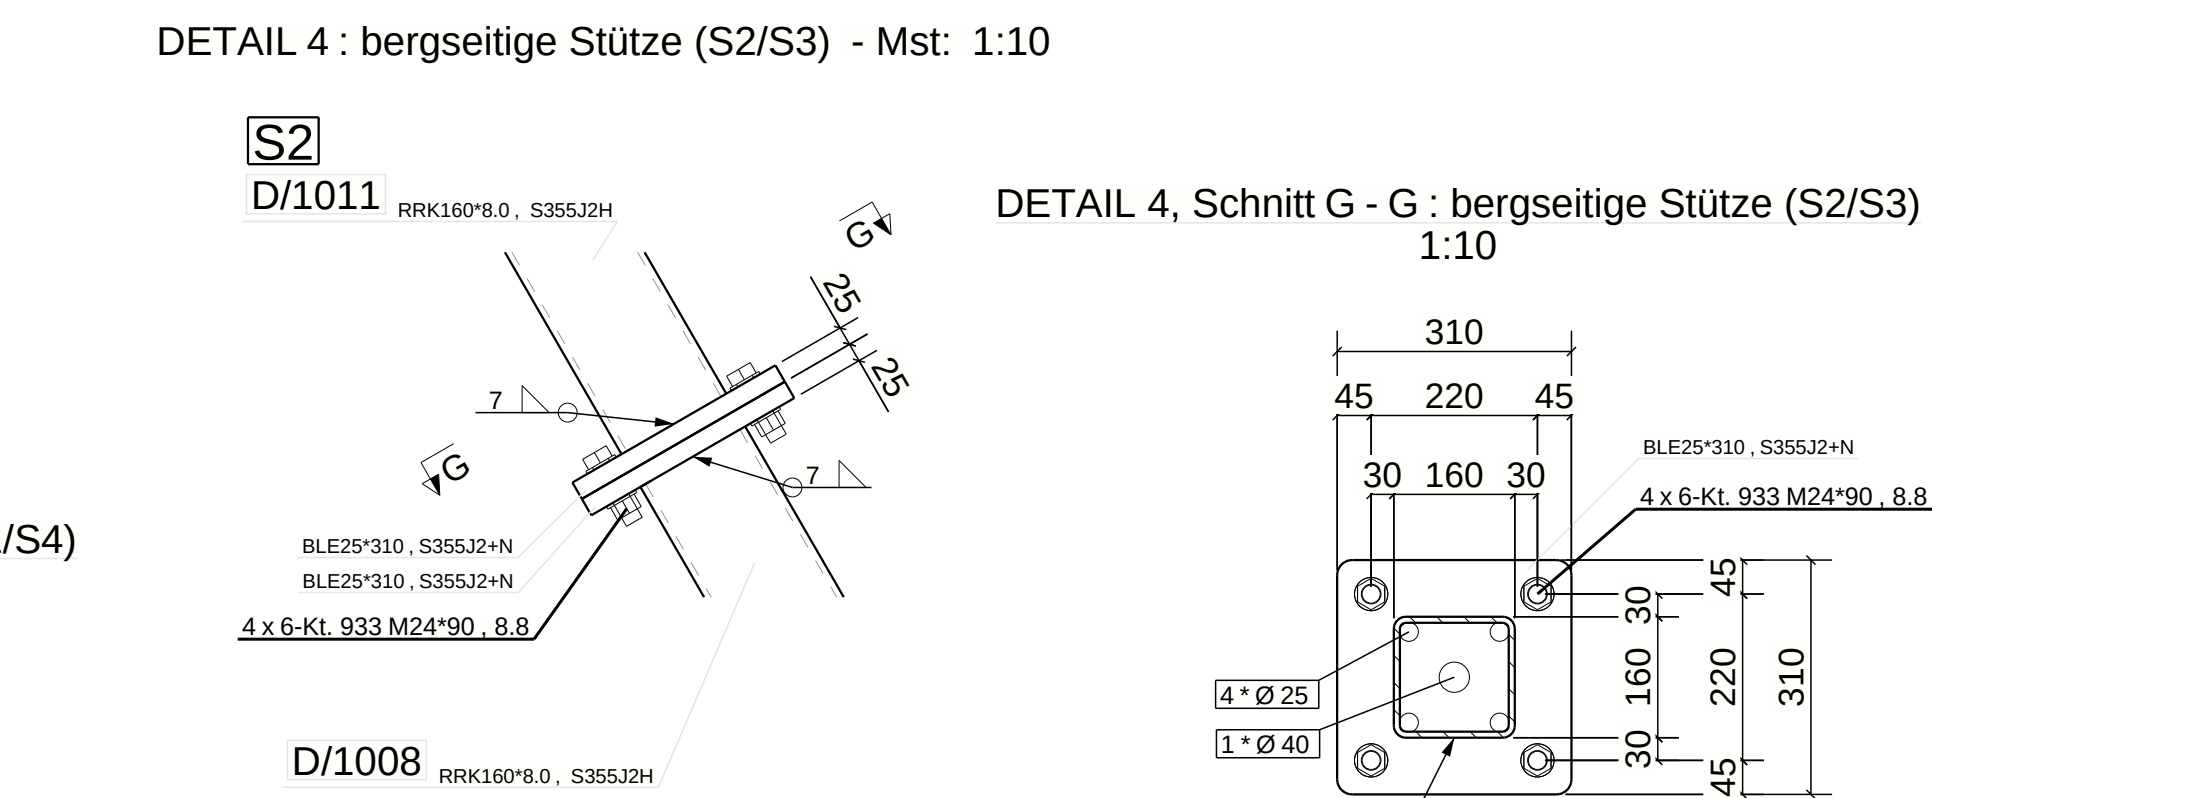



DETAIL 4, Schnitt G - G : bergseitige Stütze (S2/S3)

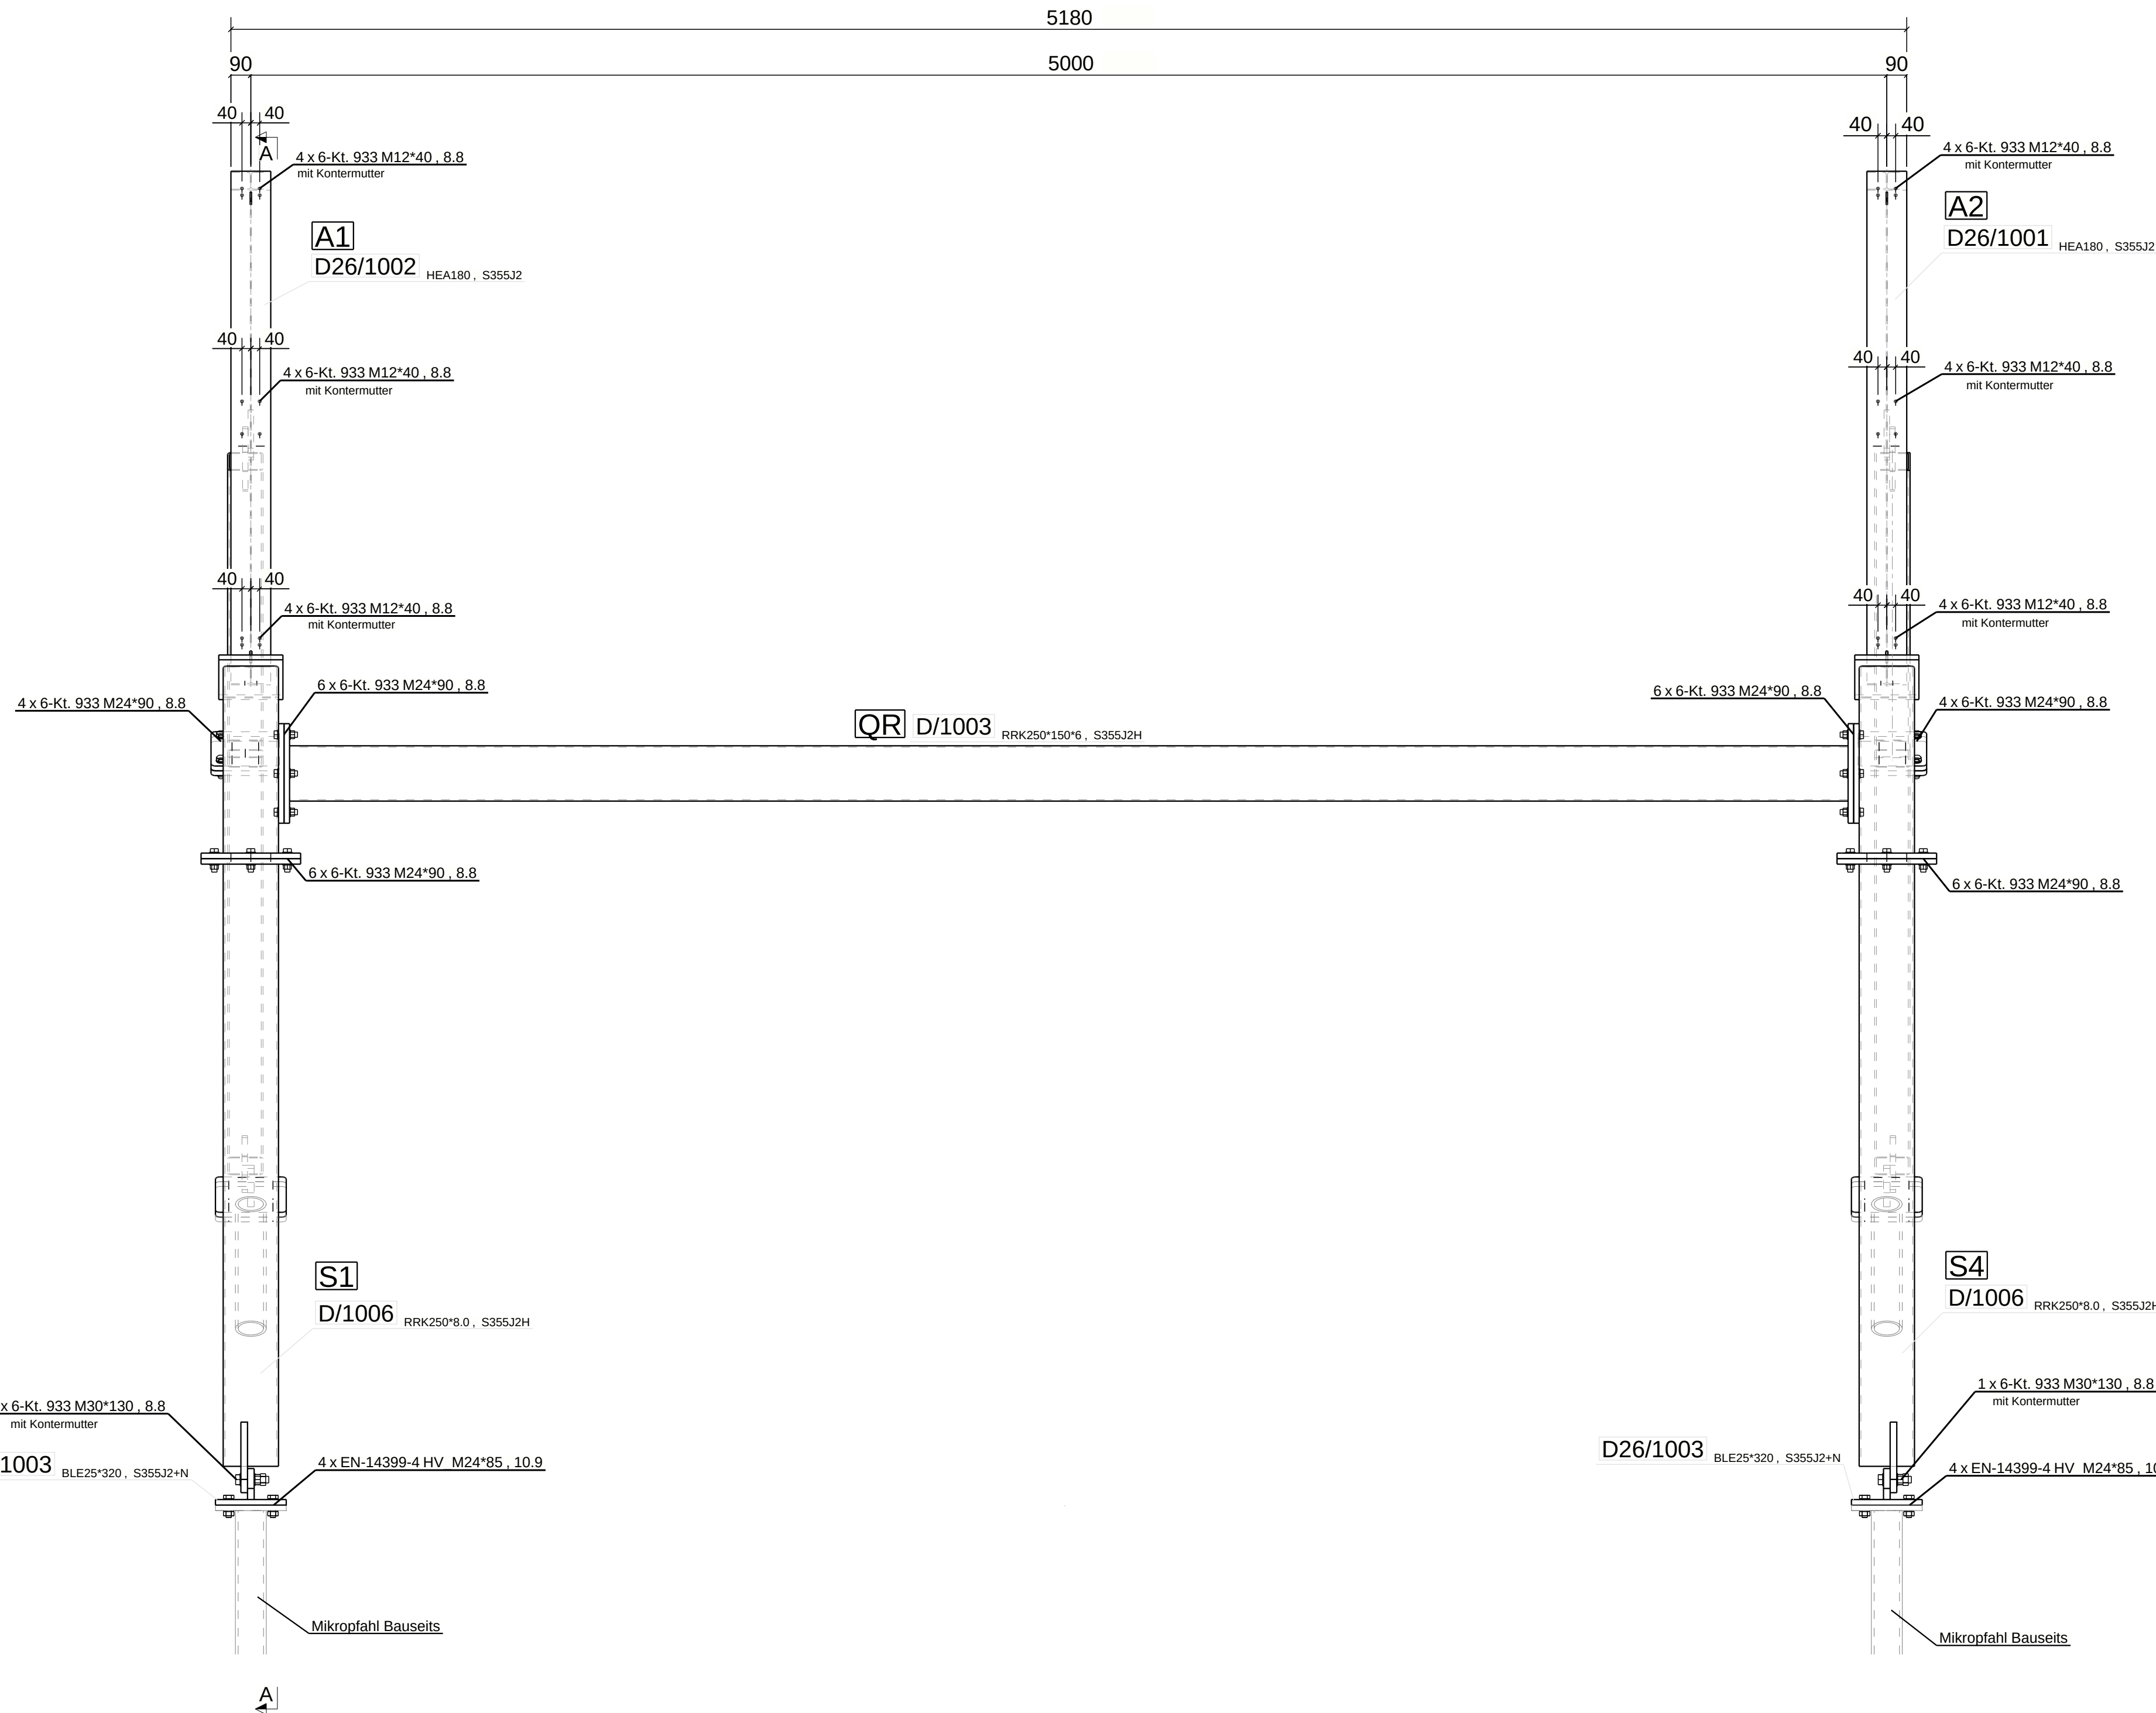


Ansicht: Primärkonstruktion Typ D - 2026
1:20

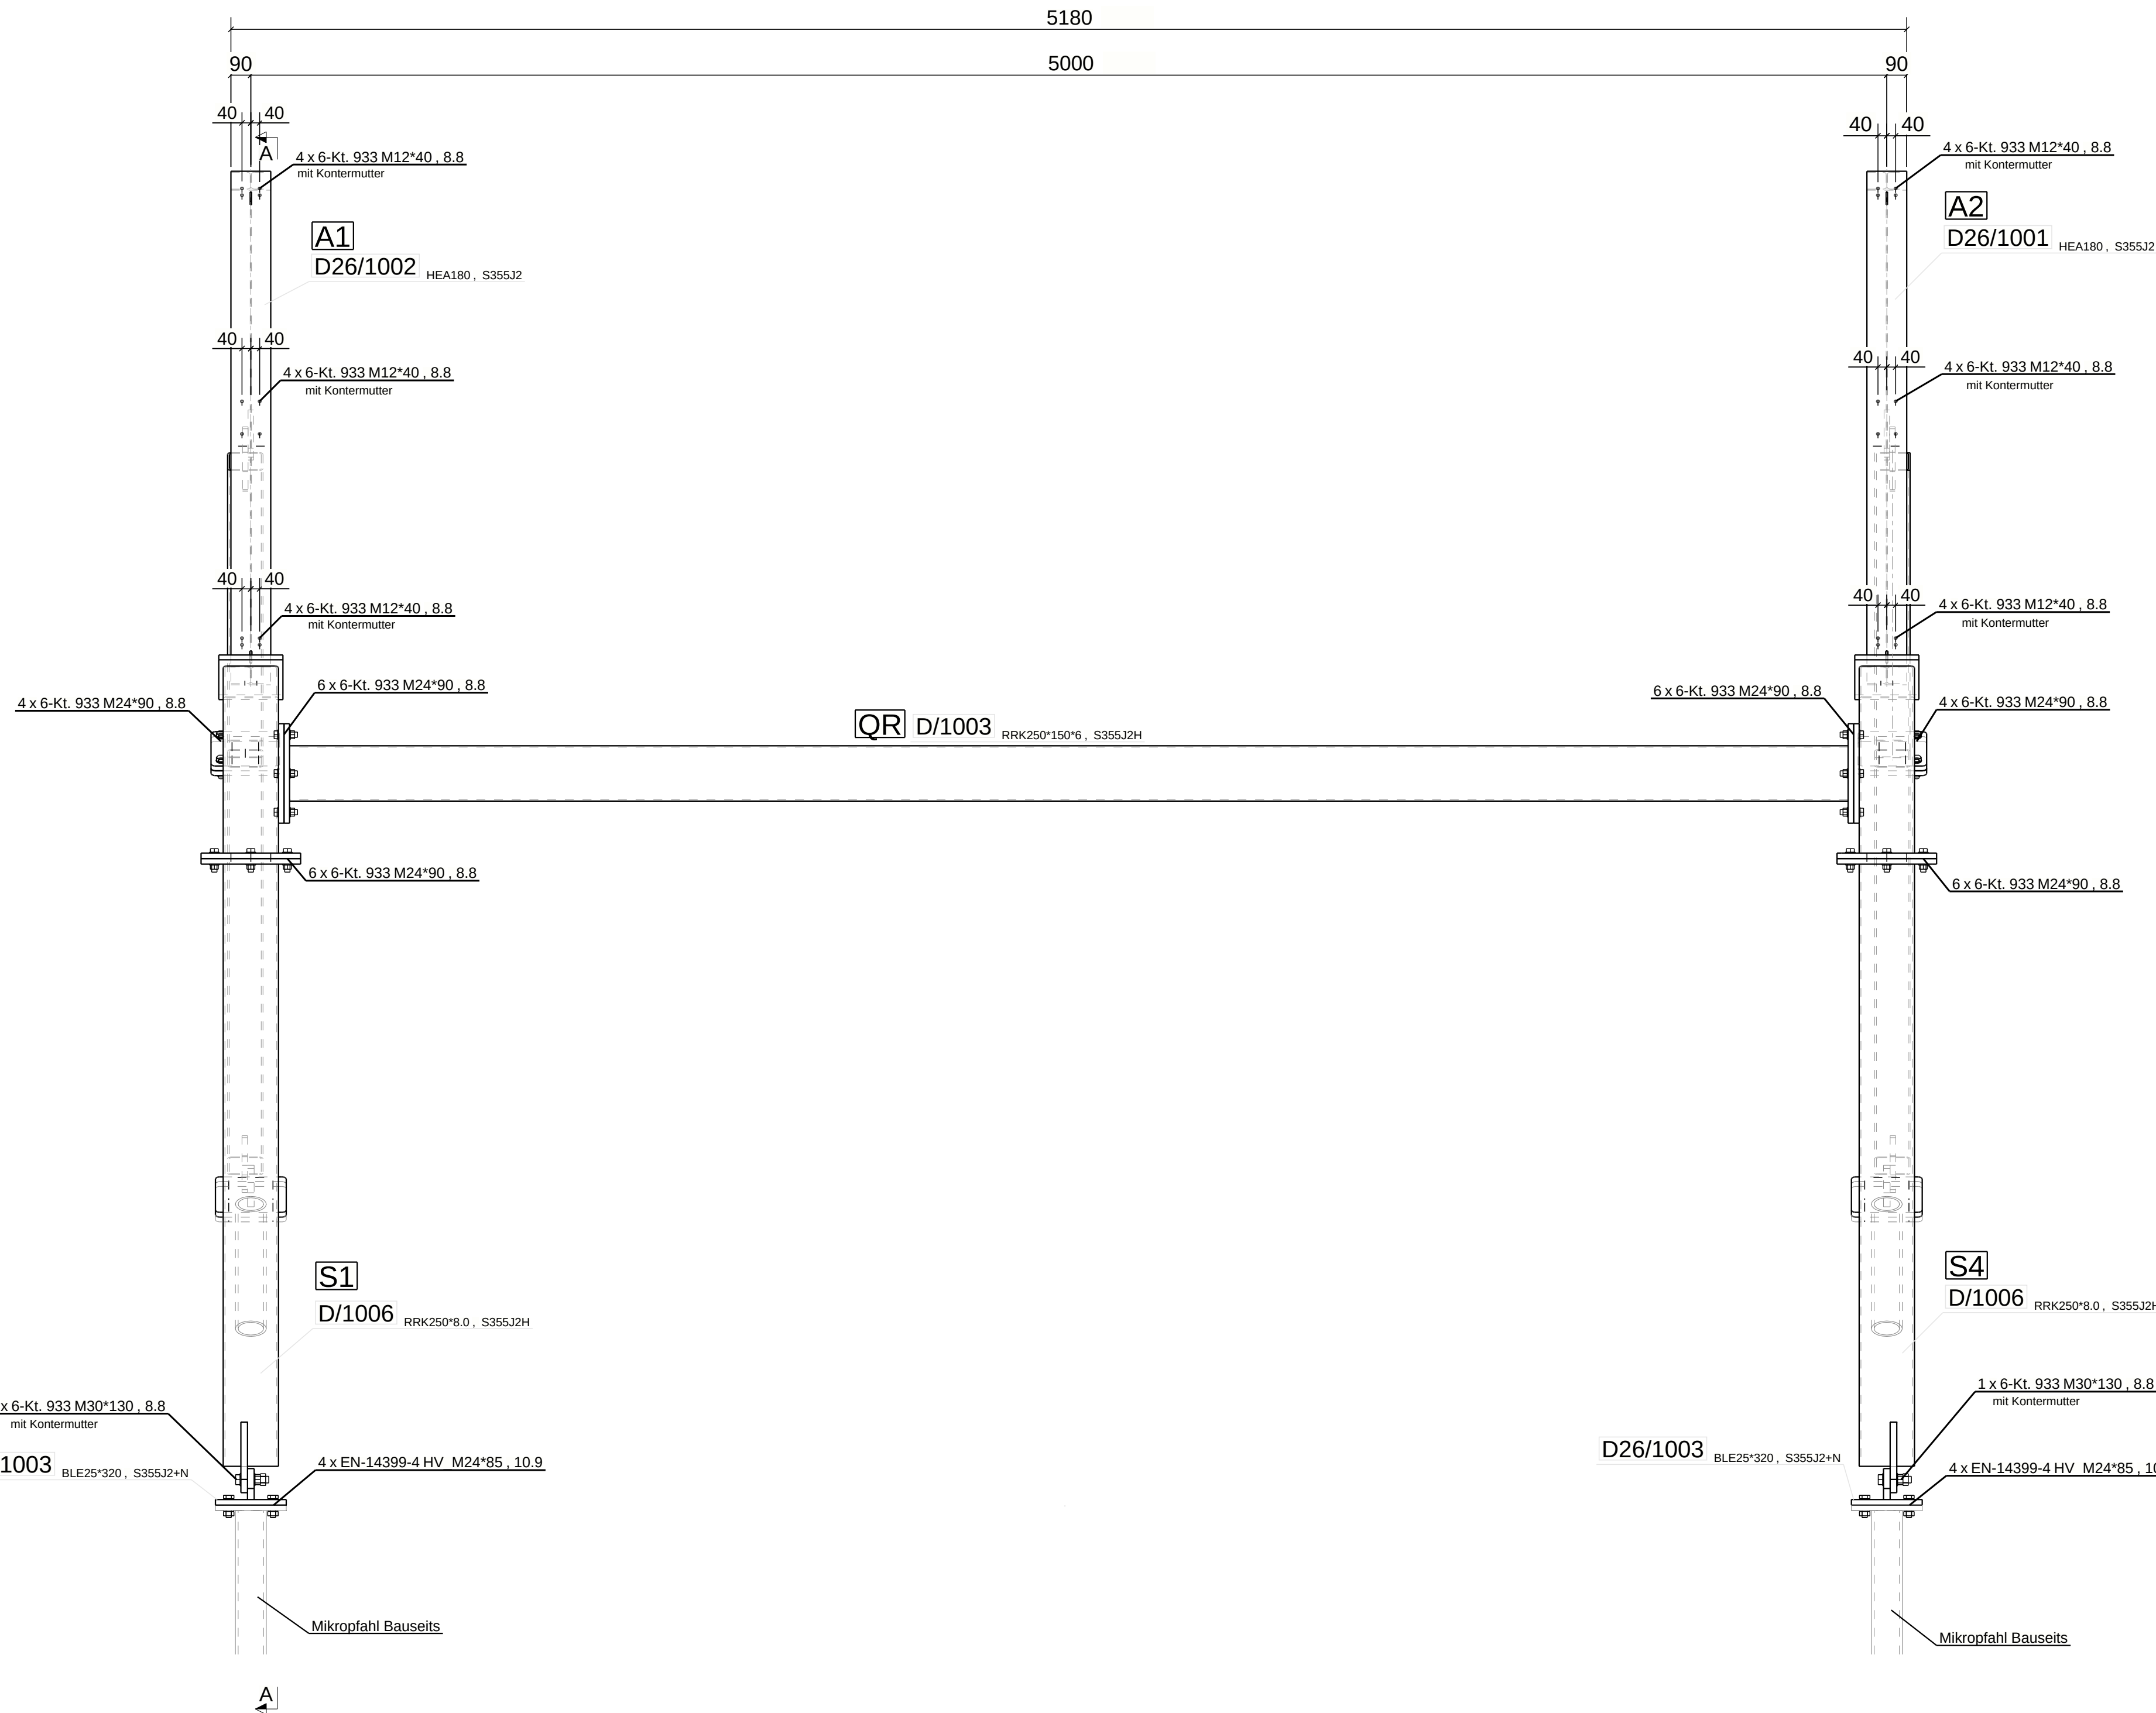


Isometrie Primärkonstruktion Typ D - 2026
1:55

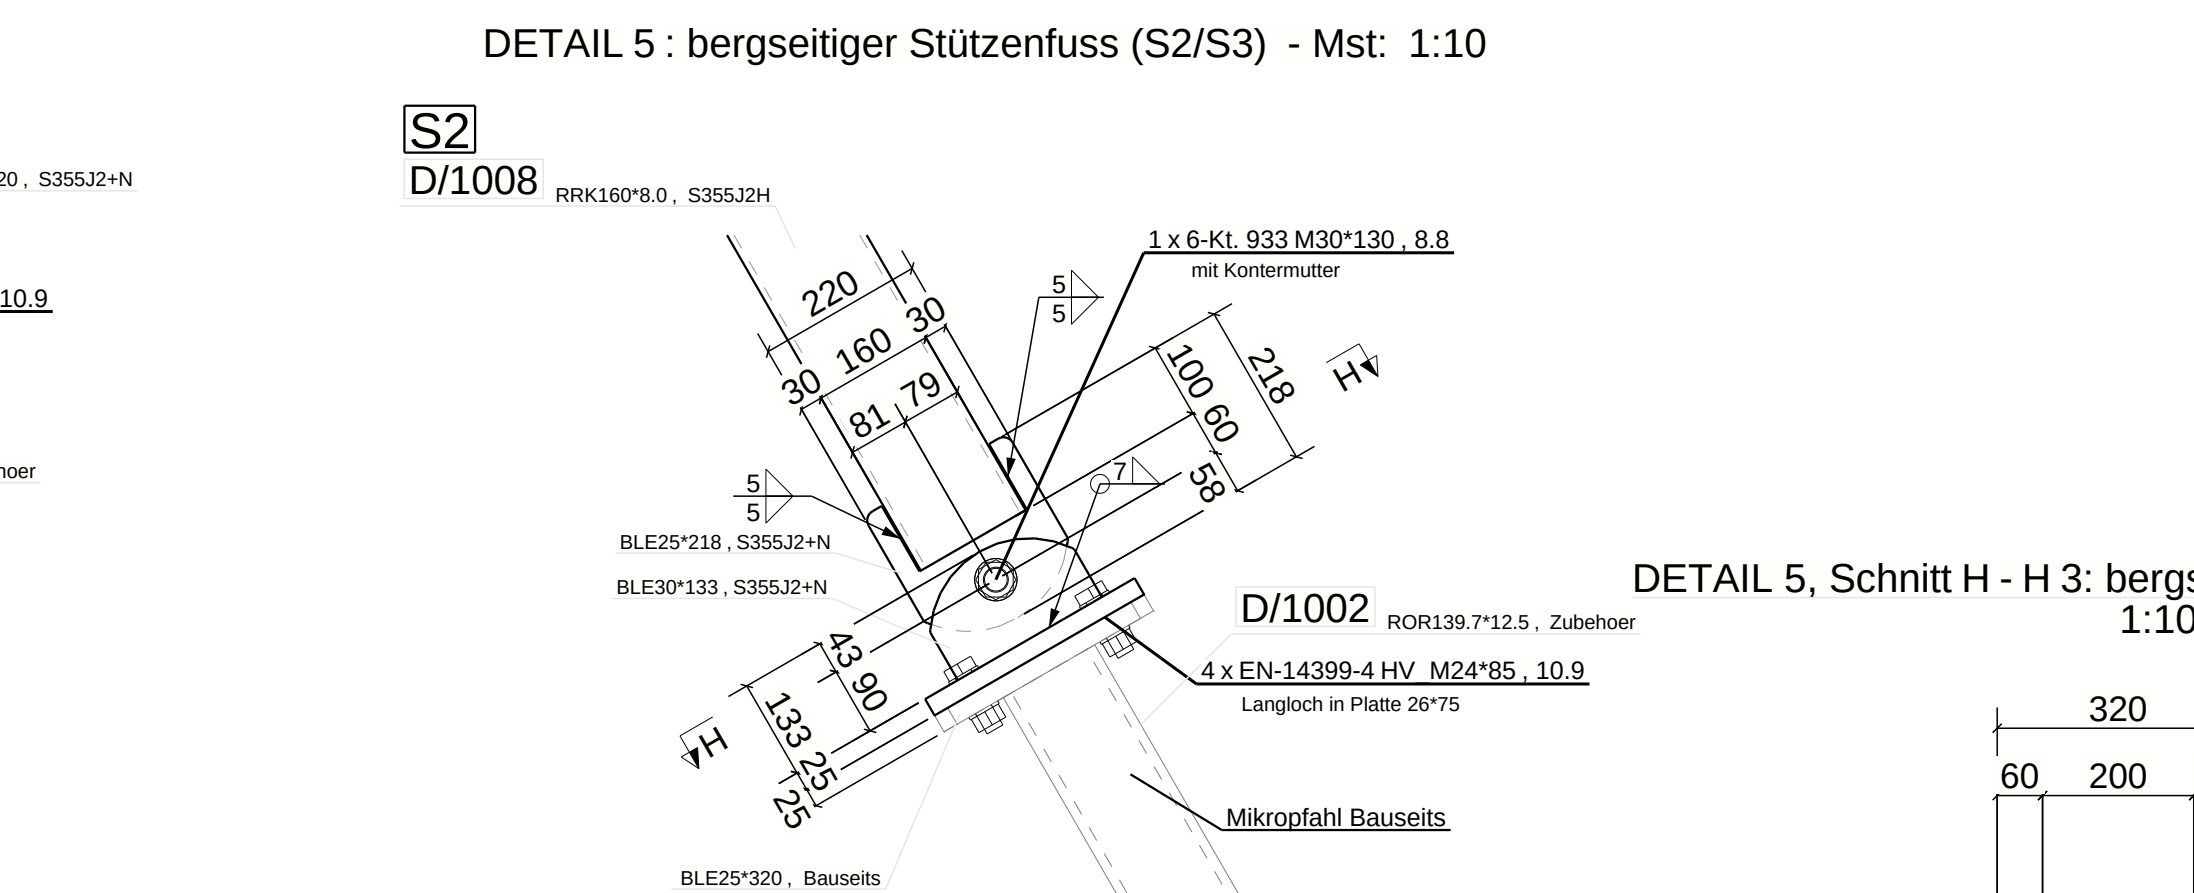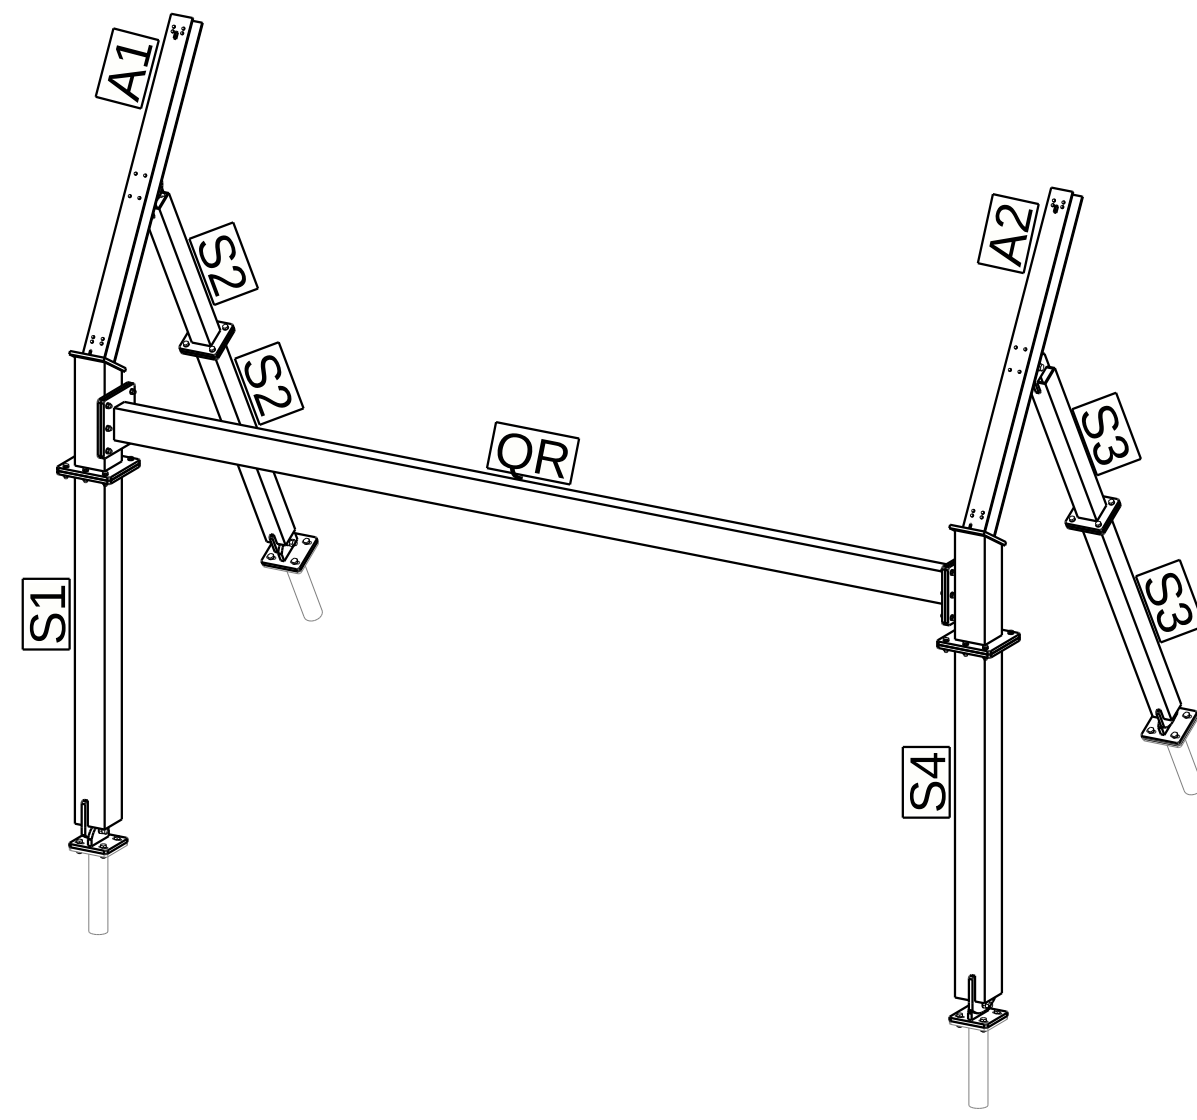


DETAIL 5, Schnitt H - H 3: bergseitiger Stützenfuss (S2/S3)

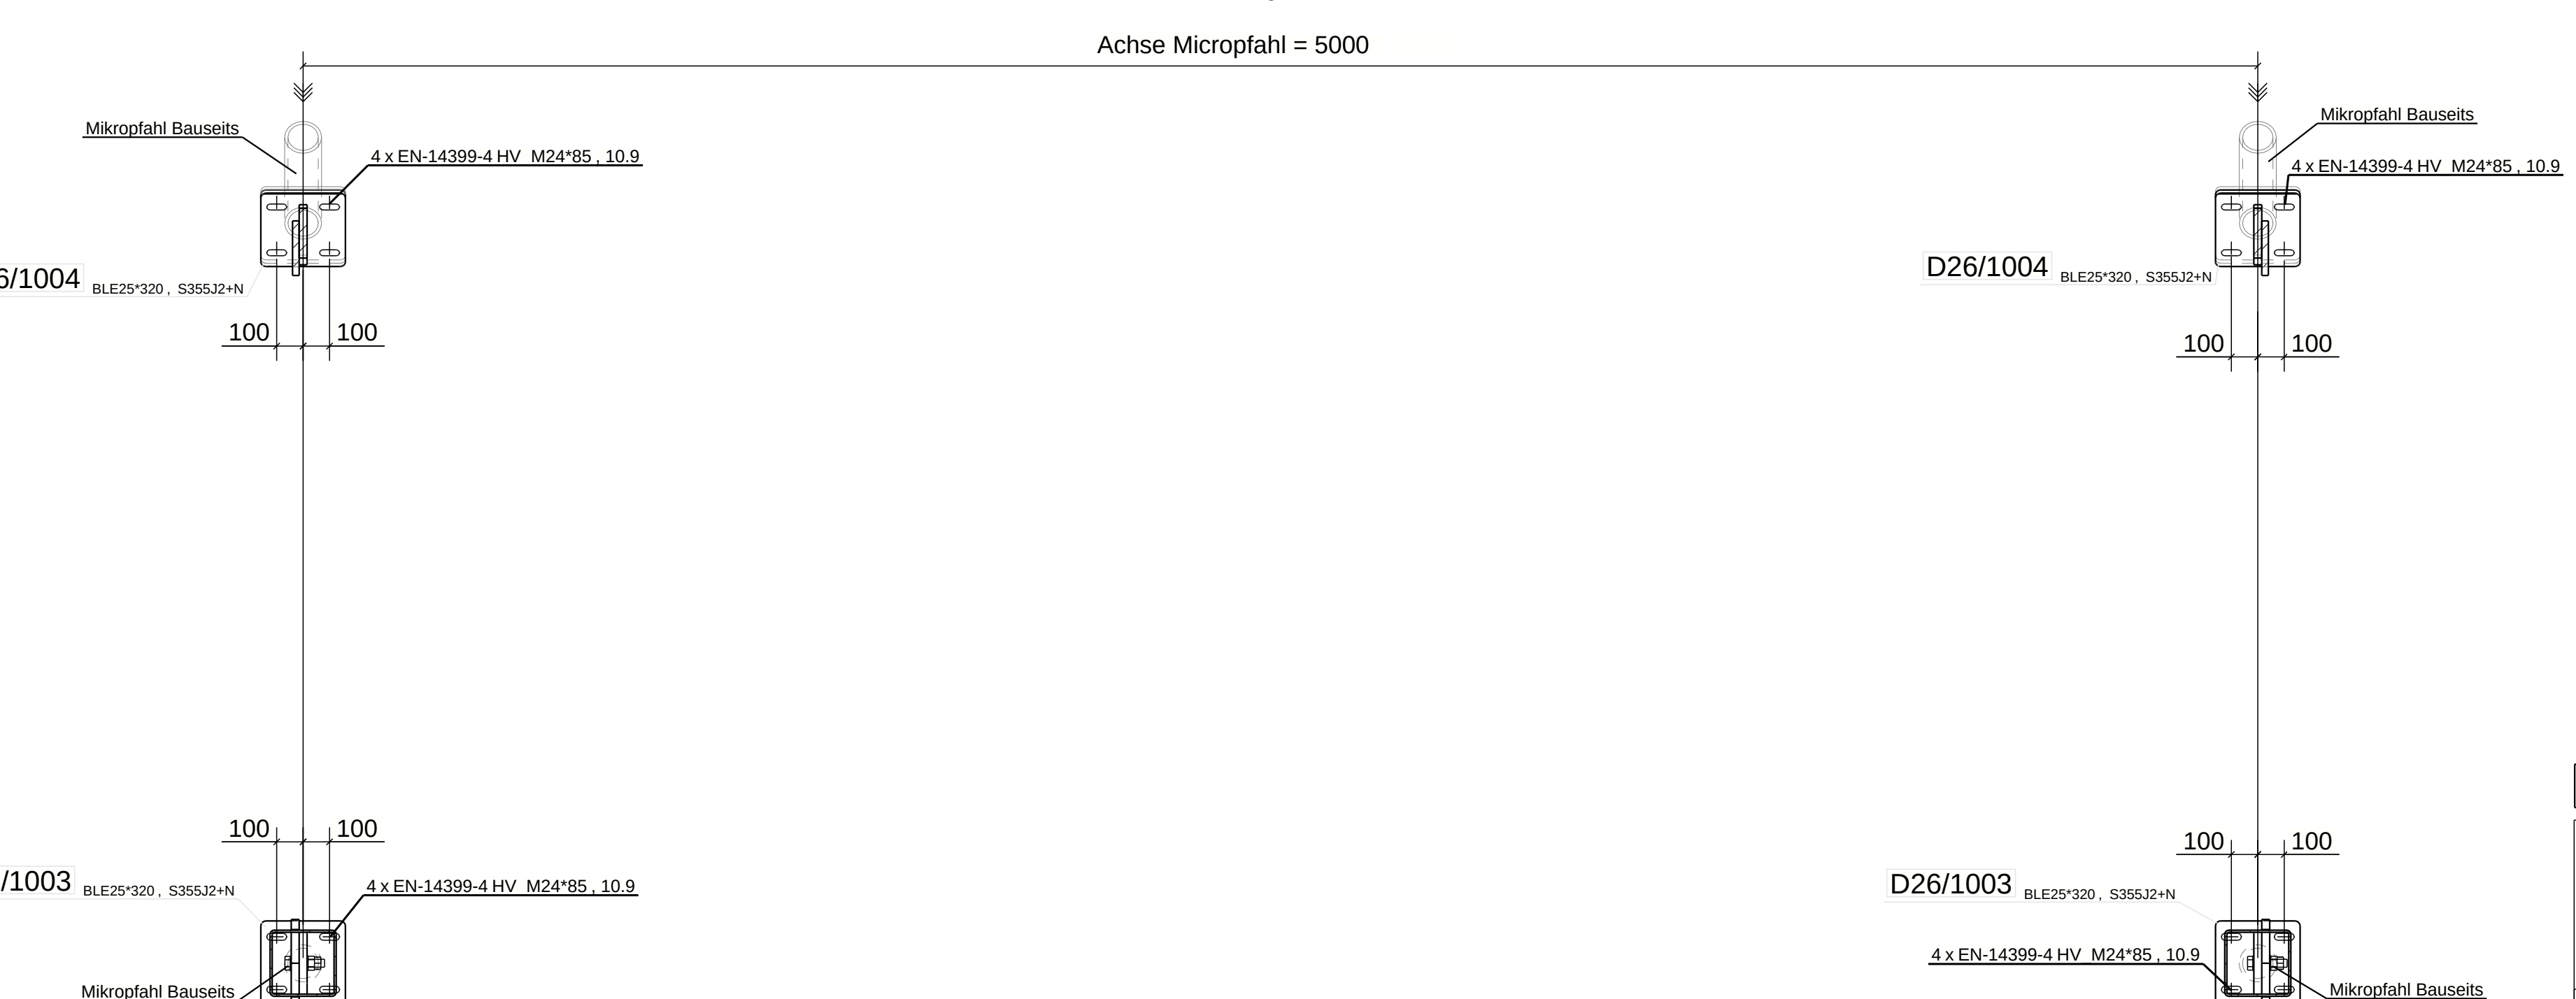


Grundriss: Primärkonstruktion Typ D - 2026
1:20

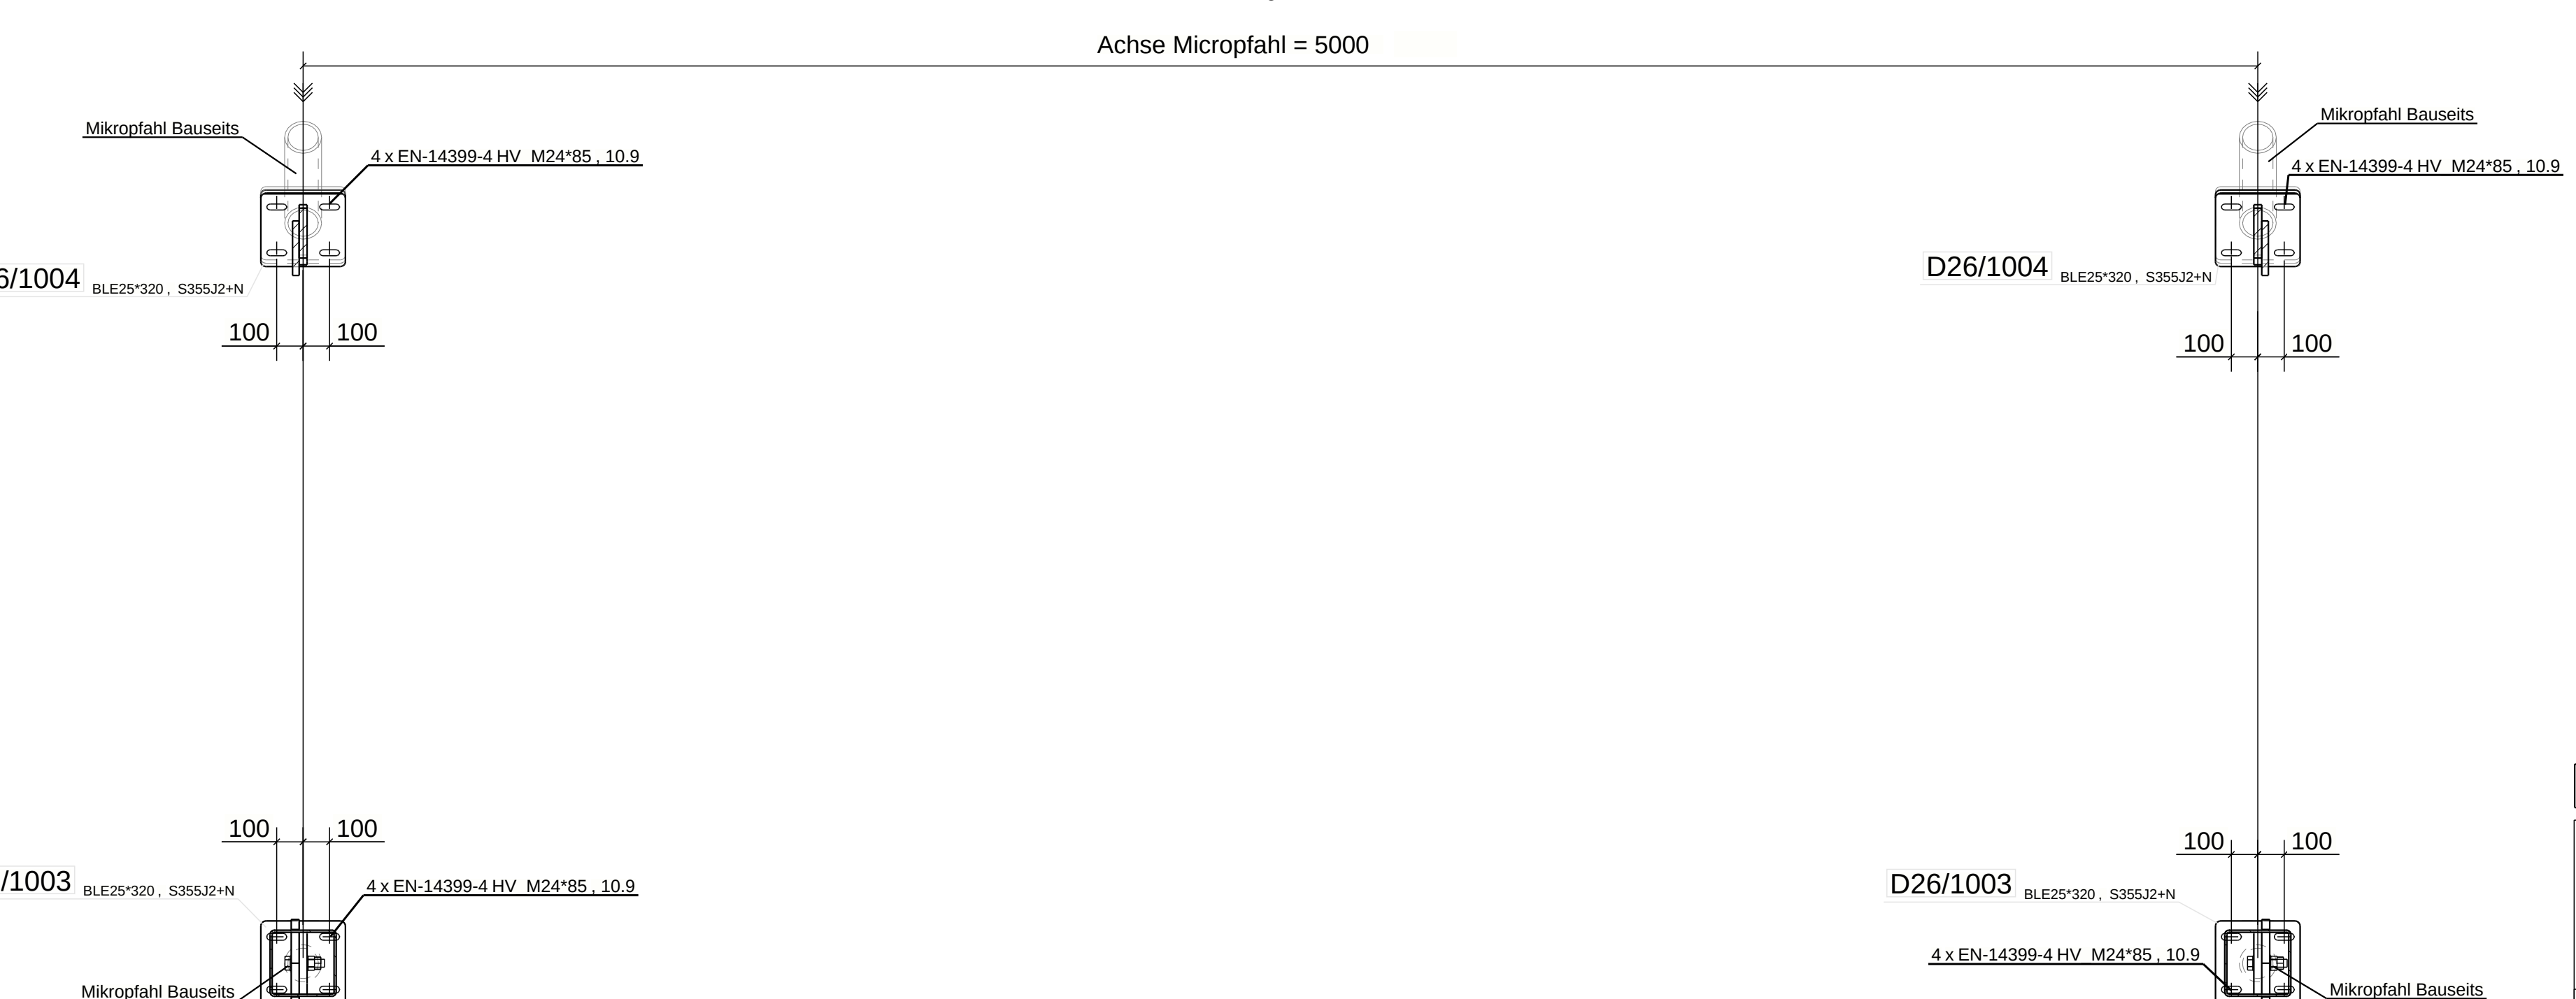

DETAIL 1. Schnitt B - B : talseitiger Stützenfuss (S1/S4)

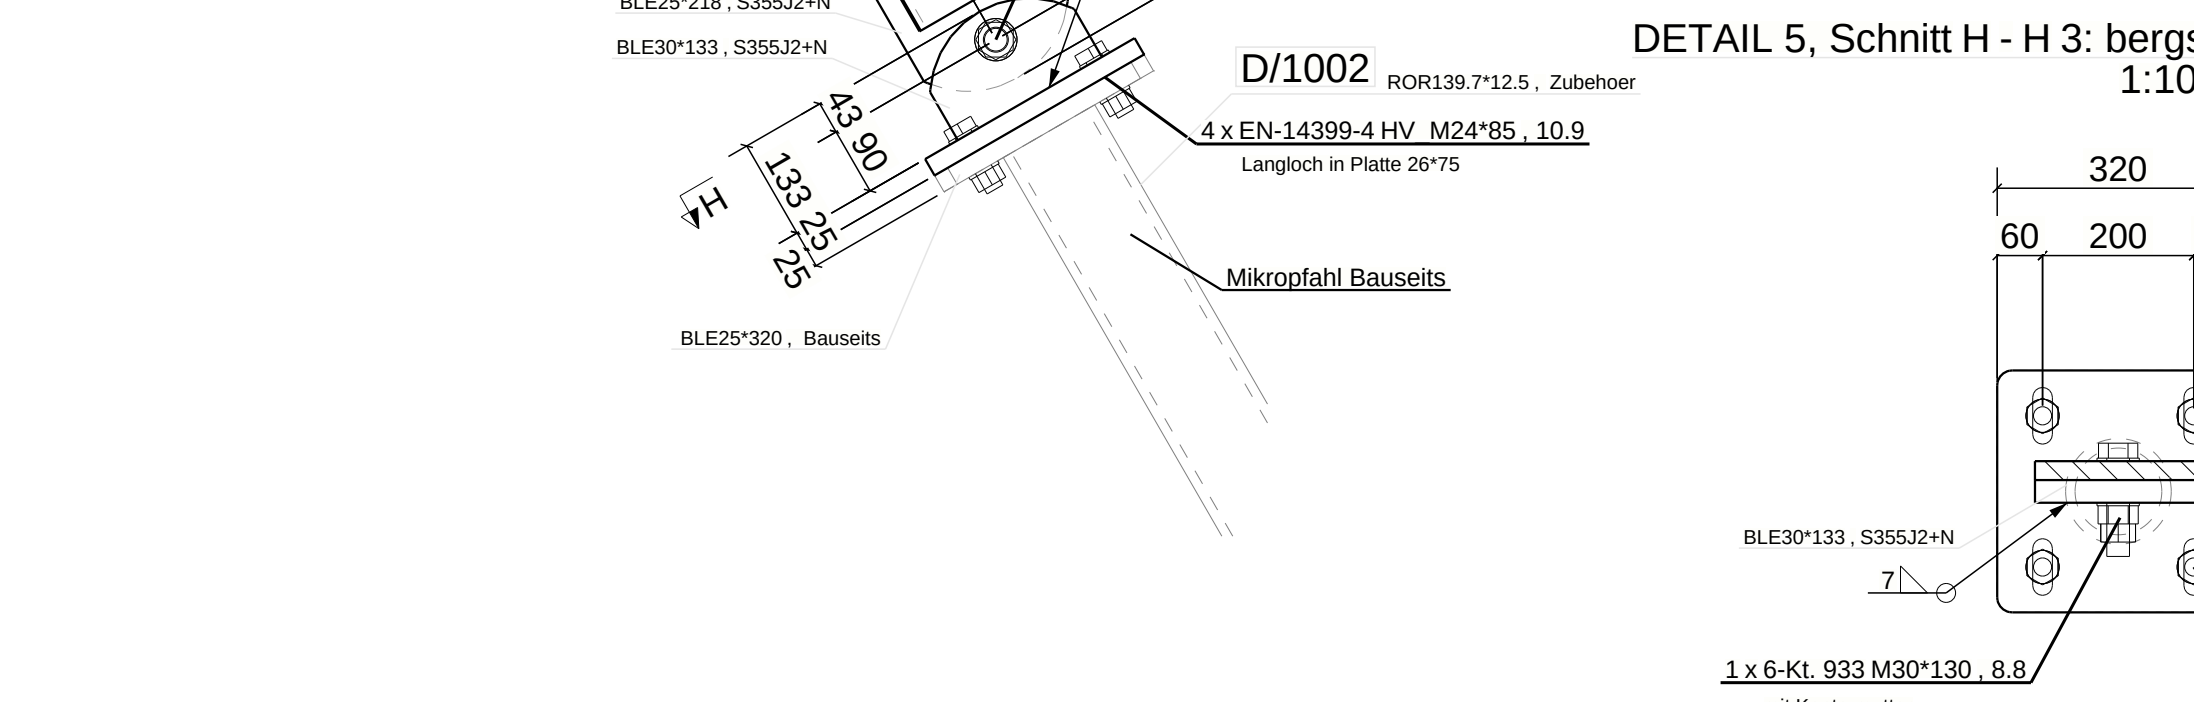

DETAIL 5, Schnitt H - H 3: bergseitiger Stützenfuss (S2/S3)

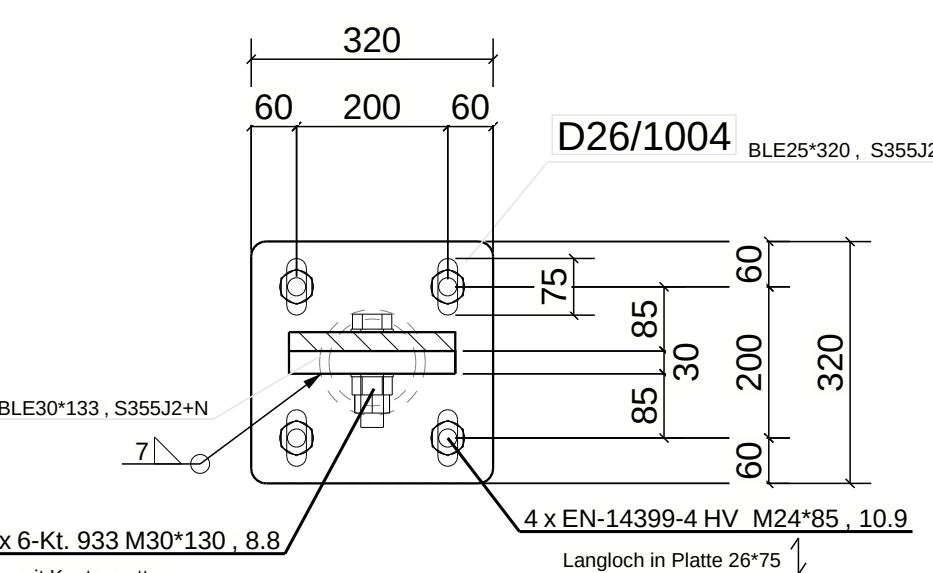[illegible]

Gesamte Konstruktion ist Roh

DINKE	DATUM		ANLEGENDE BEWEHRUNG		NACHTRÄGE
MAUCHLE Stahlbau					
Industriestrasse 9 · CH-6210 Sursee · T +41 41 925 12 51 - info@mauchle Stahlbau.ch					
Auftraggeber:	24027		Bauherr		
Zeichner:	P.Koch		Axpo Solutions AG		
	Interne Kontrolle		BAUSTELLE		
ABTEILUNG	UNTERSCHRIFT		NalpSolar		
			BENENNUNG		
			Primärkonstruktion Typ D		
			Typ 2026 - für 8er Modulstisch		
PL	J. Mäder		Ansicht, Schnitt & Details		
MASSTAB	1:10 1:20 1:55		ZEICHNUMMERNUMMER		
ANSICHT	 		24027 S O M 011		
			PROJEKT ABTEILUNG LOS FOLIOZUSAMMENHANG REVISION		